



Cut & Bend Rebar JOB ADVICE















工作通知

BBS No 钢筋加工表	<u>MVR-TT-H311</u>	Total Weight 总重量	<u>1,757</u>
Contract 合同号码		Total Pages Attached 统计页数	1+11
Customer 承包商	<u>WOH HUP PTE LTD</u>	Gate:	
Project Title 筑工地址	<u>MARINA VIEWLP 28F 1 STRAITS BIVD,SINGPORE 018906</u>		
Description 形容	L37层CJ4-2 梁		
Date Order 订单日期	24-Aug-2026	Date Required 交货日期	31-Aug-2026
Remarks 评论			
Check/Approved By 检查/审核/订货人	<u>Zhou Bing</u>	Handphone 手提电话	<u>9847 1699</u>
Site Contact Person 联络人	<u>Kumar</u>	Handphone 手提电话	<u>8133 8587</u>
Material Receiver 收货人	<u>SIVA</u>	Handphone 手提电话	<u>8426 2921</u>
Site Telephone 工地电话		Site Fax No 传真号码	
Scheduler 开料人	<u>Lu Yong Bing</u>	Handphone 手提电话	<u>8982 7022</u>
<u>***Please Allow 5 days for ??? To Process Your Order***</u>			
<u>51 Tuas South Street 5,Singapoer637644</u>			
Project Coodinator:	Leslie LIM	85242927	



PROJECT :	MARINA VIEWLP 28F 1 STRAITS BIVD,SINGAPORE 018906			Pg. 1 / 11
BBS No:	MVR-TT-H311	Rev.	Date : 2026/8/24	
Dwg. No.		Rev.	Prepared By:	
TITLE:	L37层CJ4-2 梁			BBS NO: MVR-TT-H311

BAR BENDING SCHEDULE

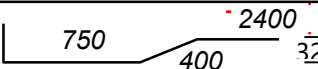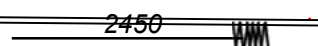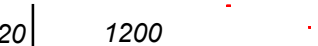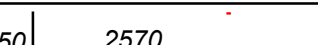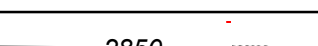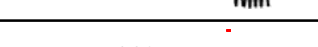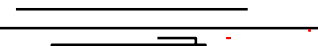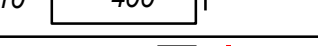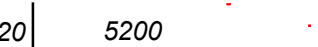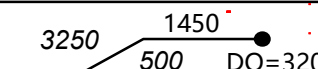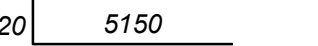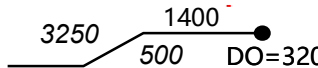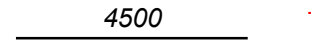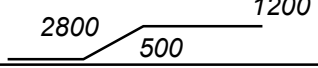MEMBER	BAR MARK	TYPE & SIZE	NO. OF MBRS	NO. OF EACH	TOTAL	SHAPE CODE	SHAPE	CUT OFF LENGTH	WEIGHT
					梁				
			RS-VB46 (200*500/425)				19#		
T1-1		H 32	1	2	2	92	350 	3900	49.24
T1-2		H 32	1	2	2		2450 		
T2		H 32	1	2	2	37	320 	1520	19.19
B1-1		H 32	1	2	2	37	350 	2920	36.87
B1-2		H 32	1	2	2		2850 		
隔铁		H 25	1	2	2	20	110 	110	0.85
L1		H 10	1	25	25	61	110 	1260	19.40
L2		H 10	1	9	9	61	110 	1110	6.15
			RS-VB45 (200*450)				20#		
T1		H 32	1	1	1	37	320 	5520	34.85
T1a		H 32	1	1	1	41		5520	34.85
T2		H 32	1	1	1	37	320 	5470	34.53
T2a		H 32	1	1	1	41		5470	34.53
B1		H 32	1	1	1	20	4500 	4500	28.41
B1a		H 32	1	1	1	41		4500	28.41

REBAR SIZE		R06	H08	H10	H13	H16	H20	H25	H32	H40	TOTAL
WEIGHT				25.6				0.8	300.9		327.3 KG



PROJECT :	MARINA VIEWLP 28F 1 STRAITS BIVD,SINGPORE 018906		Pg. 2 / 11
BBS No:	MVR-TT-H311	Rev.	Date : 2026/8/24
Dwg. No.		Rev.	Prepared By:
TITLE:	L37层CJ4-2 梁		BBS NO: MVR-TT-H311

BAR BENDING SCHEDULE

MEMBER	BAR MARK	TYPE & SIZE	NO. OF MBRS	NO. OF EACH	TOTAL	SHAPE CODE	SHAPE	CUT OFF LENGTH	WEIGHT
B2		H 32	1	1	1	20		4500	28.41
B2a		H 32	1	1	1	41		4500	28.41
L		H 10	1	21	21	61		1160	15.01
			RS-VB45-1/2 (200*300)				21#		
T1		H 20	1	2	2	38a		2800	13.81
B1		H 20	1	2	2	38a		2800	13.81
L		H 10	1	19	19	61		860	10.07
			RS-VB47-1/2 (200*300)				22#		
T1		H 16	1	2	2	38a		2800	8.84
B1		H 16	1	2	2	38a		2800	8.84
L		H 10	1	19	19	61		860	10.07
			RS-VB46a (200*300)				23#		
T1		H 20	1	2	2	38a		1860	9.17
B1		H 20	1	2	2	38a		1860	9.17
L		H 10	1	12	12	61		860	6.36

REBAR SIZE		R06	H08	H10	H13	H16	H20	H25	H32	H40	TOTAL
WEIGHT				41.5		17.7	46.0		56.8		162 KG



PROJECT :	MARINA VIEWLP 28F 1 STRAITS BIVD,SINGAPORE 018906		Pg. 3 / 11
BBS No:	MVR-TT-H311	Rev.	Date : 2026/8/24
Dwg. No.		Rev.	Prepared By:
TITLE:	L37层CJ4-2 梁		BBS NO: MVR-TT-H311

BAR BENDING SCHEDULE										
MEMBER	BAR MARK	TYPE & SIZE	NO. OF MBRS	NO.O F EACH	TOTAL	SHAP E CODE	SHAPE		CUT OFF LENGTH	WEIGHT
			RS-VB47 (240*450)					24#		
T1		H 25	1	2	2	37	300	3600	3900	30.06
T2		H 25	1	2	2	20	2100		2100	16.19
B1		H 25	1	2	2	37	300	3200	3500	26.98
B2		H 25	1	2	2	20	3000		3000	23.12
L		H 10	1	11	11	61	150	350	1240	8.40
隔铁		H 25	1	2	2	20	150		150	1.16
			RS-VB87 (285*1480)					25#		
T1		H 20	1	2	2	38	350	2250 1380	3980	19.63
T2		H 20	1	2	2	37	350	2150	2500	12.33
B1		H 16	1	2	2	37	300	1650	1950	6.16
B2		H 16	1	2	2	20	1600		1600	5.05
腰		H 13	2	6	12	20	1300		1300	16.26
隔铁		H 25	1	4	4	20	195		195	3.01
L		H 10	1	10	10	61	195	1390	3410	21.01

REBAR SIZE		R06	H08	H10	H13	H16	H20	H25	H32	H40	TOTAL
WEIGHT				29.4	16.3	11.2	32.0	100.5			189.3 KG
















PROJECT :	MARINA VIEWLP 28F 1 STRAITS BIVD,SINGPORE 018906			Pg. 4 / 11
BBS No:	MVR-TT-H311	Rev.	Date : 2026/8/24	
Dwg. No.		Rev.	Prepared By:	
TITLE:	L37层CJ4-2 梁			BBS NO: MVR-TT-H311

BAR BENDING SCHEDULE										
MEMBER	BAR MARK	TYPE & SIZE	NO. OF MBRS	NO. OF EACH	TOTAL	SHAPE CODE	SHAPE		CUT OFF LENGTH	WEIGHT
				RCB-A (225*500)			26#			
T1		H 16	1	2	2	37	400	2250	2650	8.37
B1		H 13	1	2	2	37	250	1750	2000	4.17
				RS-VB51 (225*450)			27#			
T1		H 20	1	2	2	20	3650		3650	18.00
B1		H 20	1	2	2	20	3650		3650	18.00
L		H 10	1	12	12	61	140	350	1220	9.02
				RS-VB86 (285*1480)			28#			
T1		H 20	1	2	2	38	350	2250	1380	19.63
T2		H 20	1	2	2	37	350	2150	2500	12.33
B1		H 16	1	2	2	37	300	1650	1950	6.16
B2		H 16	1	2	2	20	1600		1600	5.05
腰		H 13	2	6	12	20	1300		1300	16.26
隔铁		H 25	1	4	4	20	195		195	3.01
L		H 10	1	10	10	61	195	1390	3410	21.01

REBAR SIZE		R06	H8	H10	H13	H16	H20	H25	H32	H40	TOTAL
WEIGHT				30.0	20.4	19.6	68.0	3.0			141 KG



PROJECT :	MARINA VIEWLP 28F 1 STRAITS BIVD,SINGAPORE 018906			Pg. 5 / 11
BBS No:	MVR-TT-H311	Rev.	Date : 2026/8/24	
Dwg. No.		Rev.	Prepared By:	
TITLE:	L37层CJ4-2 梁			BBS NO: MVR-TT-H311

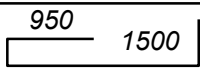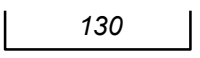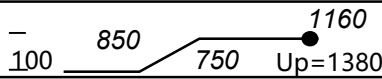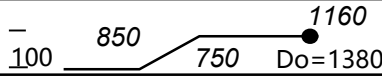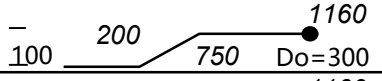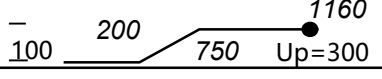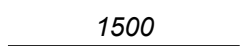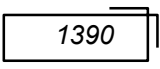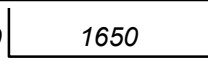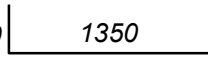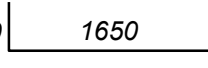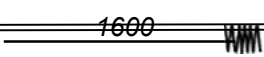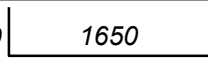BAR BENDING SCHEDULE										
MEMBER	BAR MARK	TYPE & SIZE	NO. OF MBRS	NO. OF EACH	TOTAL	SHAPE CODE	SHAPE	CUT OFF LENGTH	WEIGHT	
			RC CORBEL (210*212*665)					29#		
主筋		H 20	1	2	2	52	565 	3265	16.10	
U-Bar		H 13	1	6	6	38a	950 	2030	12.69	
			RS-VB85 (240*1480)					30#		
T1		H 20	1	1	1	41		4140	10.21	
T1a		H 20	1	1	1	41		4140	10.21	
B1		H 20	1	1	1	41		2410	5.94	
B1a		H 20	1	1	1	41		2410	5.94	
腰		H 13	2	6	12	20		1500	18.76	
L		H 10	1	12	12	61	180 	3380	24.98	
			RS-HB23-3 (400/280*400)					31#		
T1		H 20	1	3	3	37	250 	1900	14.06	
T1a		H 20	1	1	1	37	250 	1600	3.95	
T1b		H 20	1	1	1	37	250 	1900	4.69	
T1c		H 20	1	4	4		1600 	1600		
B1		H 20	1	3	3	37	250 	1900	14.06	

REBAR SIZE		R06	H08	H10	H13	H16	H20	H25	H32	H40	TOTAL
WEIGHT				25.0	31.4		85.2				141.6 KG



PROJECT :	MARINA VIEWLP 28F 1 STRAITS BIVD,SINGAPORE 018906			Pg. 6 / 11
BBS No:	MVR-TT-H311	Rev.	Date : 2026/8/24	
Dwg. No.		Rev.	Prepared By:	
TITLE:	L37层CJ4-2 梁			BBS NO: MVR-TT-H311

BAR BENDING SCHEDULE

MEMBER	BAR MARK	TYPE & SIZE	NO. OF MBRS	NO. OF EACH	TOTAL	SHAPE CODE	SHAPE	CUT OFF LENGTH	WEIGHT
B1a		H 20	1	1	1	37	250 1350	1600	3.95
B1b		H 20	1	1	1	37	250 1250	1500	3.70
B1c		H 20	1	4	4		1150	1150	
L1		H 10	1	7	7	61	300 310	1460	6.30
L2		H 10	1	1	1	61	300 190	1220	0.75
			RS-HB26a (200*500)				32#		
T1		H 20	1	2	2	38a	250 2900 250	3400	16.77
B1-1		H 20	1	2	2	37	250 2750	3000	14.80
B1-2		H 20	1	2	2	37	250 1300	1550	7.64
L		H 10	1	14	14	61	110 400	1260	10.87
洞加		H 13	2	2	4	61	130 400	1372	5.72
	T/B	H 16	2	2	4	37	450 1000	1450	9.16
			RS-HB27 (200*500)				33#		
T1		H 20	1	2	2	38a	250 1920 250	2420	11.94
B1		H 20	1	2	2	38a	250 1920 250	2420	11.94
L		H 10	1	9	9	61	110 400	1260	6.99

REBAR SIZE		R06	H08	H10	H13	H16	H20	H25	H32	H40	TOTAL
WEIGHT				24.9	5.7	9.2	70.7				110.5 KG



PROJECT :	MARINA VIEWLP 28F 1 STRAITS BIVD,SINGAPORE 018906			Pg. 7 / 11
BBS No:	MVR-TT-H311	Rev.	Date : 2026/8/24	
Dwg. No.		Rev.	Prepared By:	
TITLE:	L37层CJ4-2 梁			BBS NO: MVR-TT-H311

BAR BENDING SCHEDULE										
MEMBER	BAR MARK	TYPE & SIZE	NO. OF MBRS	NO. OF EACH	TOTAL	SHAPE CODE	SHAPE		CUT OFF LENGTH	WEIGHT
			RS-HB28 (200*500)				34#			
T1		H 20	1	2	2	38a	250	2200	250	2700 13.32
B1		H 20	1	2	2	38a	250	2200	250	2700 13.32
L		H 10	1	10	10	61	110	400		1260 7.76
			RS-HB29 (200*500)				35#			
T1-1		H 20	1	2	2	37	250	1730		1980 9.77
T1-2		H 20	1	2	2			1600		
B1-1		H 20	1	2	2	37	250	1730		1980 9.77
B1-2		H 20	1	2	2			1150		
L		H 10	1	9	9	61	110	400		1260 6.99
			RS-HB26b (200*500)				36#			
T1		H 16	1	2	2	38a	200	2900	200	3300 10.42
B1-1		H 16	1	2	2	37	200	2750		2950 9.32
B1-2		H 16	1	2	2	37	200	1100		1300 4.11
L		H 10	1	14	14	61	110	400		1260 10.87
洞加		H 13	2	2	4	61	130	400		1372 5.72

REBAR SIZE		R06	H08	H10	H13	H16	H20	H25	H32	H40	TOTAL
WEIGHT				25.6	5.7	23.8	46.2				101.3 KG



PROJECT :				Pg. 8 / 11
BBS No:	MVR-TT-H311	Rev.	Date :	
Dwg. No.		Rev.	Prepared By:	
TITLE:	L37层CJ4-2 梁			BBS NO: MVR-TT-H311

BAR BENDING SCHEDULE

MEMBER	BAR MARK	TYPE & SIZE	NO. OF MBRS	NO. OF EACH	TOTAL	SHAPE CODE	SHAPE	CUT OFF LENGTH	WEIGHT
	T/B	H 16	2	2	4	37	450 1000	1450	9.16
			RS-HB26c (200*300)				37#		
T1		H 20	1	2	2	38a	200 2930 200	3330	16.42
B1-1		H 20	1	2	2	37	200 2750	2950	14.55
B1-2		H 20	1	2	2	37	200 1300	1500	7.40
L		H 10	1	26	26	61	110 200	860	13.77
			RS-HB34 (200*665/430)				38#		
T1		H 20	1	2	2	38a	250 3030 250	3530	17.41
B1-1		H 20	1	2	2		550 450 2450 250	3700	18.25
B1-2		H 20	1	2	2	37	250 1350	1600	7.89
L1		H 10	1	12	12	61	110 565	1590	11.75
L2		H 10	1	2	2	61	110 330	1120	1.38

REBAR SIZE		R06	H08	H10	H13	H16	H20	H25	H32	H40	TOTAL
WEIGHT				26.9		9.2	81.9				118 KG



PROJECT :				Pg. 9 / 11
BBS No:	MVR-TT-H311	Rev.	Date :	
Dwg. No.		Rev.	Prepared By:	
TITLE:	L37层CJ4-2 梁			BBS NO: MVR-TT-H311

BAR BENDING SCHEDULE

MEMBER	BAR MARK	TYPE & SIZE	NO. OF MBRS	NO. OF EACH	TOTAL	SHAPE CODE	SHAPE	CUT OFF LENGTH	WEIGHT
			RS-HB35/36 (200*480)				39#		
T1		H 32	1	2	2	38a	320 5700 320	6340	80.05
B1-1		H 32	1	2	2	37	320 5470	5790	73.10
B1-2		H 32	1	2	2	37	320 2000	2320	29.29
B2		H 32	1	2	2	20	4850	4850	61.24
隔铁		H 25	1	4	4	20	110	110	1.70
L		H 10	1	26	26	61	110 380	1220	19.54
			RS-HB37 (200*430/665)				40#		
T1		H 16	1	2	2	38a	200 3030 200	3430	10.83
B1-1		H 16	1	2	2	37	200 1250	1450	4.58
B1-2		H 16	1	2	2		450 450 2450 200	3550	11.21
L1		H 10	1	2	2	61	110 330	1120	1.38
L2		H 10	1	12	12	61	110 565	1590	11.75
			RS-HB38 (200*665)				41#		
T1		H 16	1	2	2	38a	200 2800 200	3200	10.11
B1		H 16	1	2	2	38a	200 2800 200	3200	10.11

REBAR SIZE		R06	H08	H10	H13	H16	H20	H25	H32	H40	TOTAL
WEIGHT				32.7		46.8		1.7	243.7		324.9 KG



PROJECT :				Pg. 10 / 11
BBS No:	MVR-TT-H311	Rev.	Date :	
Dwg. No.		Rev.	Prepared By:	
TITLE:	L37层CJ4-2 梁			BBS NO: MVR-TT-H311

BAR BENDING SCHEDULE

MEMBER	BAR MARK	TYPE & SIZE	NO. OF MBRS	NO. OF EACH	TOTAL	SHAPE CODE	SHAPE	CUT OFF LENGTH	WEIGHT
L		H 10	1	13	13	61	110	1590	12.73
			RS-HB39 (200*665/430)					42#	
T1		H 16	1	2	2	38a	200	3120	9.85
B1-1		H 16	1	2	2		450	3250	10.26
B1-2		H 16	1	2	2	37	200	1450	4.58
L1		H 10	1	11	11	61	110	1590	10.77
L2		H 10	1	2	2	61	110	1120	1.38
			RS-HB40 (200*480)					43#	
T1		H 20	1	2	2	37	300	3160	15.59
B1		H 20	1	2	2	37	250	3110	15.34
L		H 10	1	13	13	61	110	1220	9.77
			LB11 (150*200)				44#		
T1		H 13	1	2	2	38a	130	1210	2.52
B1		H 16	1	2	2	38a	130	1210	3.82
L		H 08	1	6	6	61	90	632	1.50


REBAR SIZE		R06	H08	H10	H13	H16	H20	H25	H32	H40	TOTAL
WEIGHT			1.5	34.7	2.5	28.5	30.9				98.1 KG



PROJECT :				Pg. 11 / 11
BBS No:	MVR-TT-H311	Rev.	Date :	
Dwg. No.		Rev.	Prepared By:	
TITLE:	L37层CJ4-2 梁			BBS NO: MVR-TT-H311


BAR BENDING SCHEDULE											
MEMBER	BAR MARK	TYPE & SIZE	NO. OF MBRS	NO. OF EACH	TOTAL	SHAPE CODE	SHAPE		CUT OFF LENGTH	WEIGHT	
				LB11 (150*200)			45#				
T1		H 13	1	2	2	38a	130	2250	130	2510	5.23
B1		H 16	1	2	2	38a	130	2250	130	2510	7.93
L		H 08	1	16	16	61	90	130		632	3.99
				LB6 (200*200)			46#				
T1		H 13	1	2	2	38a	220	2180	220	2620	5.46
B1		H 16	1	2	2	20	2500			2500	7.90
L		H 08	1	16	16	61	130	130		712	4.50
				LB6 (200*200)			47#				
T1		H 13	1	2	2	37	130	1300		1430	2.98
B1		H 16	1	2	2	37	130	1400		1530	4.83

REBAR SIZE		R06	H08	H10	H13	H16	H20	H25	H32	H40	TOTAL
WEIGHT			8.5		13.7	20.7					42.8 KG

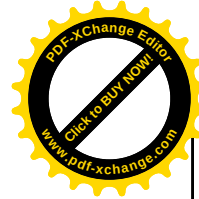

GENERAL NOTES (UNLESS OTHERWISE NOTED:

1. SLAB DROP/KERB LOCATION & SIZE, STAIRCASE DETAILS
FFL R.C. WALL, OPENING LOCATION & SIZE
REFER TO LATEST ARCH'L SETTING OUT PLAN.
2. CONCRETE GRADE SHALL BE C32/40 FOR ALL ELEMENTS.

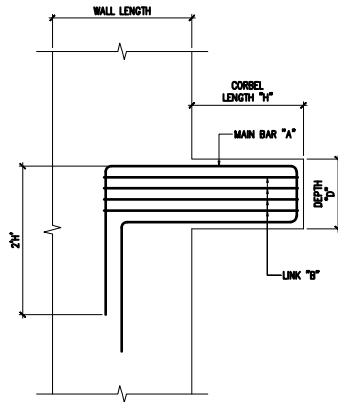

DETAIL A - STANDARD CORBEL DETAIL

SCALE : 1:25

ABBREVIATION:

SFL - STRUCTURAL FLOOR LEVEL
FFL - FINISH FLOOR LEVEL
BFL - BASIC FLOOR LEVEL
USL - UPPER SLAB LEVEL
BSL - BELOW SLAB LEVEL
MSL - MID SLAB LEVEL
TOB - TOP OF BEAM
BOB - BOTTOM OF BEAM
LSB - LIFT SEPARATION BEAM
TOW - TOP OF WALL
BOO - BOTTOM OF OPENING
BOW - BOTTOM OF WALL
U/S - UPSTAND BEAM
TOC - TOP OF COLUMN
TOCB - TOP OF CAPPING BEAM
SIL - STRUCTURAL INVERT LEVEL
MCL - MASS CONCRETE LEVEL
TOPC - TOP OF PILE CAP
TOP - TOP OF PLINTH
TO - TEMPORARY OPENING
PH - PASSENGER HOIST

LEGEND:

- RC WALL / COLUMN
- RC WALL / COLUMN BELOW
- DOUBLE SLAB
- MASS CONCRETE
- NON-LOAD BEARING WALL
- IMPACT WALL/PARAPET WALL
- RECESS
- DOWNHANG WALL
- TEMPORARY BEAM
- TEMPORARY SLAB
- TEMPORARY OPENING
- MUCKHOLE
- FOR CONFIRMATION / K I V
- REVISION
- 200 SLAB THICKNESS
- HCS200 HOLLOWCORE SLAB THICKNESS
- PBU HATCH

1 sheet of 25

BUILDING AND CONSTRUCTION AUTHORITY

APPROVED UNDER SECTION 5 / SECTION 5A OF THE
BUILDING CONTROL ACT (CHAPTER 29)

Project Ref No : A1252-00566-2022-ST19

for Commissioner of Building Control

DT-MVR-C&S-178

FOR CONSTRUCTION

22 MAY 2025

TECHNICAL
WOH HUP (PRIVATE) LIMITED
MARINA VIEW RESIDENCES (MVR)

PE'S CERTIFICATION



AC'S CERTIFICATION

ACCREDITED CHECKER

NO: 1089



MVR PJW CO WH CST ZZ SK W 2080B

Typical Lintel Beam Rev B

Revision B Changes:
Refer to pg 2. L34 Lintel
beam shall follow as per
lintel beam schedule

E TYPICAL LINTEL BEAM SCHEDULE 3500

LINTEL SCHEDULE [FOR 100 THK x 2500 HIGH(max.) BRICKWALL ONLY]				
LINTEL	SPAN (m)	DEPTH x WIDTH (mm)	REINFT.	LINK
LB1	2.0	200 x 100	1H13 (T) & 1H16 (B)	H8 – 125
LB2	3.0	300 x 100	1H13 (T) & 1H16 (B)	H8 – 150
LB3	4.0	350 x 100	1H13 (T) & 1H16 (B)	H8 – 175
LB4	5.0	450 x 100	1H16 (T) & 1H20 (B)	H10 – 250
LB5	> 5.0	DETAILS TO STRUCTURAL DESIGN OR TO CONTRACTOR'S PROPOSAL		

SNAPSHOT OF 21.070/N1

3500

LINTEL SCHEDULE [FOR 200 THK x 2500 HIGH(max.) BRICKWALL ONLY]				
LINTEL	SPAN (m)	DEPTH x WIDTH (mm)	REINFT.	LINK
LB6	2.0	200 x 200	2H13 (T) & 2H16 (B)	H8 – 125
LB7	3.0	300 x 200	2H13 (T) & 2H16 (B)	H8 – 150
LB8	4.0	350 x 200	2H13 (T) & 2H16 (B)	H8 – 175
LB9	5.0	450 x 200	2H16 (T) & 2H20 (B)	H10 – 250
LB10	> 5.0	DETAILS TO STRUCTURAL DESIGN OR TO CONTRACTOR'S PROPOSAL		

SNAPSHOT OF 21.070/N1

3500

LINTEL SCHEDULE [FOR 150 THK x 2500 HIGH(max.) BRICKWALL ONLY]				
LINTEL	SPAN (m)	DEPTH x WIDTH (mm)	REINFT.	LINK
LB11	2.0	200 x 150	2H13 (T) & 2H16 (B)	H8 – 125
LB12	3.0	300 x 150	2H13 (T) & 2H16 (B)	H8 – 150
LB13	4.0	350 x 150	2H13 (T) & 2H16 (B)	H8 – 175
LB14	5.0	450 x 150	2H16 (T) & 2H20 (B)	H10 – 250
LB15	> 5.0	DETAILS TO STRUCTURAL DESIGN OR TO CONTRACTOR'S PROPOSAL		

FOR CONSTRUCTION

22 APR 2026

TECHNICAL
WOH HUP (PRIVATE) LIMITED
MARINA VIEW RESIDENCES (MVR)

INTERPOLATION
BETWEEN 100mm THK &
200mm THK LINTEL

Copy to

1. PD - Chen Han Qi
2. PM - Wong Wei Siong
3. SE
4. RE/RTO
5. All Subcons
6. WH CST
7. WH QS
8. WH Rebar Scheduler
9. DC
10. IOI - Muliadi, How See, Darren

From: Joseph
22-Apr-26

KTP 20250804:


We concur all the lintel schedules can
withstand upto 3.5m high brickwall (24kN/m3)


KTP- NO OBJECTION

08/29/2024




KTP: Refer to MVR
- Beam Recess
Alternative Rebar
Details Sketch for
Z/C-bar provision

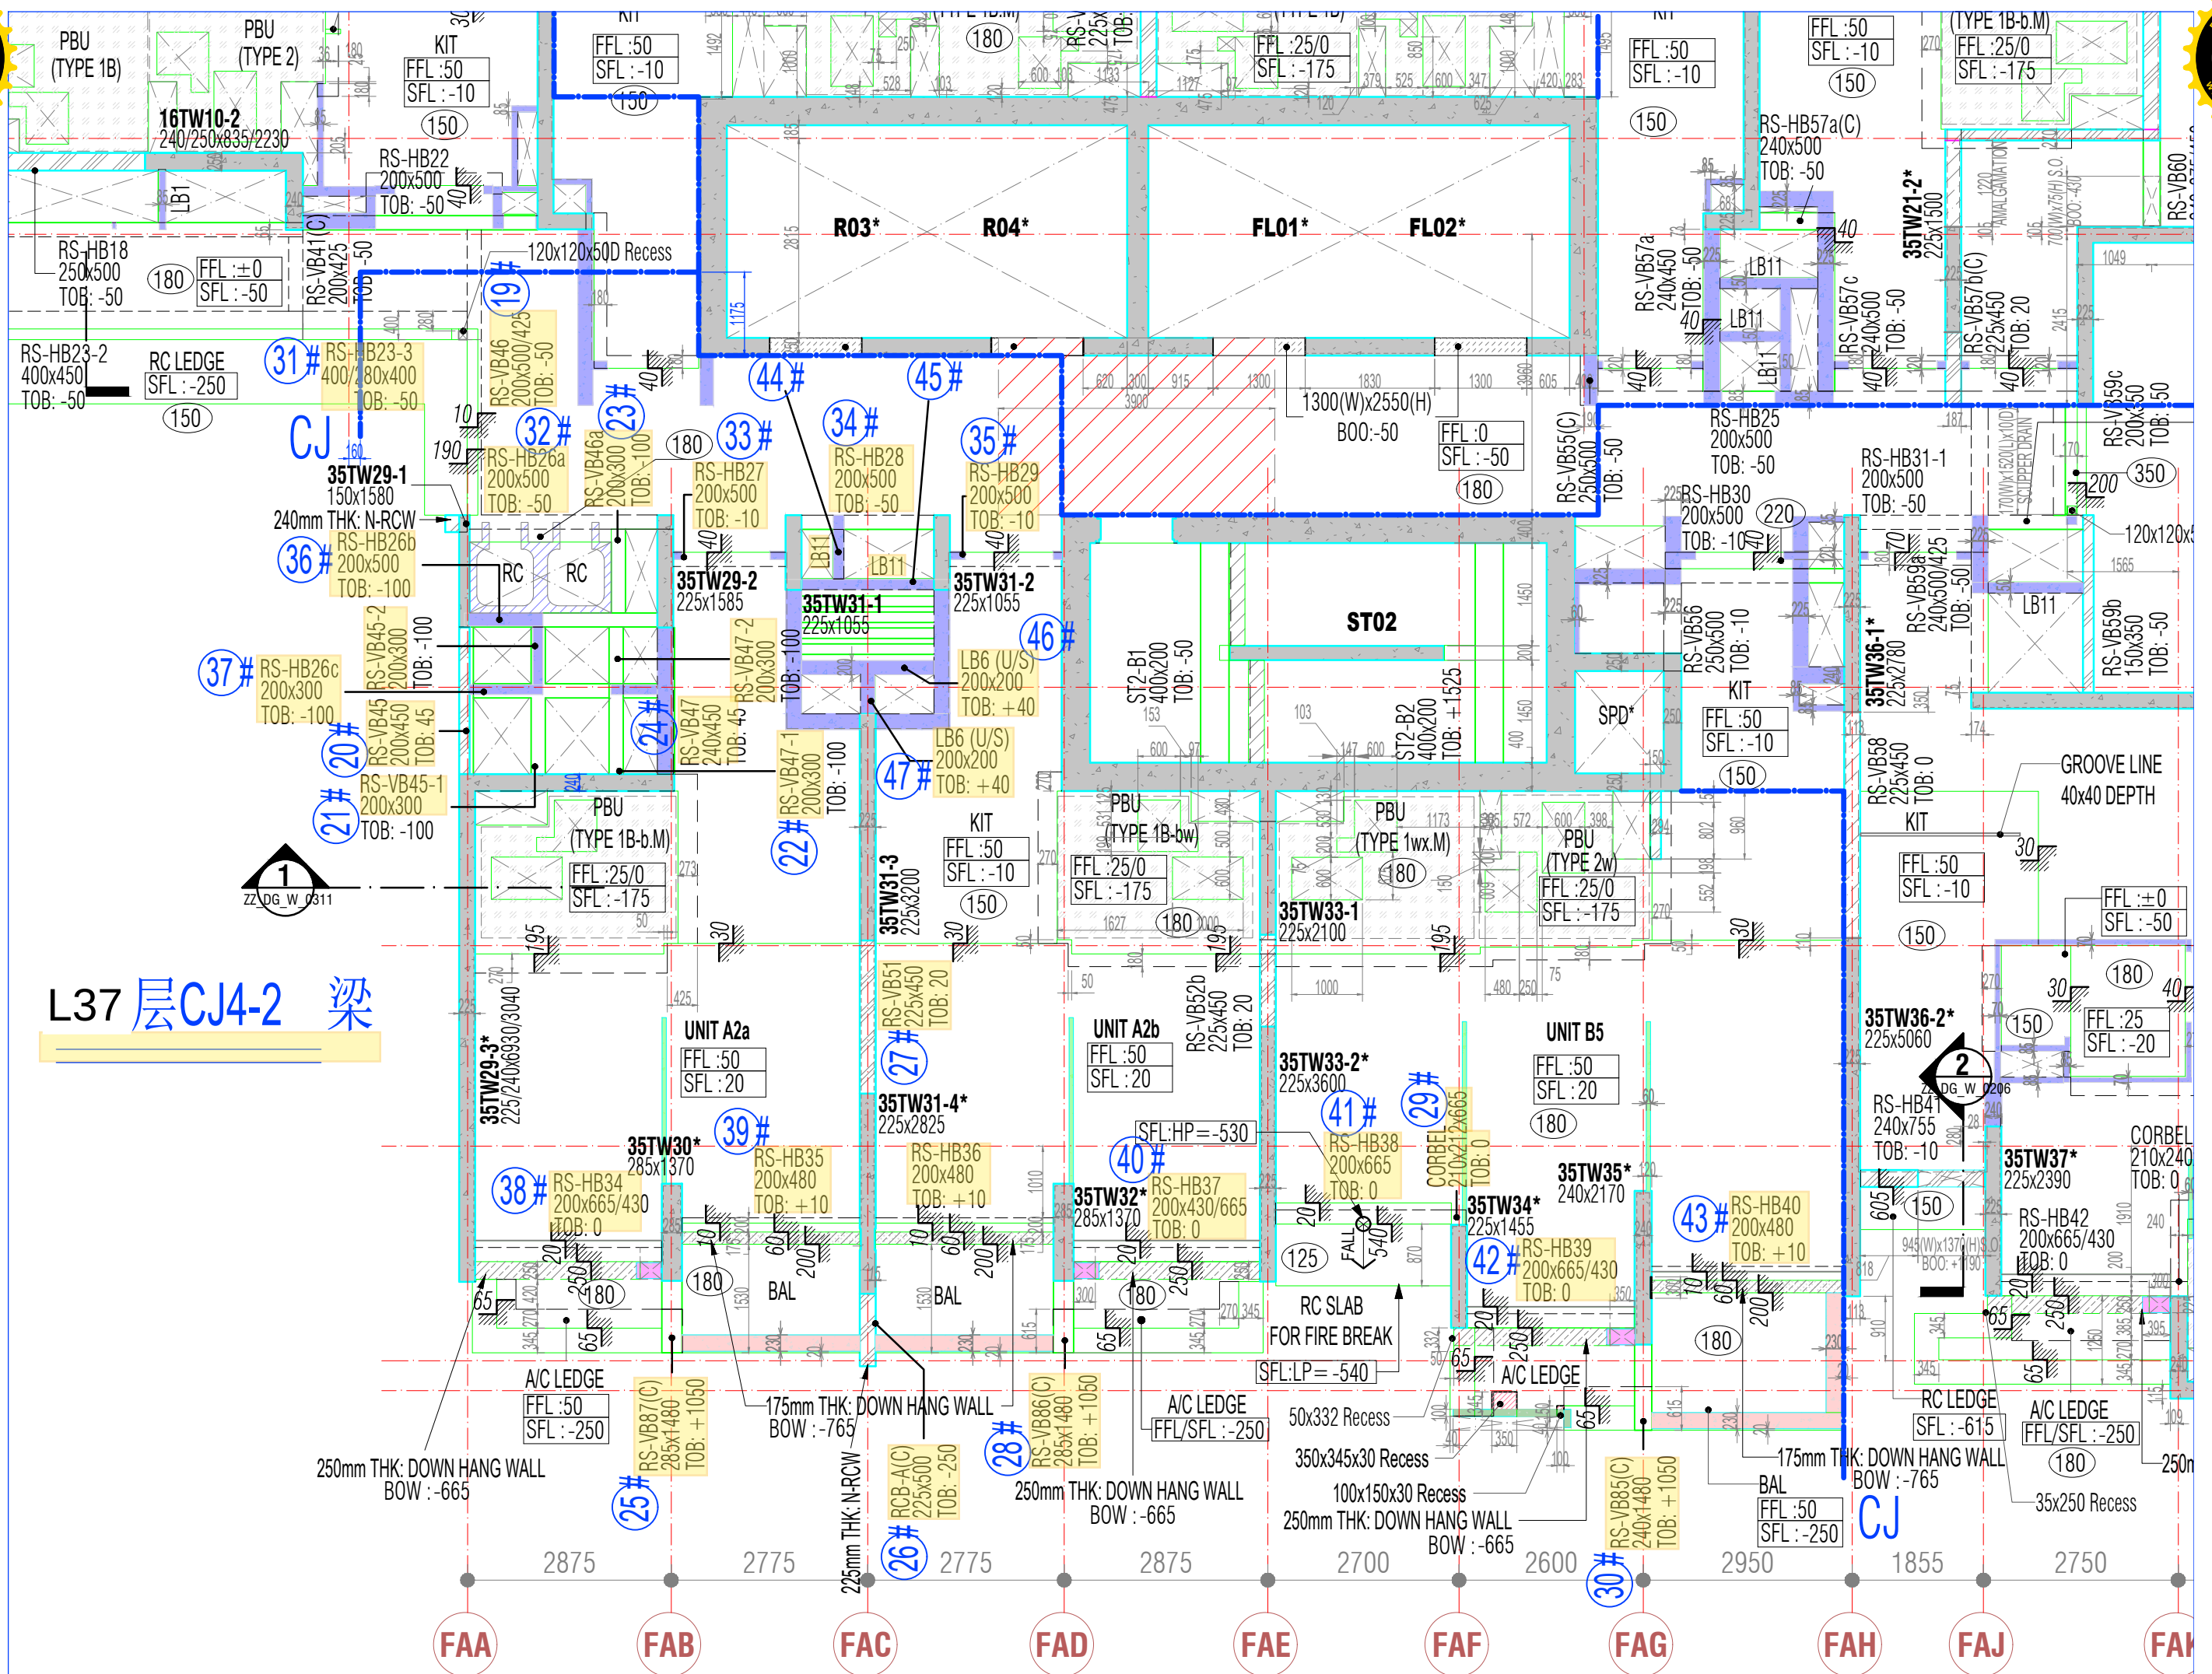

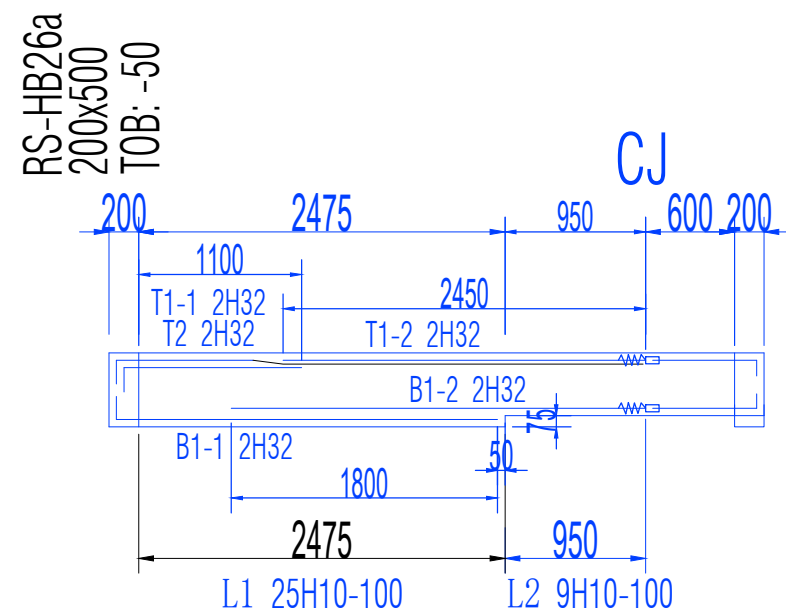

19 #

RS-VB46
200x500/425
TOB: -50

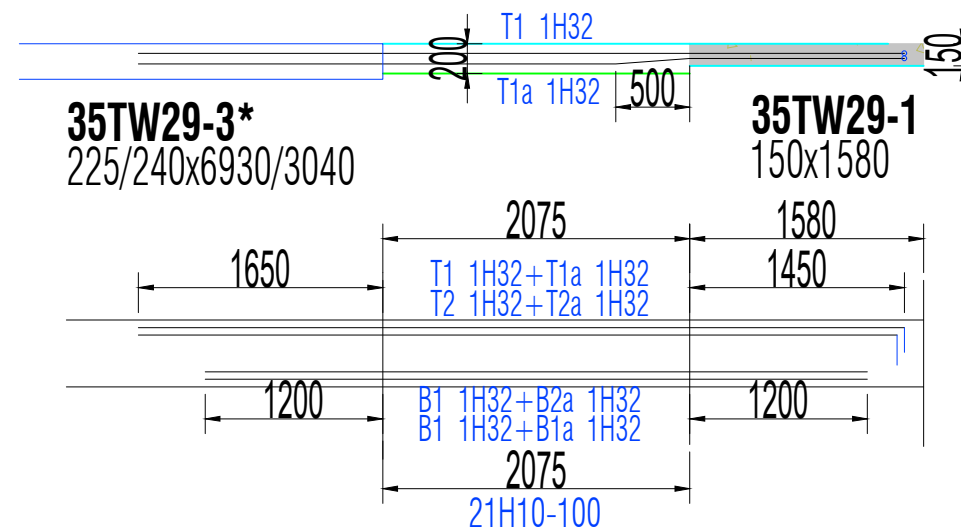



20 #

RS-VB45
200x450
TOB: 45

21 #

RS-VB45-1
200x300
TOB: -100


RS-VB45-2
200x300
TOB: -100

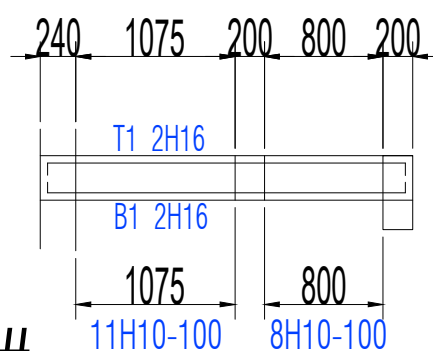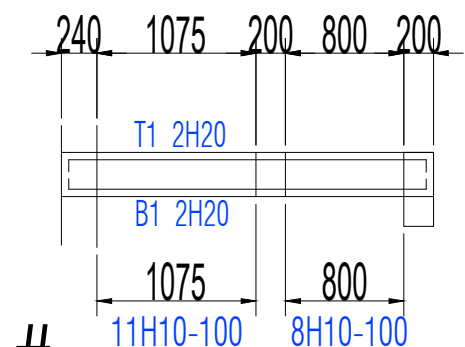

22 #


RS-VB47-1
200x300
TOB: -100

RS-VB47-2
200x300
TOB: -100

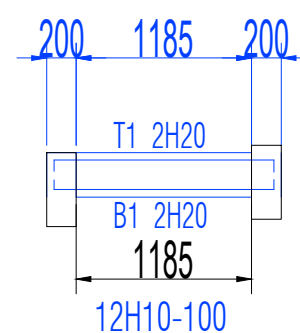








23 #


RS-VB46a
200x300
TOB: -100

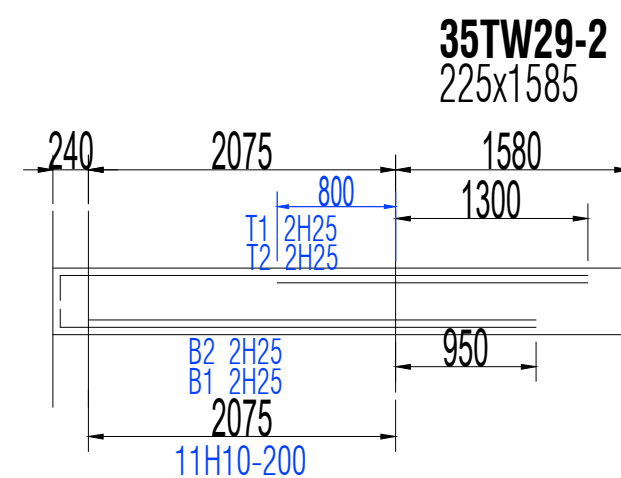

24 #


RS-VB47
240x450
TOB: 45

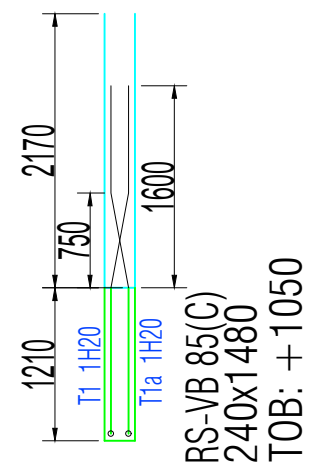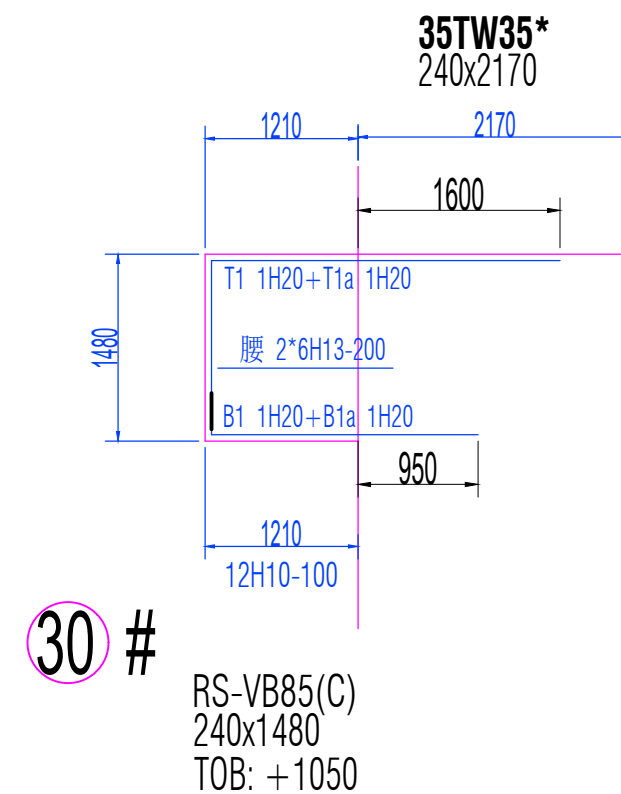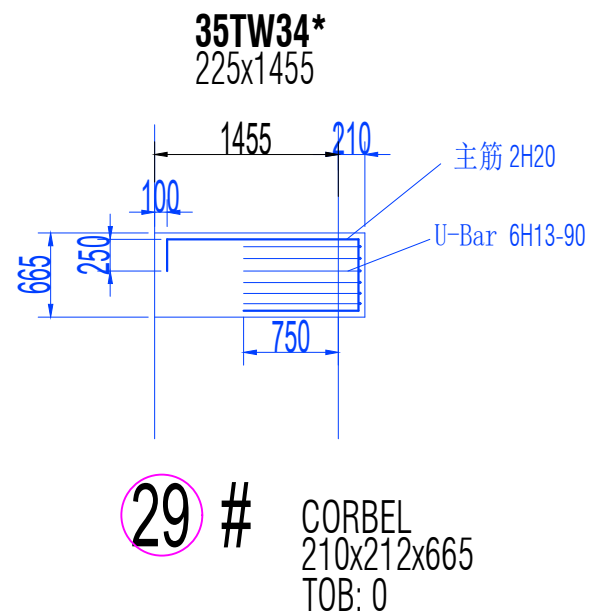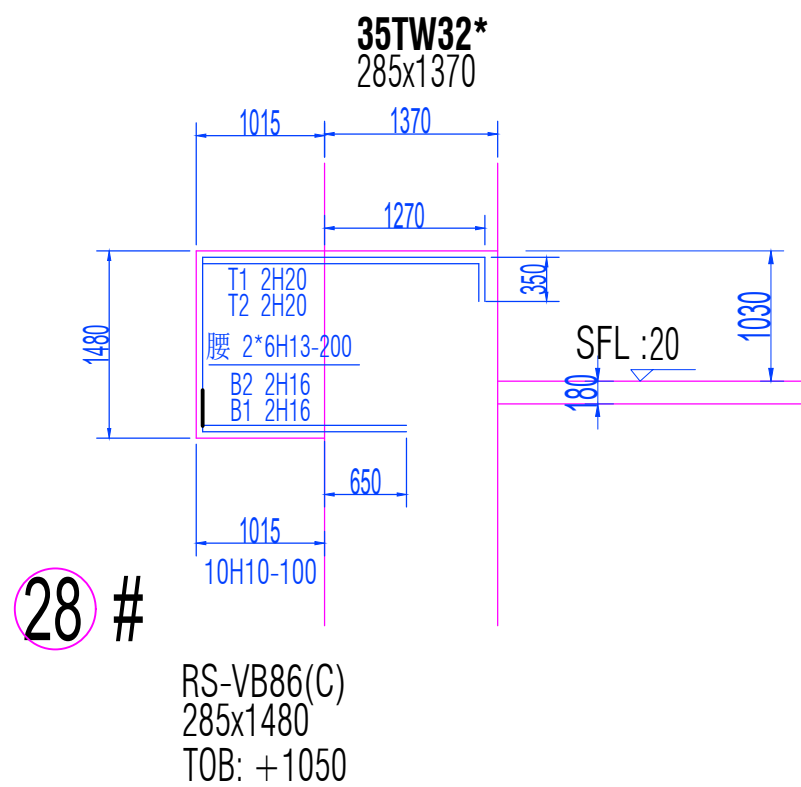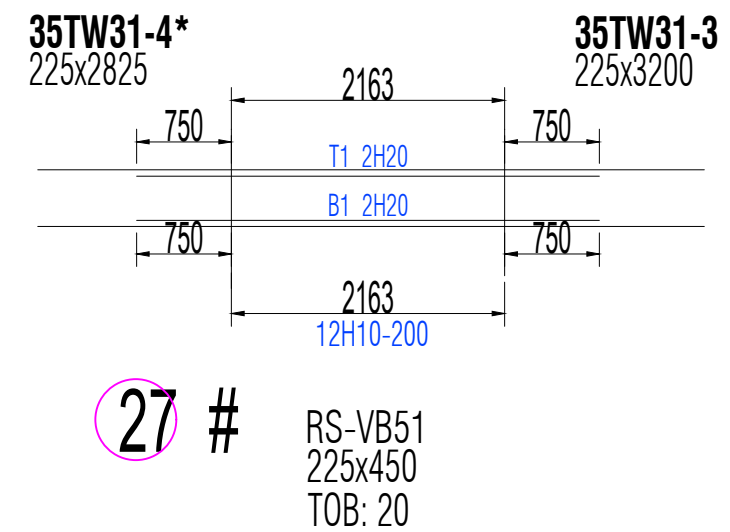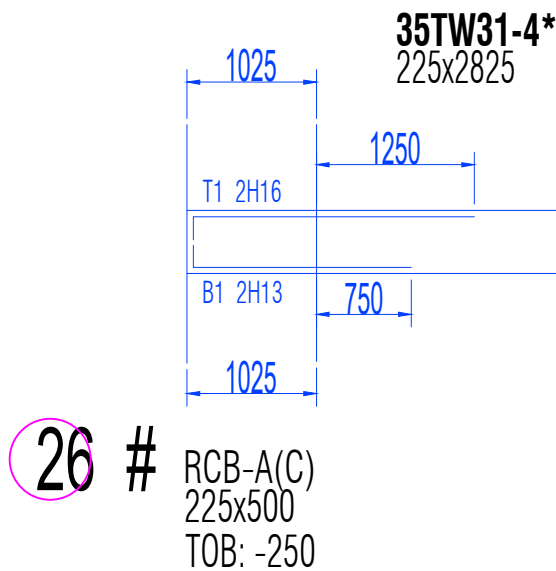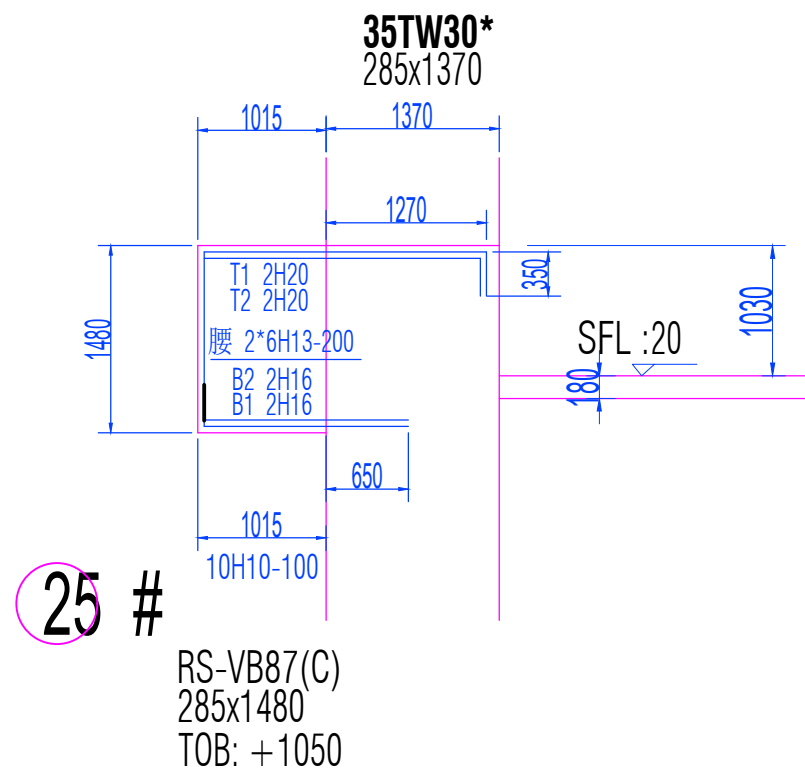

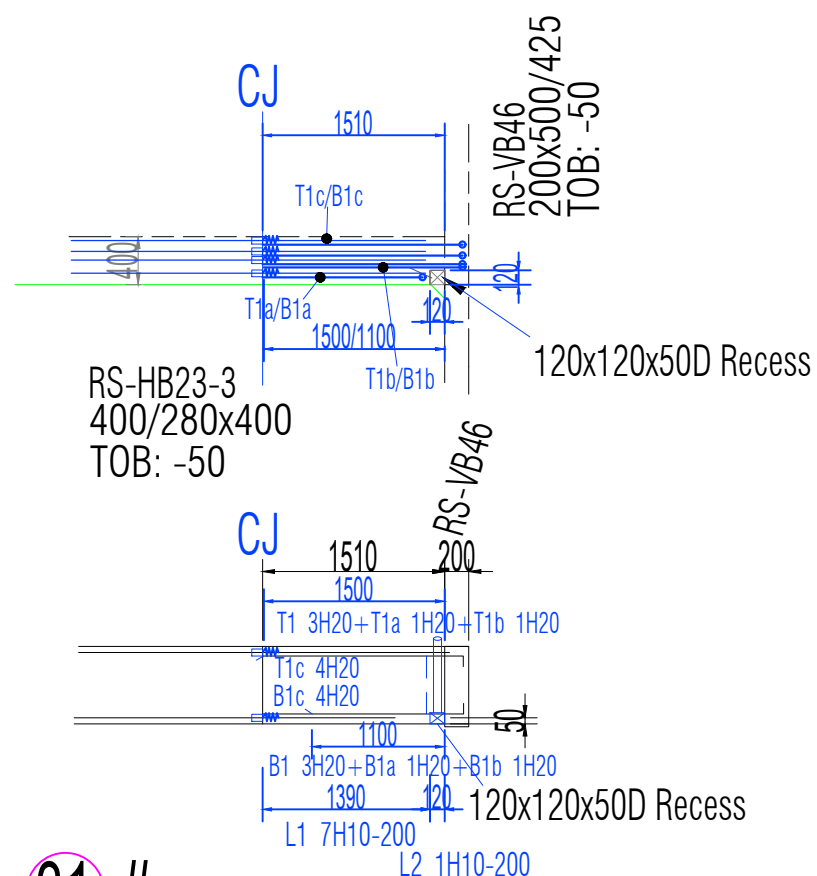


31 #

RS-HB23-3
400/280x400
TOB: -50

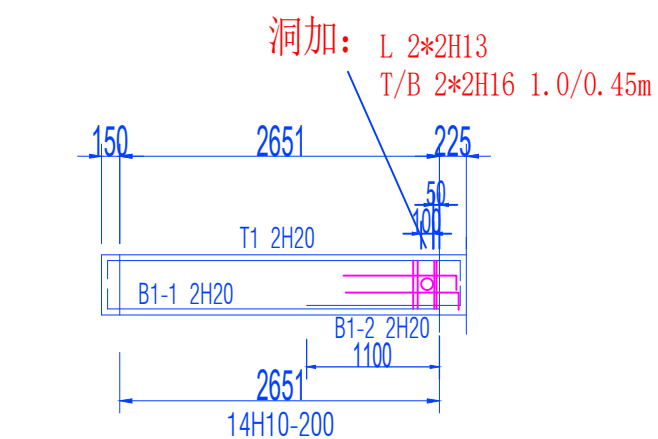


32 #

RS-HB26a
200x500
TOB: -50

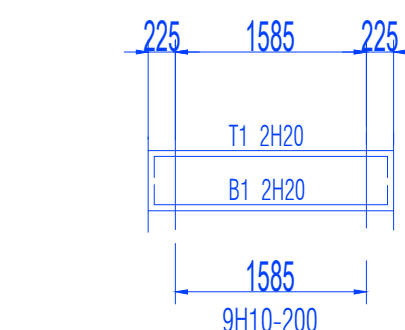


33 #

RS-HB27
200x500
TOB: -10

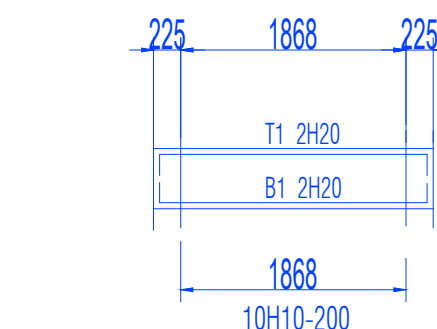


34 #

RS-HB28
200x500
TOB: -50

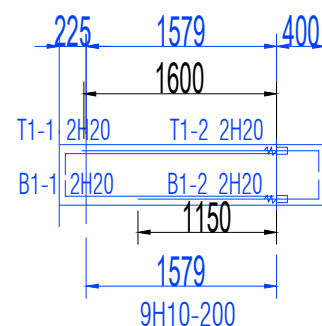


35 #

RS-HB29
200x500
TOB: -10

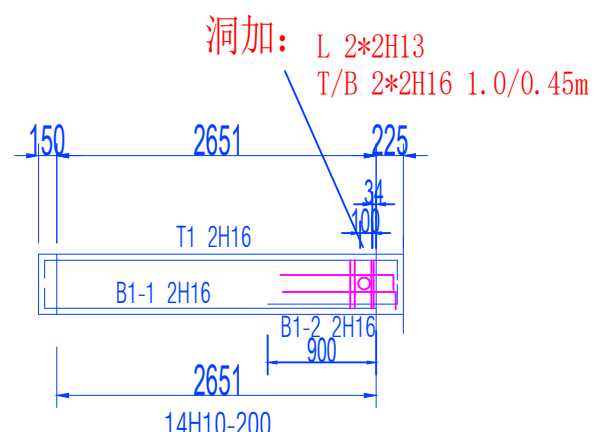


36 #

RS-HB26b
200x500
TOB: -100

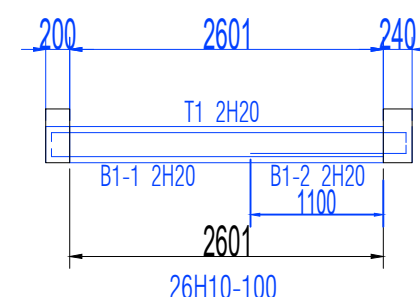

37 #


RS-HB26c
200x300
TOB: -100

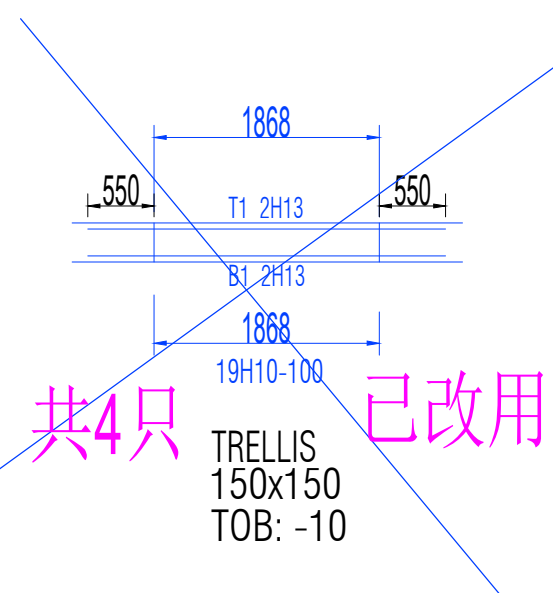


共4只

已改用预制梁

TRELLIS
150x150
TOB: -10

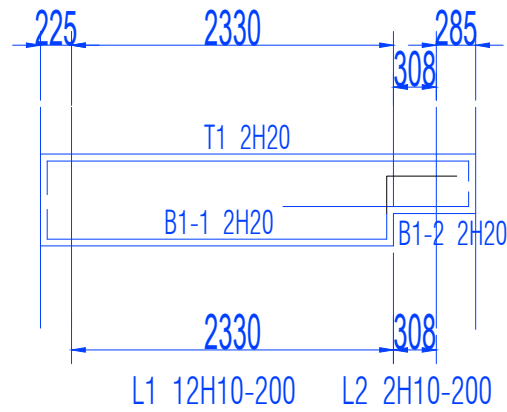


38 # RS-HB34
200x665/430
TOB: 0

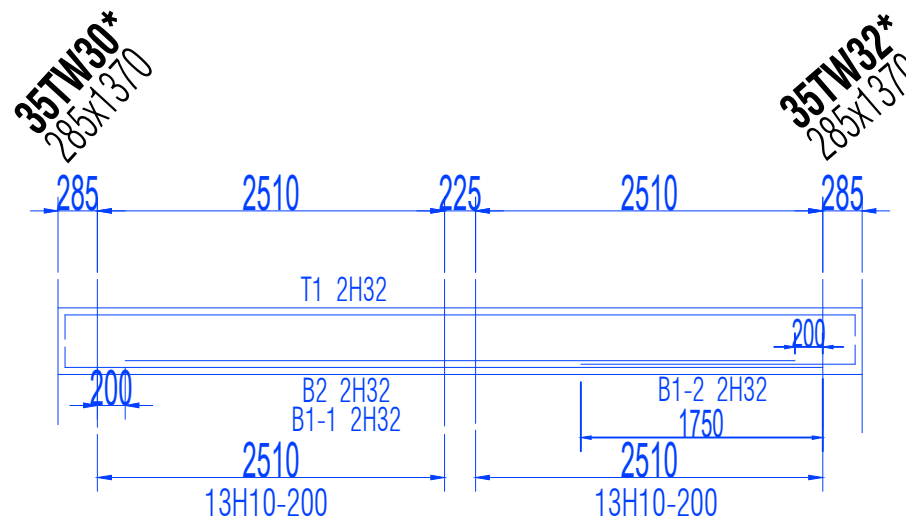


39 # RS-HB35
200x480
TOB: +10


RS-HB36
200x480
TOB: +10

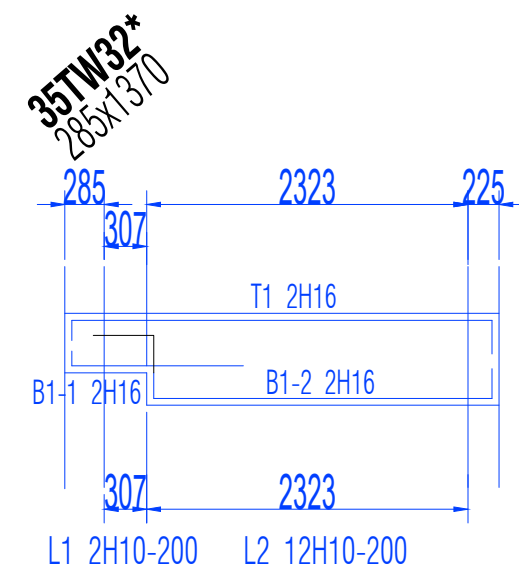


40 # RS-HB37
200x430/665
TOB: 0

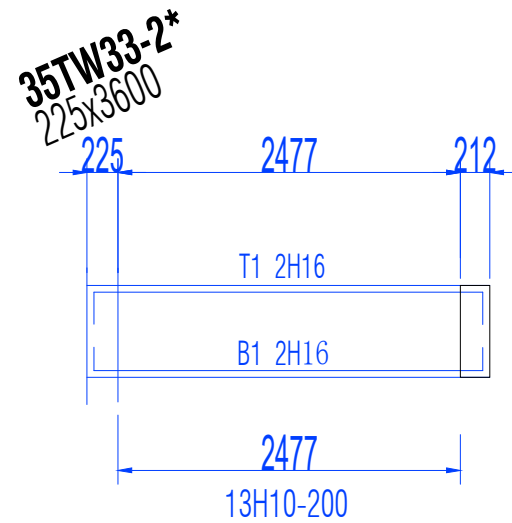


41 # RS-HB38
200x665
TOB: 0

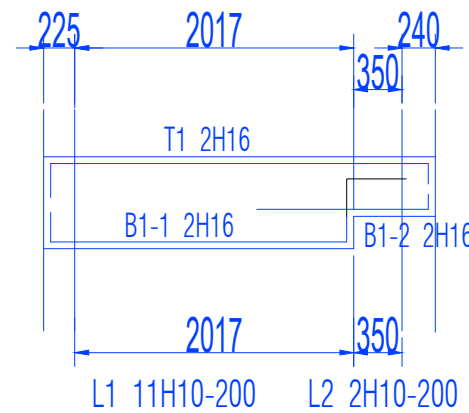


42 # RS-HB39
200x665/430
TOB: 0

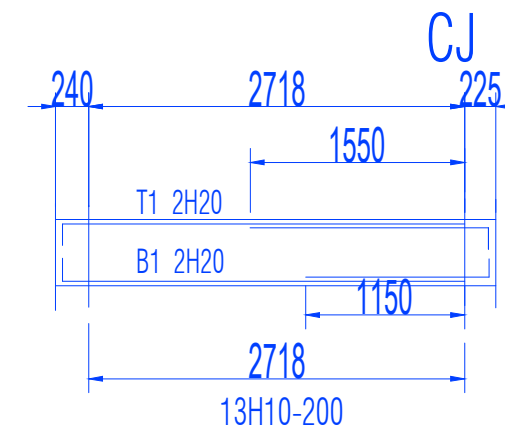


43 # RS-HB40
200x480
TOB: +10

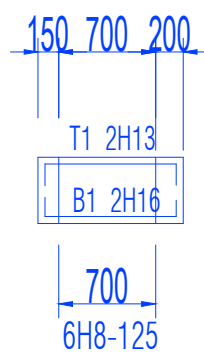


44 # LB11 (150*200)

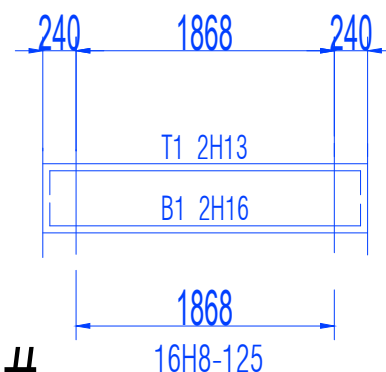

45 # LB11 (150*200)

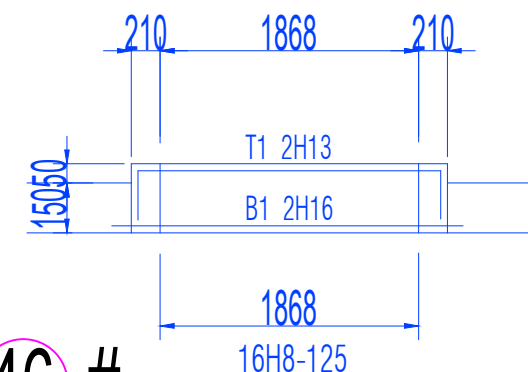



46 # LB6 (200*200)

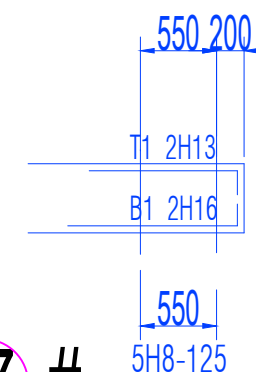


47 # LB6 (200*200)




MVR PJW CO WH CST ZZ ZZ SK W 2792
L36-48 RC Beam Schedule

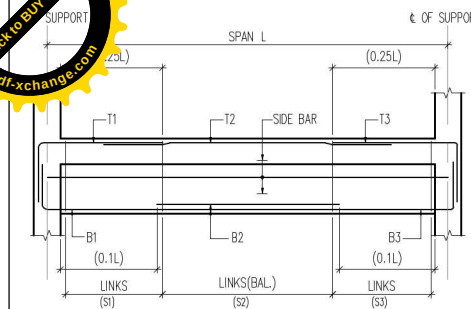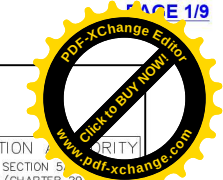

TYPICAL SINGLE SPAN BEAM
SIMPLY SUPPORTED FRAME (SF) & MOMENT FRAME (MF)

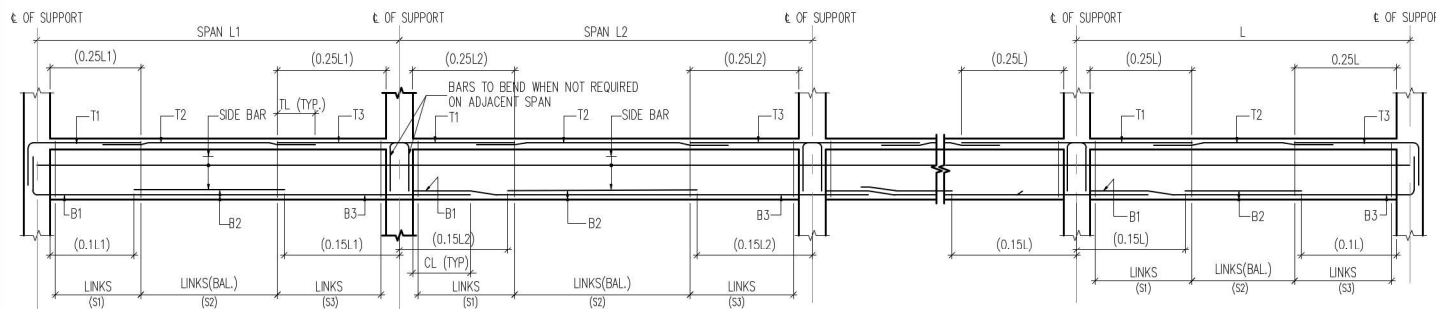

NOTES:
1. D = BEAM DEPTH
2. SHOULD THE REINF. B3 & B1 AT A SUPPORT FOR CONTINUOUS BEAM DIFFER, REBAR WHICHEVER IS GREATER SHOULD BE ADOPTED.

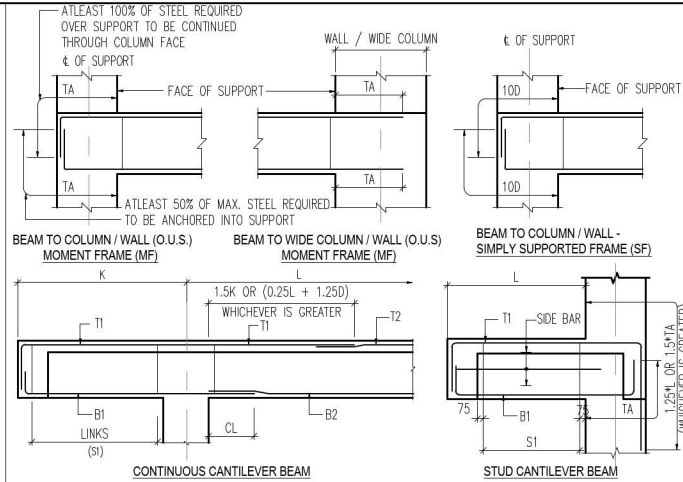

— sheet of —

BUILDING AND CONSTRUCTION AUTHORITY
APPROVED UNDER SECTION 5 / SECTION 5
BUILDING CONTROL ACT (CHAPTER 29)

Project Ref No : A1252-00566-2022--

Copy to
1. PD - Chen Han Qi
2. SPMPM
3. SE
4. RE/TO
5. All Subcon
6. WH MVR, WH Site
7. WH QS
8. WH Rebar Scheduler
9. DC
10. IOI - Muliadi, How See, Darren

From: Calvin Yap
29-June-2026

FOR CONSTRUCTION
29 Jun 2026

TECHNICAL
WOH HUP PRIVATE LIMITED
MARINA VIEW RESIDENCES (MVR)

BEAM MARK	BEAM SIZE (WxD)	TOP BARS			BOTTOM BARS			LINKS			SIDE BAR	REMARKS
		T1	T2	T3	B1	B2	B3	TYPE	S1	S2	S3	
L36-HB1(C)	200x665	2H25	-	-	2H20	-	-	A1	H10-100	-	-	CANT
L36-HB2	200x430/665	2H16	2H16	2H16	2H16	2H16	2H16	A1	H10-200	H10-200	H10-200	SF
L36-HB3	225x755	2H16	2H16	2H16	2H16	2H16	2H16	A1	H10-200	H10-200	H10-200	SF
L36-HB4	200x480	2H16	2H16	2H16	2H16	2H16	2H16	A1	H10-200	H10-200	H10-200	SF
L36-HB5	200x430/665	2H16	2H16	2H16	2H16	2H16	2H16	A1	H10-200	H10-200	H10-200	SF
L36-HB6	200x665	2H16	2H16	2H16	2H16	2H16	2H16	A1	H10-200	H10-200	H10-200	SF
L36-HB7	450x415/180	4H20	4H20	4H20	4H20	4H20	4H20	A1	H10-100	H10-100	H10-50	SF, TL
L36-HB8	200x480	2H20	2H20	2H20+2H20	2H20	2H20+2H20	2H20	A1	H13-100	H13-100	H13-100	SF
L36-HB9	200x480	2H20	2H20	2H20	2H20	2H20	2H20	A1	H10-200	H10-200	H10-200	SF
L36-HB10	200x430/665	2H16	2H16	2H16	2H16	2H16	2H16	A1	H10-200	H10-200	H10-200	SF
L36-HB11	200x665	2H32	2H32+2H32	2H32+2H32+2H25	2H25	2H25	2H25	A1	H10-200	H10-200	H10-200	SF, MF
L36-HB12	200x665	2H32+2H32+2H25	2H32+2H32	2H32	2H25	2H25	2H25	A1	H10-200	H10-200	H10-200	SF, MF
L36-HB13	200x665/430	2H20	2H20	2H20	2H20	2H20	2H20	A1	H10-200	H10-200	H10-200	SF
L36-HB14	200x480	2H20	2H20	2H20	2H20	2H20	2H20	A1	H10-200	H10-200	H10-200	SF
L36-HB15	200x480	2H20	2H20	2H20	2H20	2H20	2H20	A1	H10-200	H10-200	H10-200	SF
L36-HB16	200x430/665	2H16	2H16	2H16	2H16	2H16	2H16	A1	H10-200	H10-200	H10-200	SF
L36-HB17(C)	200x665	2H25	-	-	2H20	-	-	A1	H10-100	-	-	CANT
L36-HB18	250x500	2H16	2H16	2H16	2H16	2H16+2H16	2H16	A1	H10-200	H10-200	H10-200	SF
L36-HB19	220/200x500	2H32	2H32	2H32	2H32+2H25	2H32+2H25	2H32+2H25	A1	H10-200	H10-200	H10-200	SF
L36-HB21	200x500	2H25	2H25	2H25	2H25	2H25	2H25	A1	H10-200	H10-200	H10-200	SF
L36-HB22	200x500	2H25	2H25	2H25	2H25+2H25	2H25+2H25	2H25+2H25	A1	H10-200	H10-200	H10-200	SF
L36-HB23-1	280/400x400	4H20	4H20	4H20+4H20	4H20	4H20	4H20	A1	H10-200	H10-200	H10-200	SF, MF
L36-HB23-2	400x450	4H20+4H20	4H20	4H20	4H20+4H20	4H20+4H20	4H20+4H20	A1	H10-200	H10-200	H10-200	SF, MF
L36-HB23-3	400/280x400	4H20	4H20	4H20	4H20+4H20	4H20	4H20	A1	H10-200	H10-200	H10-200	SF, MF
L36-HB25	200x500	2H25	2H25	2H25	2H25	2H25	2H25	A1	H10-200	H10-200	H10-200	SF
L36-HB26a	200x500	2H20	2H20	2H20	2H20	2H20	2H20	A1	H10-200	H10-200	H10-200	SF
L36-HB27	200x500	2H20	2H20	2H20	2H20	2H20	2H20	A1	H10-200	H10-200	H10-200	SF
L36-HB30	200x500	2H25	2H25	2H25	2H20	2H20	2H20	A1	H10-200	H10-200	H10-200	SF
L36-HB31-1	200x500	2H20	2H20	2H20+2H20	2H20	2H20	2H20	A1	H10-200	H10-200	H10-200	SF, MF
L36-HB31-2(C)	200x500	2H20+2H20	-	-	2H20	-	-	A1	H10-100	-	-	CANT
L36-HB34	200x665/430	2H20	2H20	2H20	2H20	2H20	2H20	A1	H10-200	H10-200	H10-200	SF
L36-HB35	200x480	2H32	2H32	2H32	2H32	2H32+2H32	2H32+2H32	A1	H10-200	H10-200	H10-200	SF, MF
L36-HB36	200x480	2H32	2H32	2H32	2H32+2H32	2H32+2H32	2H32	A1	H10-200	H10-200	H10-200	SF, MF

PE'S CERTIFICATION

PROFESSIONAL ENGINEER
CIVIL
FOONG KIT KUEN
4340
SINGAPORE

AC'S CERTIFICATION

ACCREDITED CHECKER
NO: 1089

KOK KING MIN
In AC Organisation
Registration No: A054
BUILDING CONTROL ACT
SINGAPORE

CONSTRUCTION SKETCH

ISSUED
29 JUNE 2026
KTP CONSULTANTS PTE. LTD.

REV	AMENDMENTS	DR	DES	CHK	DATE
2	REVISED BEAM DETAILS				01.06.26
1	REVISED BEAM DETAILS				10.03.25

PROJECT

PROPOSED NEW ERECTION OF 51 STOREY MIXED USE DEVELOPMENT COMPRISING 5 STOREY HOTEL AND CARPARK PODIUM, 9 STOREY HOTEL (350 ROOMS), 36/37 STOREY RESIDENTIAL FLATS (683 UNITS) AND 2 BASEMENTS ON LOTS 00483K AND 00484N TS 30 AND SUBTERRANEAN SPACE LOT 800772C TS 30 AT MARINA VIEW (DOWNTOWN CORE PLANNING AREA)

ARCHITECT
ARCHITECT 61 PTE. LTD.

KTP CONSULTANTS PTE LTD
Surbana Jurong Campus 38 Cleantech Loop, #01-31 Singapore 636741
Tel : 65 6248 1288

DRAWN: CH	DATE:	DESIGNED: JS/AP/TS
SCALE: 1:100	CHECKED: ChewAL	


DWG. NO. 21.070/L36B1

LEVEL-36 TO L38 BEAM SCHEDULE-1


THE OWNERSHIP OF THE COPYRIGHT IN THIS DRAWING IS RETAINED BY KTP CONSULTANTS. WHOSE CONSENT MUST BE SOUGHT BEFORE ANY USE OR REPRODUCTION OF THE DRAWING OR ANY PART THEREOF CAN BE MADE.



MVR PJW CO WH CST ZZ ZZ SK W 2792
L36-48 RC Beam Schedule

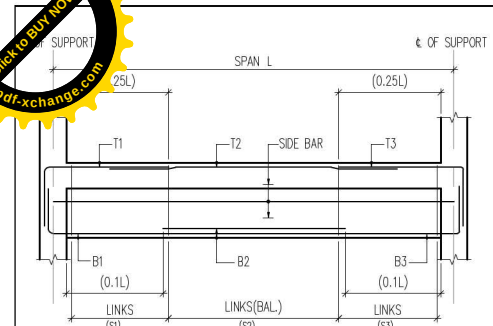


TYPICAL SINGLE SPAN BEAM
SIMPLY SUPPORTED FRAME (SF) & MOMENT FRAME (MF)

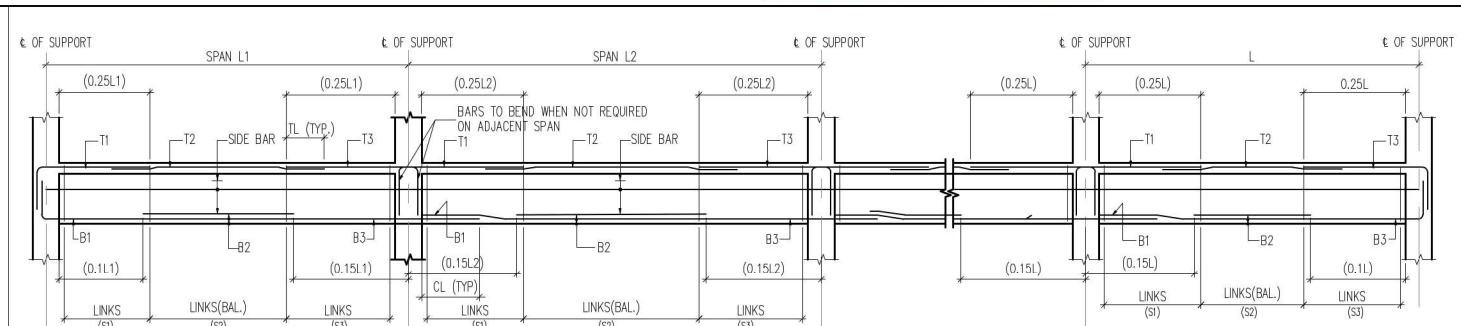

LEFT END SPAN TYPICAL INTERMEDIATE SPAN TYPICAL INTERMEDIATE SPAN RIGHT END SPAN
TYPICAL CONTINUOUS SPAN BEAM

NOTES:
1. D = BEAM DEPTH
2. SHOULD THE REINF. B3 & B1 AT A SUPPORT FOR CONTINUOUS BEAM DIFFER, REBAR WHICHEVER IS GREATER SHOULD BE ADOPTED.

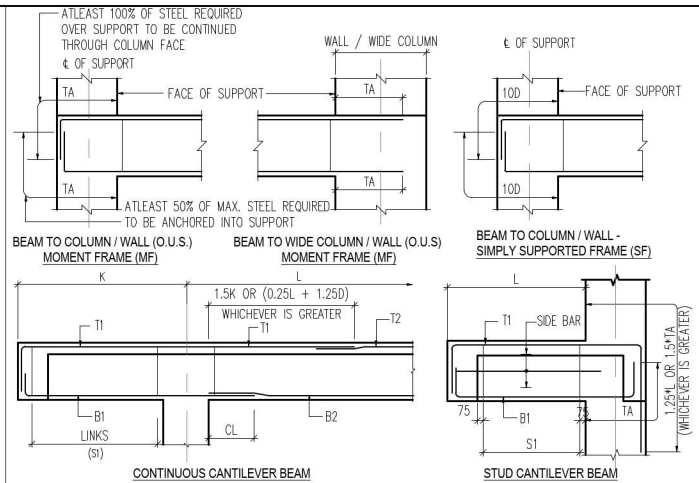

— sheet of —

BUILDING AND CONSTRUCTION
APPROVED UNDER SECTION 5 / SECTION 5A
BUILDING CONTROL ACT (CHAPTER 29)

Project Ref No : A1252-00566-2022--

for Commissioner of Building Control

FOR CONSTRUCTION
29 Jun 2026
TECHNICAL
WOH HUP (PRIVATE) LIMITED
MARINA VIEW RESIDENCES (MVR)

BEAM MARK	BEAM SIZE (WxD)	TOP BARS			BOTTOM BARS			LINKS				SIDE BAR	REMARKS	BEAM MARK	BEAM SIZE (WxD)	TOP BARS			BOTTOM BARS			LINKS				SIDE BAR	REMARKS
		T1	T2	T3	B1	B2	B3	TYPE	S1	S2	S3					T1	T2	T3	B1	B2	B3	TYPE	S1	S2	S3		
L36-VB56c	200x350	2H16	2H16	2H16	2H16	2H16	2H16	A1	H10-200	H10-200	H10-200		SF	L36-VB56c	200x350	2H16	2H16	2H16	2H16	2H16	2H16	A1	H10-200	H10-200	H10-200		SF
L36-VB60	240x375x450	2H32	2H32	2H32	2H32	2H32+2H32	2H32+2H32	A1	H10-100	H10-100	H10-100		SF	L36-VB4	200x665	2H25	2H25	2H25+2H20	2H32	2H32+2H25	2H32+2H25	A1	H10-200	H10-200	H10-200		SF/MF
L36-VB65	200x665	2H16	2H16	2H16	2H16	2H16	2H16	A1	H10-200	H10-200	H10-200		SF	L36-VB5	200x665	2H25+2H20	2H25	2H20	2H32+2H25	2H32	2H32	A1	H10-200	H10-200	H10-200		MFSF
L36-VB66	200x665x430	2H16	2H16	2H16	2H16	2H16	2H16	A1	H10-200	H10-200	H10-200		SF	L36-VB6	430x420	4H20	4H20	4H20	4H25	4H25	4H25	A1	H10-200	H10-200	H10-200		SF
L36-VB67	200x480	2H16	2H16	2H16	2H25	2H25	2H25	A1	H10-200	H10-200	H10-200		SF	L36-VB7	200x665	2H16	2H16	2H16	2H25	2H25	2H25	A1	H10-200	H10-200	H10-200		SF
L36-VB68	400x420	4H20	4H20	4H20	4H20	4H20	4H20	A1	H10-200	H10-200	H10-200		SF	L36-VB8	200x480	2H20	2H20	2H20	2H20	2H20	2H20	A1	H10-200	H10-200	H10-200		SF
L36-VB69	200x430x665	2H16	2H16	2H16	2H16	2H16	2H16	A1	H10-200	H10-200	H10-200		SF	L36-VB9	200x430x665	2H16	2H16	2H16	2H16	2H16	2H16	A1	H10-200	H10-200	H10-200		SF
L36-VB70	200x665	2H16	2H16	2H16	2H16	2H16	2H16	A1	H10-200	H10-200	H10-200		SF	L36-VB10	200x480	2H20	2H20	2H20	2H20	2H20	2H20	A1	H10-200	H10-200	H10-200		SF
L36-VB71(C)	225x1480	2H20	-	-	2H20	-	-	A1	H10-100	-	-	H13-200	CANT	L36-VB11	200x430x665	2H16	2H16	2H16	2H16	2H16	2H16	A1	H10-200	H10-200	H10-200		SF
L36-VB78(C)	285x1480	2H20+2H20	-	-	2H16+2H16	-	-	A1	H10-100	-	-	H13-200	CANT	L36-VB12	200x665	2H16	2H16	2H16	2H16	2H16	2H16	A1	H10-200	H10-200	H10-200		SF
L36-VB79(C)	285x1480	2H20+2H20	-	-	2H16+2H16	-	-	A1	H10-100	-	-	H13-200	CANT	L36-VB13	200x665	2H16	2H16	2H16	2H16	2H16	2H16	A1	H10-200	H10-200	H10-200		SF
L36-VB80(C)	285x1480	2H20+2H20	-	-	2H16+2H16	-	-	A1	H10-100	-	-	H13-200	CANT	L36-VB14	200x480	2H16	2H16	2H16	2H16	2H16	2H16	A1	H10-200	H10-200	H10-200		SF
L36-VB81(C)	285x1480	2H20+2H20	-	-	2H16+2H16	-	-	A1	H10-100	-	-	H13-200	CANT	L36-VB15	200x430x665	2H16	2H16	2H16	2H16	2H16	2H16	A1	H10-200	H10-200	H10-200		SF
L36-VB82(C)	285x1480	2H20+2H20	-	-	2H16+2H16	-	-	A1	H10-100	-	-	H13-200	CANT	L36-VB21	200x665x430	2H16	2H16	2H16	2H16	2H16	2H16	A1	H10-200	H10-200	H10-200		SF
L36-VB85(C)	240x1480	2H20	-	-	2H20	-	-	A1	H10-100	-	-	H13-200	CANT	L36-VB22	200x500	2H32	2H32+2H32	2H32+2H32	2H32	2H32+2H32	2H32+2H32	A1	H13-100	H13-100	H13-100		SF/MF
L36-VB86(C)	285x1480	2H20+2H20	-	-	2H16+2H16	-	-	A1	H10-100	-	-	H13-200	CANT	L36-VB23	200x500	2H32+2H32	2H32+2H32	2H32	2H32+2H32	2H32	2H32	A1	H10-200	H10-200	H10-200		MFSF
L36-VB87(C)	285x1480	2H20+2H20	-	-	2H16+2H16	-	-	A1	H10-100	-	-	H13-200	CANT	L36-VB24	200x500	2H20	2H20	2H20	2H20	2H20	2H20	A1	H10-100	H10-100	H10-100		SF
L36-HB24(C)	230x425	2H32+2H32	-	-	2H32+2H25	-	-	A1	H13-100	-	-	CANT	L36-VB25	200x500	2H16	2H16	2H16	2H16	2H16	2H16	A1	H13-100	H13-100	H13-100		SF	
L36-HB24a(C)	230x425	2H32+2H32	-	-	2H32	-	-	A1	H10-100	-	-	CANT	L36-VB27	200x425	2H20	2H20	2H20	2H20	2H20	2H20	A1	H10-200	H10-200	H10-200		SF	
L36-HB32(C)	200x500	2H20+2H20	-	-	2H20	-	-	A1	H10-100	-	-	CANT	L36-VB28a	250x500	2H32+2H32	2H32+2H32	2H32+2H32	2H32+2H32	2H32+2H32	2H32+2H32	A1	H10-200	H10-200	H10-200		SF	
L36-HB33	225x450x450	2H25+2H25	2H25	2H25	2H32	2H32	2H32	A1	H10-200	H10-200	H10-200	MFSF	L36-VB29	200x500	2H16	2H16	2H16	2H16	2H16	2H16	A1	H10-200	H10-200	H10-200		SF	
L36-HB44	200x500	2H16	2H16	2H16	2H16	2H16	2H16	A1	H10-200	H10-200	H10-200	SF	L36-VB28b(US)	240x305	2H16	2H16	2H16	2H16	2H16	2H16	A1	H10-100	H10-100	H10-100		SF	
L36-HB45	225x420x450	2H25	2H25	2H25	2H32	2H32	2H32	A1	H10-200	H10-200	H10-200	SF	L36-VB30a	200x500	2H16	2H16	2H16	2H25	2H25	2H25	A1	H10-200	H10-200	H10-200		SF	
L36-HB46(C)	250x500	2H25	-	-	2H16	-	-	A1	H10-100	-	-	CANT	L36-VB30b	200x500	2H16	2H16	2H16	2H25	2H25	2H25	A1	H10-200	H10-200	H10-200		SF	
L36-HB47	250x450	2H16	2H16	2H16	2H16	2H16	2H16	A1	H10-200	H10-200	H10-200	SF	L36-VB31	200x500	2H16	2H16	2H16	2H25	2H25	2H25	A1	H10-200	H10-200	H10-200		SF	
L36-HB48	225x450	2H16	2H16	2H16	2H16	2H16	2H16	A1	H10-200	H10-200	H10-200	SF	L36-VB32-1	255x500	2H32	2H32	2H32	2H32	2H32	2H32	A1	H10-200	H10-200	H10-200		SF/MF	
L36-HB49	280x400	2H20	2H20	2H20	2H16+2H16	2H16+2H16	2H16	A1	H10-100	H10-100	H10-100	SF	L36-VB32-2	200x500	2H32	2H32	2H32	2H32	2H32+2H32	2H32	A1	H10-200	H10-200	H10-200		H10-200	
L36-HB50(C)	240x430	2H25	-	-	2H20	-	-	A1	H10-100	-	-	CANT	L36-VB32-3	200x500x425	2H32	2H32	2H32	2H32	2H32	2H32	A1	H10-200	H10-200	H10-200		MFSF	
L36-HB86	200x425	2H16	2H16	2H16	2H16	2H16	2H16	A1	H10-200	H10-200	H10-200	SF	L36-VB31	350x665	2H32+2H32	2H32+2H32	2H32+2H32	2H32	2H32	2H32	A1	H13-150	H13-150	H13-150		SF	
L36-HB75a(C)	240x1480	2H20	-	-	2H20	-	-	A1	H10-100	-	-	H13-200	CANT	L36-VB36	200x665	2H16	2H16	2H16	2H32	2H32	2H32	A1	H10-200	H10-200	H10-200		SF
L36-HB76a(C)	225x1480	2H20	-	-	2H20	-	-	A1	H10-100	-	-	H13-200	CANT	L36-VB37	200x665x430	2H16	2H16	2H16	2H16	2H16	2H16	A1	H10-200	H10-200	H10-200		SF
L36-HB88(C)	285x1480	2H20+2H20	-	-	2H16+2H16	-	-	A1	H10-100	-	-	H13-200	CANT	L36-VB38	200x480	2H20	2H20	2H20	2H20	2H20	2H20	A1	H10-200	H10-200	H10-200		SF
L36-HB89(C)	240x1480	2H20	-	-	2H20	-	-	A1	H10-100	-	-	H13-200	CANT	L36-VB39	200x480	2H16	2H16	2H16	2H20	2H20	2H20	A1	H10-200	H10-200	H10-200		SF
L36-HB87	225x450	2H20	2H20	2H20	2H20	2H20	2H20	A1	H10-200	H10-200	H10-200	SF	L36-VB40	200x430x665	2H16	2H16	2H16	2H16	2H16	2H16	A1	H10-200	H10-200	H10-200		SF	
													L36-VB75a(C)	225x400	2H32	-	-	2H32	-	-	A1	H13-100	-	-		CANT	

PE'S CERTIFICATION

PROFESSIONAL ENGINEER
CIVIL
FOONG KIT KUEN
4340
SINGAPORE

AC'S CERTIFICATION

ACCREDITED CHECKER
NO: 1089

FOR CONSTRUCTION
29 Jun 2026
TECHNICAL
WOH HUP (PRIVATE) LIMITED
MARINA VIEW RESIDENCES (MVR)

KOK KING MIN
In AC Organisation
Registration No: A054
BUILDING CONTROL ACT
SINGAPORE

CONSTRUCTION SKETCH

ISSUED
29 JUNE 2026
KTP CONSULTANTS PTE. LTD.

2	REVISED BEAM DETAILS				01.06.26
1	REVISED BEAM DETAILS				10.03.25
REV	AMENDMENTS	OR	DES	CHK	DATE

PROJECT

PROPOSED NEW ERECTION OF 51 STOREY MIXED USE DEVELOPMENT COMPRISING 5 STOREY HOTEL AND CARPARK PODIUM, 9 STOREY HOTEL (350 ROOMS), 36/37 STOREY RESIDENTIAL FLATS (683 UNITS) AND 2 BASEMENTS ON LOTS 00483K AND 00484N TS 30 AND SUBTERRANEAN SPACE LOT 800772C TS 30 AT MARINA VIEW (DOWNTOWN CORE PLANNING AREA)

ARCHITECT
ARCHITECT 61 PTE. LTD.

KTP
KTP Consultants Pte Ltd
Surbana Jurong Campus 38 Cleantech Loop, #01-31 Singapore 636741
Tel : +65 6248 1288

DRAWN: CH DATE: DESIGNED: JS/AP/PS
SCALE: 1:100 CHECKED: ChewAL


DWG. NO. 21.070/L36B2

LEVEL-36 TO L38 BEAM SCHEDULE-2


THE OWNERSHIP OF THE COPYRIGHT IN THIS DRAWING IS RETAINED BY KTP CONSULTANTS WHOSE CONSENT MUST BE SOUGHT BEFORE ANY USE OR REPRODUCTION OF THE DRAWING OR ANY PART THEREOF CAN BE MADE.




SCALE : 1:25

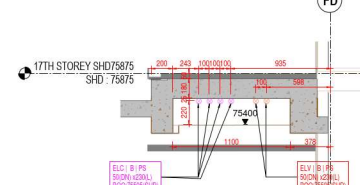


6 Recess Beam -Sec 06
1 : 25

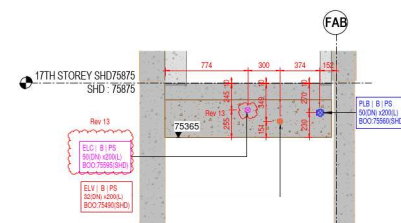


11 Unit Main Door Section - 14
1:25

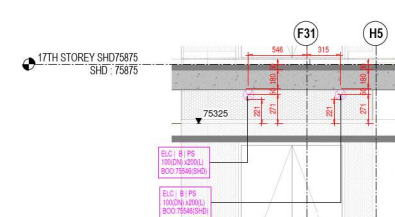


14 Section - 17
1 : 25

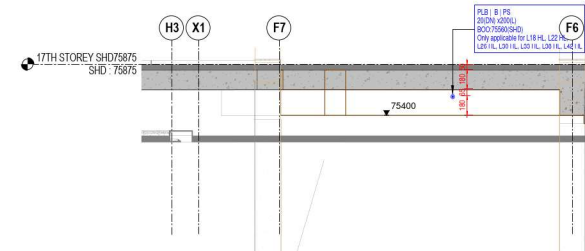


15 Section - 18
1 : 25

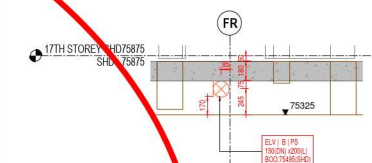

17 Section - 20
1 : 25

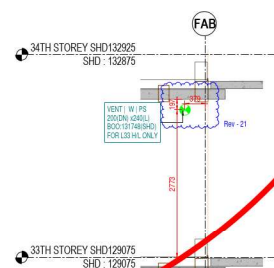

21 Section - 30
1 : 50

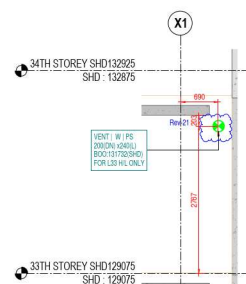

22 Section - 31
1 : 50
