



Cut & Bend Rebar – JOB ADVICE

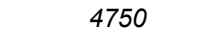
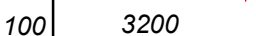
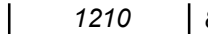
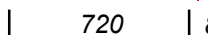
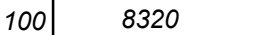
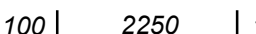
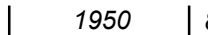
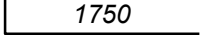
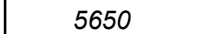
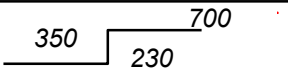
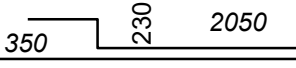
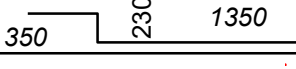
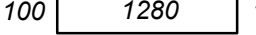
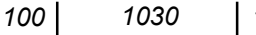
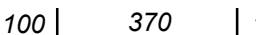
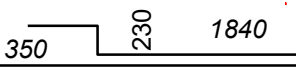
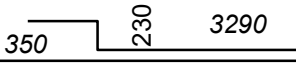
工作通知 Fax:6261 9133

BBS No 钢筋加工表	<u>MVR-TT-H313</u>	Total Weight 总重量	<u>890</u>
Contract 合同号码		Total Pages Attached 统计页数	1+6
Customer 承包商	<u>WOH HUP PTE LTD</u>	Gate:	
Project Title 施工地址	<u>MARINA VIEWLP 28F 1 STRAITS BIVD,SINGAPORE 018906</u>		
Description 形容	L37层CJ4-2 板 B1		
Date Order 订单日期	24-Aug-2026	Date Required 交货日期	31-Aug-2026
Remarks 评论			
Check/Approved By 检查/审核/订货人	<u>Zhou Bing</u>	Handphone 手提电话	<u>9847 1699</u>
Site Contact Person 联络人	<u>Kumar</u>	Handphone 手提电话	<u>8133 8587</u>
Material Receiver 收货人	<u>SIVA</u>	Handphone 手提电话	<u>8426 2921</u>
Site Telephone 工地电话		Site Fax No 传真号码	
Scheduler 开料人	<u>Lu Yong Bing</u>	Handphone 手提电话	<u>8982 7022</u>
<u>***Please Allow 5 days for ??? To Process Your Order***</u>			
<u>51 Tuas South Street 5,Singapoer637644</u>			

Name	Contact numbers	Email Address
project Coodinator	Leslie LIM	8524 2927



PROJECT :	MARINA VIEWLP 28F 1 STRAITS BIVD,SINGAPORE 018906		Pg. 1 / 6
BBS No:	MVR-TT-H313	Rev.	Date : 2026/8/24
Dwg. No.		Rev.	Prepared By:
TITLE:	L37层CJ4-2 板 B1		BBS NO: MVR-TT-H313

BAR BENDING SCHEDULE									
MEMBER	BAR MARK	TYPE & SIZE	NO. OF MBRS	NO.O F EACH	TOTAL	SHAP E CODE	SHAPE	CUT OFF LENGTH	WEIGHT
					B1				
	43	H 10	1	3	3	20		4750	8.78
	44	H 10	1	3	3	37		3300	6.10
	45	H 10	1	5	5	38a		1370	4.22
	46	H 10	1	8	8	38a		880	4.34
	47	H 10	1	12	12	37		8420	62.24
	48	H 10	1	2	2	38a		2450	3.02
	49	H 10	1	14	14	38a		2110	18.20
	50	H 10	1	14	14	37		1830	15.78
	51	H 10	1	6	6	37		5730	21.18
	52	H 10	1	2	2	54		1280	1.58
	53	H 10	1	1	1			2730	1.68
	54	H 10	1	4	4			2030	5.00
	55	H 10	1	1	1	38a		1480	0.91
	56	H 10	1	2	2	38a		1230	1.52
	57	H 10	1	3	3	38a		570	1.05
	58	H 10	1	3	3			2520	4.66
	59	H 10	1	3	3			3970	7.34

REBAR SIZE		R06	H08	H10	H13	H16	H20	H25	H32	H40	TOTAL
WEIGHT				####							167.6 KG



PROJECT :		MARINA VIEWLP 28F 1 STRAITS BIVD,SINGAPORE 018906	Pg. 2 / 6
BBS No:		MVR-TT-H313	Rev. Date : 2026/8/24
Dwg. No.			Rev. Prepared By:
TITLE:		L37层CJ4-2 板 B1	BBS NO: MVR-TT-H313

BAR BENDING SCHEDULE



















MEMBER	BAR MARK	TYPE & SIZE	NO. OF MBRS	NO. OF EACH	TOTAL	SHAPE CODE	SHAPE	CUT OFF LENGTH	WEIGHT
	60	H 10	1	2	2			3580	4.41
	61	H 10	1	11	11	38a		5540	37.54
	62	H 10	1	1	1	53		6540	4.03
	63	H 10	1	1	1	20		6500	4.00
	64	H 10	1	18	18	37		6550	72.63
	65	H 10	1	18	18	20		6250	69.30
	66	H 10	1	2	2	38a		3200	3.94
	67	H 10	1	4	4	38a		1600	3.94
	68	H 10	1	11	11	37		1370	9.28
	69	H 10	1	11	11			1100	7.45
	70	H 10	1	13	13	38a		2020	16.18
	71	H 10	1	13	13	38a		2020	16.18
	72	H 10	1	2	2	38a		3200	3.94
	73	H 10	1	11	11	37		1370	9.28
	74	H 10	1	11	11			1100	7.45
	75	H 10	1	4	4	38a		1600	3.94
	76	H 10	1	13	13	38a		1130	9.05
	77	H 10	1	2	2	54		880	1.08

REBAR SIZE		R06	H08	H10	H13	H16	H20	H25	H32	H40	TOTAL
WEIGHT				####							283.6 KG



















PROJECT :	MARINA VIEWLP 28F 1 STRAITS BIVD,SINGAPORE 018906		Pg. 3 / 6
BBS No:	MVR-TT-H313	Rev.	Date : 2026/8/24
Dwg. No.		Rev.	Prepared By:
TITLE:	L37层CJ4-2 板 B1		BBS NO: MVR-TT-H313

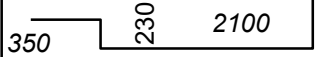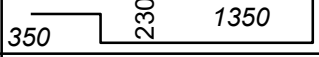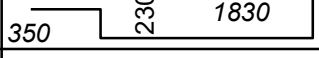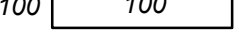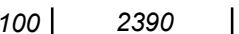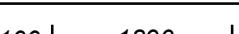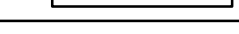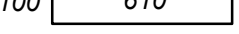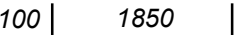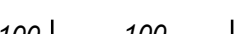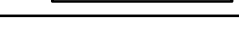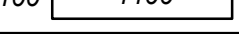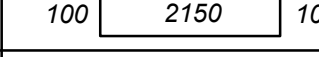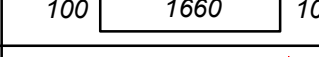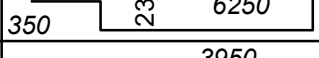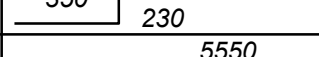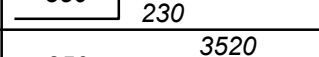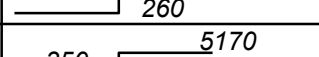BAR BENDING SCHEDULE

MEMBER	BAR MARK	TYPE & SIZE	NO. OF MBRS	NO. OF EACH	TOTAL	SHAPE CODE	SHAPE	CUT OFF LENGTH	WEIGHT
	78	H 10	1	1	1			2780	1.71
	79	H 10	1	4	4			2030	5.00
	80	H 10	1	3	3			2510	4.64
	81	H 10	1	2	2	38a		300	0.37
	82	H 10	1	2	2	38a		2590	3.19
	83	H 10	1	2	2	38a		2090	2.57
	84	H 10	1	3	3	38a		810	1.50
	85	H 10	1	1	1	38a		2050	1.26
	86	H 10	1	2	2	38a		300	0.37
	87	H 10	1	4	4	38a		1300	3.20
	88	H 10	1	1	1	38a		2350	1.45
	89	H 10	1	2	2	38a		1860	2.29
	90	H 10	1	1	1			6930	4.27
	91	H 10	1	2	2	54		4530	5.58
	92	H 10	1	2	2	54		6130	7.55
	93	H 10	1	1	1	54		4130	2.54
	94	H 10	1	1	1	54		5780	3.56
	95	H 10	1	1	1	53		7150	4.40

REBAR SIZE		R06	H08	H10	H13	H16	H20	H25	H32	H40	TOTAL
WEIGHT				55.5							55.5 KG

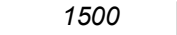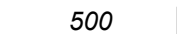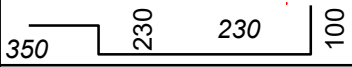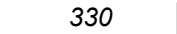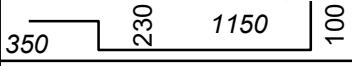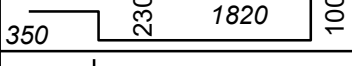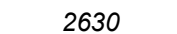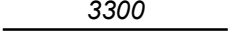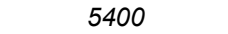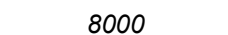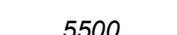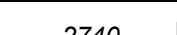  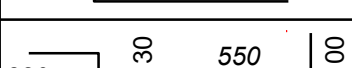 

PROJECT :		MARINA VIEWLP 28F 1 STRAITS BIVD,SINGAPORE 018906							Pg. 4 / 6	
BBS No:		MVR-TT-H313					Rev.		Date : 2026/8/24	
Dwg. No.							Rev.		Prepared By:	
TITLE:		L37层CJ4-2 板 B1							BBS NO: MVR-TT-H313	
BAR BENDING SCHEDULE										
MEMBER	BAR MARK	TYPE & SIZE	NO. OF MBRS	NO. OF EACH	TOTAL	SHAPE CODE	SHAPE		CUT OFF LENGTH	WEIGHT
	96	H 10	1	1	1	38a	100		1700	1.05
	97	H 10	1	4	4	38a	100		700	1.72
	98	H 10	1	5	5			910	2.80	
	99	H 10	1	4	4	38a	100		530	1.31
	100	H 10	1	1	1			1830	1.13	
	101	H 10	1	3	3			2500	4.62	
	102	H 10	1	11	11	37	170		2800	18.97
	103	H 10	1	1	1	20			3300	2.03
	104	H 10	1	1	1	20			5400	3.33
	105	H 10	1	18	18	20			8000	88.70
	106	H 10	1	4	4	37	100		5600	13.80
	107	H 10	1	3	3	38a	100		2940	5.43
	108	H 10	1	9	9	38a	100		1560	8.65
	109	H 10	1	5	5	37	100		1530	4.71
	110	H 10	1	5	5			1100	3.39	
	111	H 10	1	14	14	38a	100		2430	20.96

REBAR SIZE		R06	H8	H10	H13	H16	H20	H25	H32	H40	TOTAL
WEIGHT				####							182.6 KG



PROJECT :	MARINA VIEWLP 28F 1 STRAITS BIVD,SINGAPORE 018906		Pg. 5 / 6
BBS No:	MVR-TT-H313	Rev.	Date : 2026/8/24
Dwg. No.		Rev.	Prepared By:
TITLE:	L37层CJ4-2 板 B1		BBS NO: MVR-TT-H313

BAR BENDING SCHEDULE									
MEMBER	BAR MARK	TYPE & SIZE	NO. OF MBRS	NO. OF EACH	TOTAL	SHAPE CODE	SHAPE	CUT OFF LENGTH	WEIGHT
							洞加B		
	17	H 16	1	2	2	37	780 1280	2060	6.51
	18	H 16	1	2	2	37	250 1650	1900	6.00
	19	H 16	1	1	1	38	500 350 600	1450	2.29
	20	H 16	1	1	1	20	2580	2580	4.07
	21	H 16	1	2	2	20	2580	2580	8.15
	22	H 16	1	1	1	37	1100 1300	2400	3.79
	23	H 16	1	2	2	54	250 1300 530	2080	6.57
	24	H 16	1	2	2	20	2400	2400	7.58
	25	H 16	1	2	2	20	3200	3200	10.11
	25a	H 16	2	2	4	20	2700	2700	17.05
	26	H 16	2	2	4	20	2180	2180	13.77
	27	H 16	2	1	2	37	1100 1300	2400	7.58
	28	H 16	1	1	1	38a	600 2390 600	3590	5.67
	28a	H 16	1	1	1	38a	530 2350 530	3410	5.38
	29	H 16	1	1	1	20	4960	4960	7.83
	30	H 16	1	2	2	20	4960	4960	15.66



REBAR SIZE		R06	H08	H10	H13	H16	H20	H25	H32	H40	TOTAL
WEIGHT						####					128 KG






PROJECT :	MARINA VIEWLP 28F 1 STRAITS BIVD,SINGAPORE 018906		Pg. 6 / 6
BBS No:	MVR-TT-H313	Rev.	Date : 2026/8/24
Dwg. No.		Rev.	Prepared By:
TITLE:	L37层CJ4-2 板 B1		BBS NO: MVR-TT-H313

BAR BENDING SCHEDULE									
MEMBER	BAR MARK	TYPE & SIZE	NO. OF MBRS	NO. OF EACH	TOTAL	SHAPE CODE	SHAPE	CUT OFF LENGTH	WEIGHT
	31	H 16	2	1	2	37	650 1670	2320	7.33
	32	H 16	1	2	2	20	2180	2180	6.88
	33	H 16	1	2	2	20	2340	2340	7.39
	34	H 16	1	2	2	37	1030 1100	2130	6.73
	35	H 16	1	1	1	38	500 350 600	1450	2.29
	36	H 16	1	1	1	20	2340	2340	3.69
	37	H 16	1	2	2	20	3180	3180	10.04
	38	H 16	1	1	1	38	400 1750 1130	3280	5.18
	39	H 16	1	2	2	20	2340	2340	7.39
	40	H 16	1	1	1	38	250 1300 400	1950	3.08
	41	H 16	1	2	2	20	2340	2340	7.39
	42	H 16	1	2	2	20	1610	1610	5.08

REBAR SIZE		R06	H08	H10	H13	H16	H20	H25	H32	H40	TOTAL
WEIGHT						72.5					72.5 KG

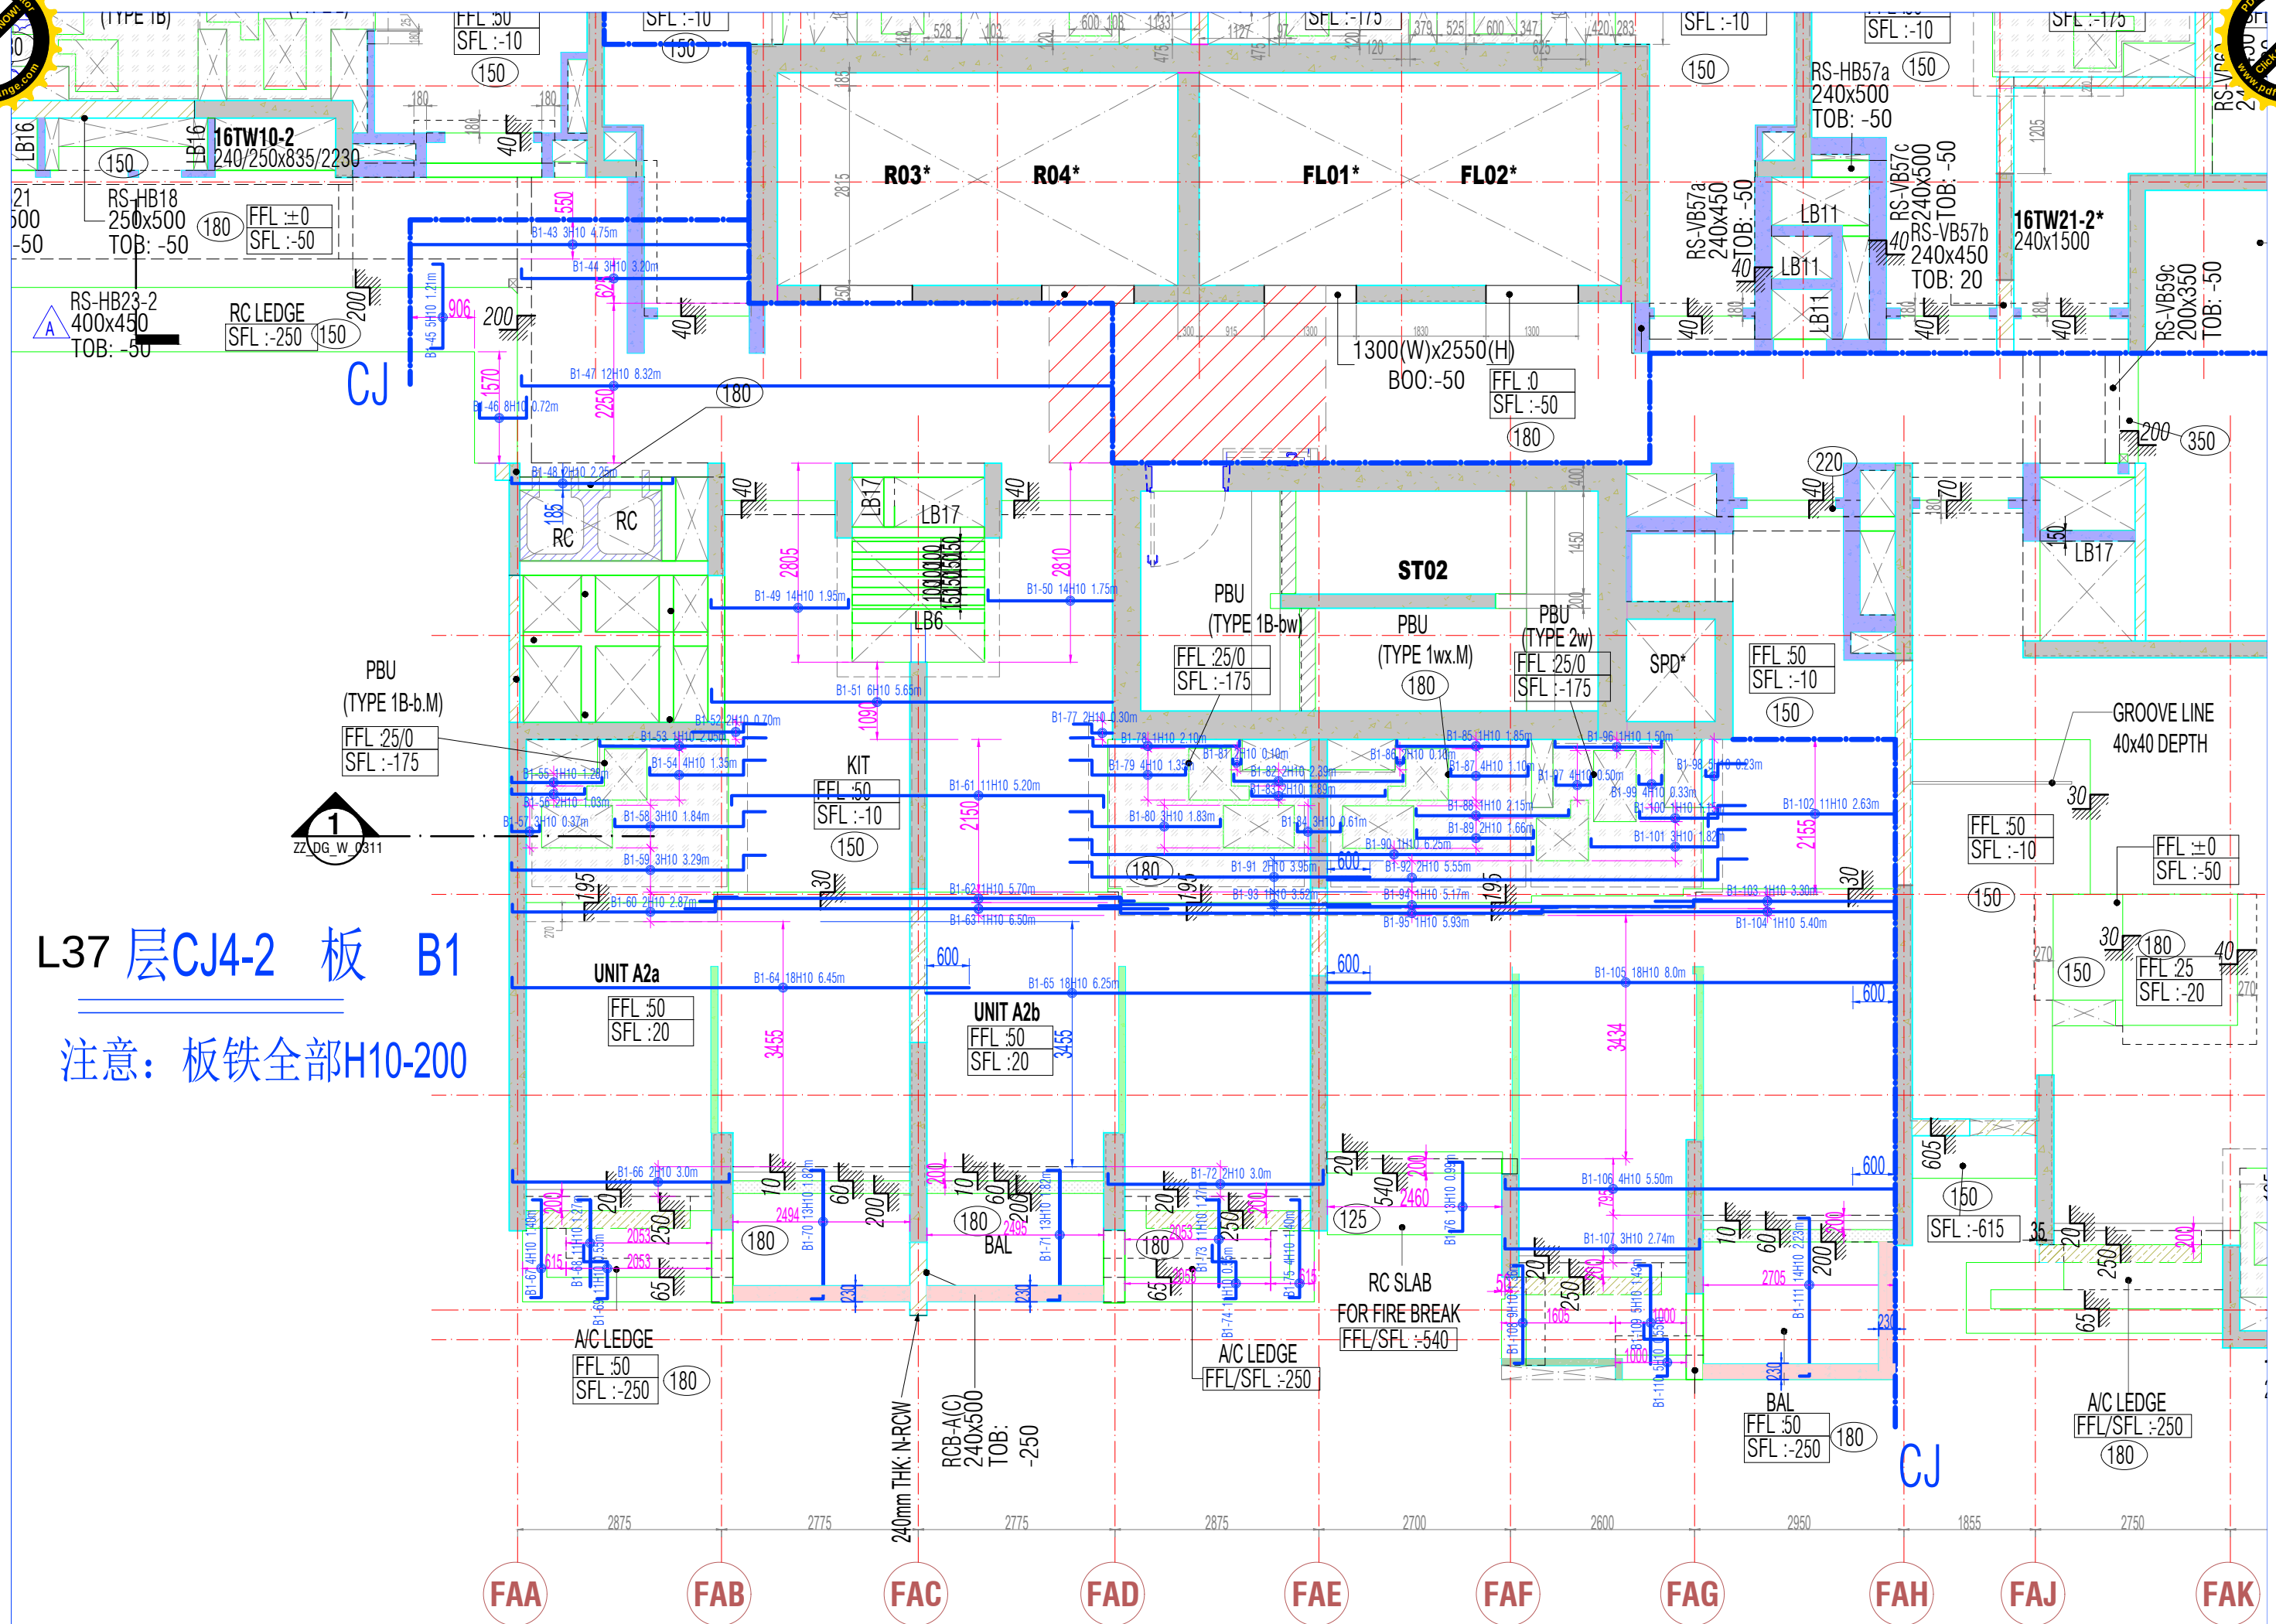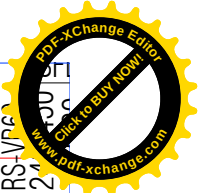

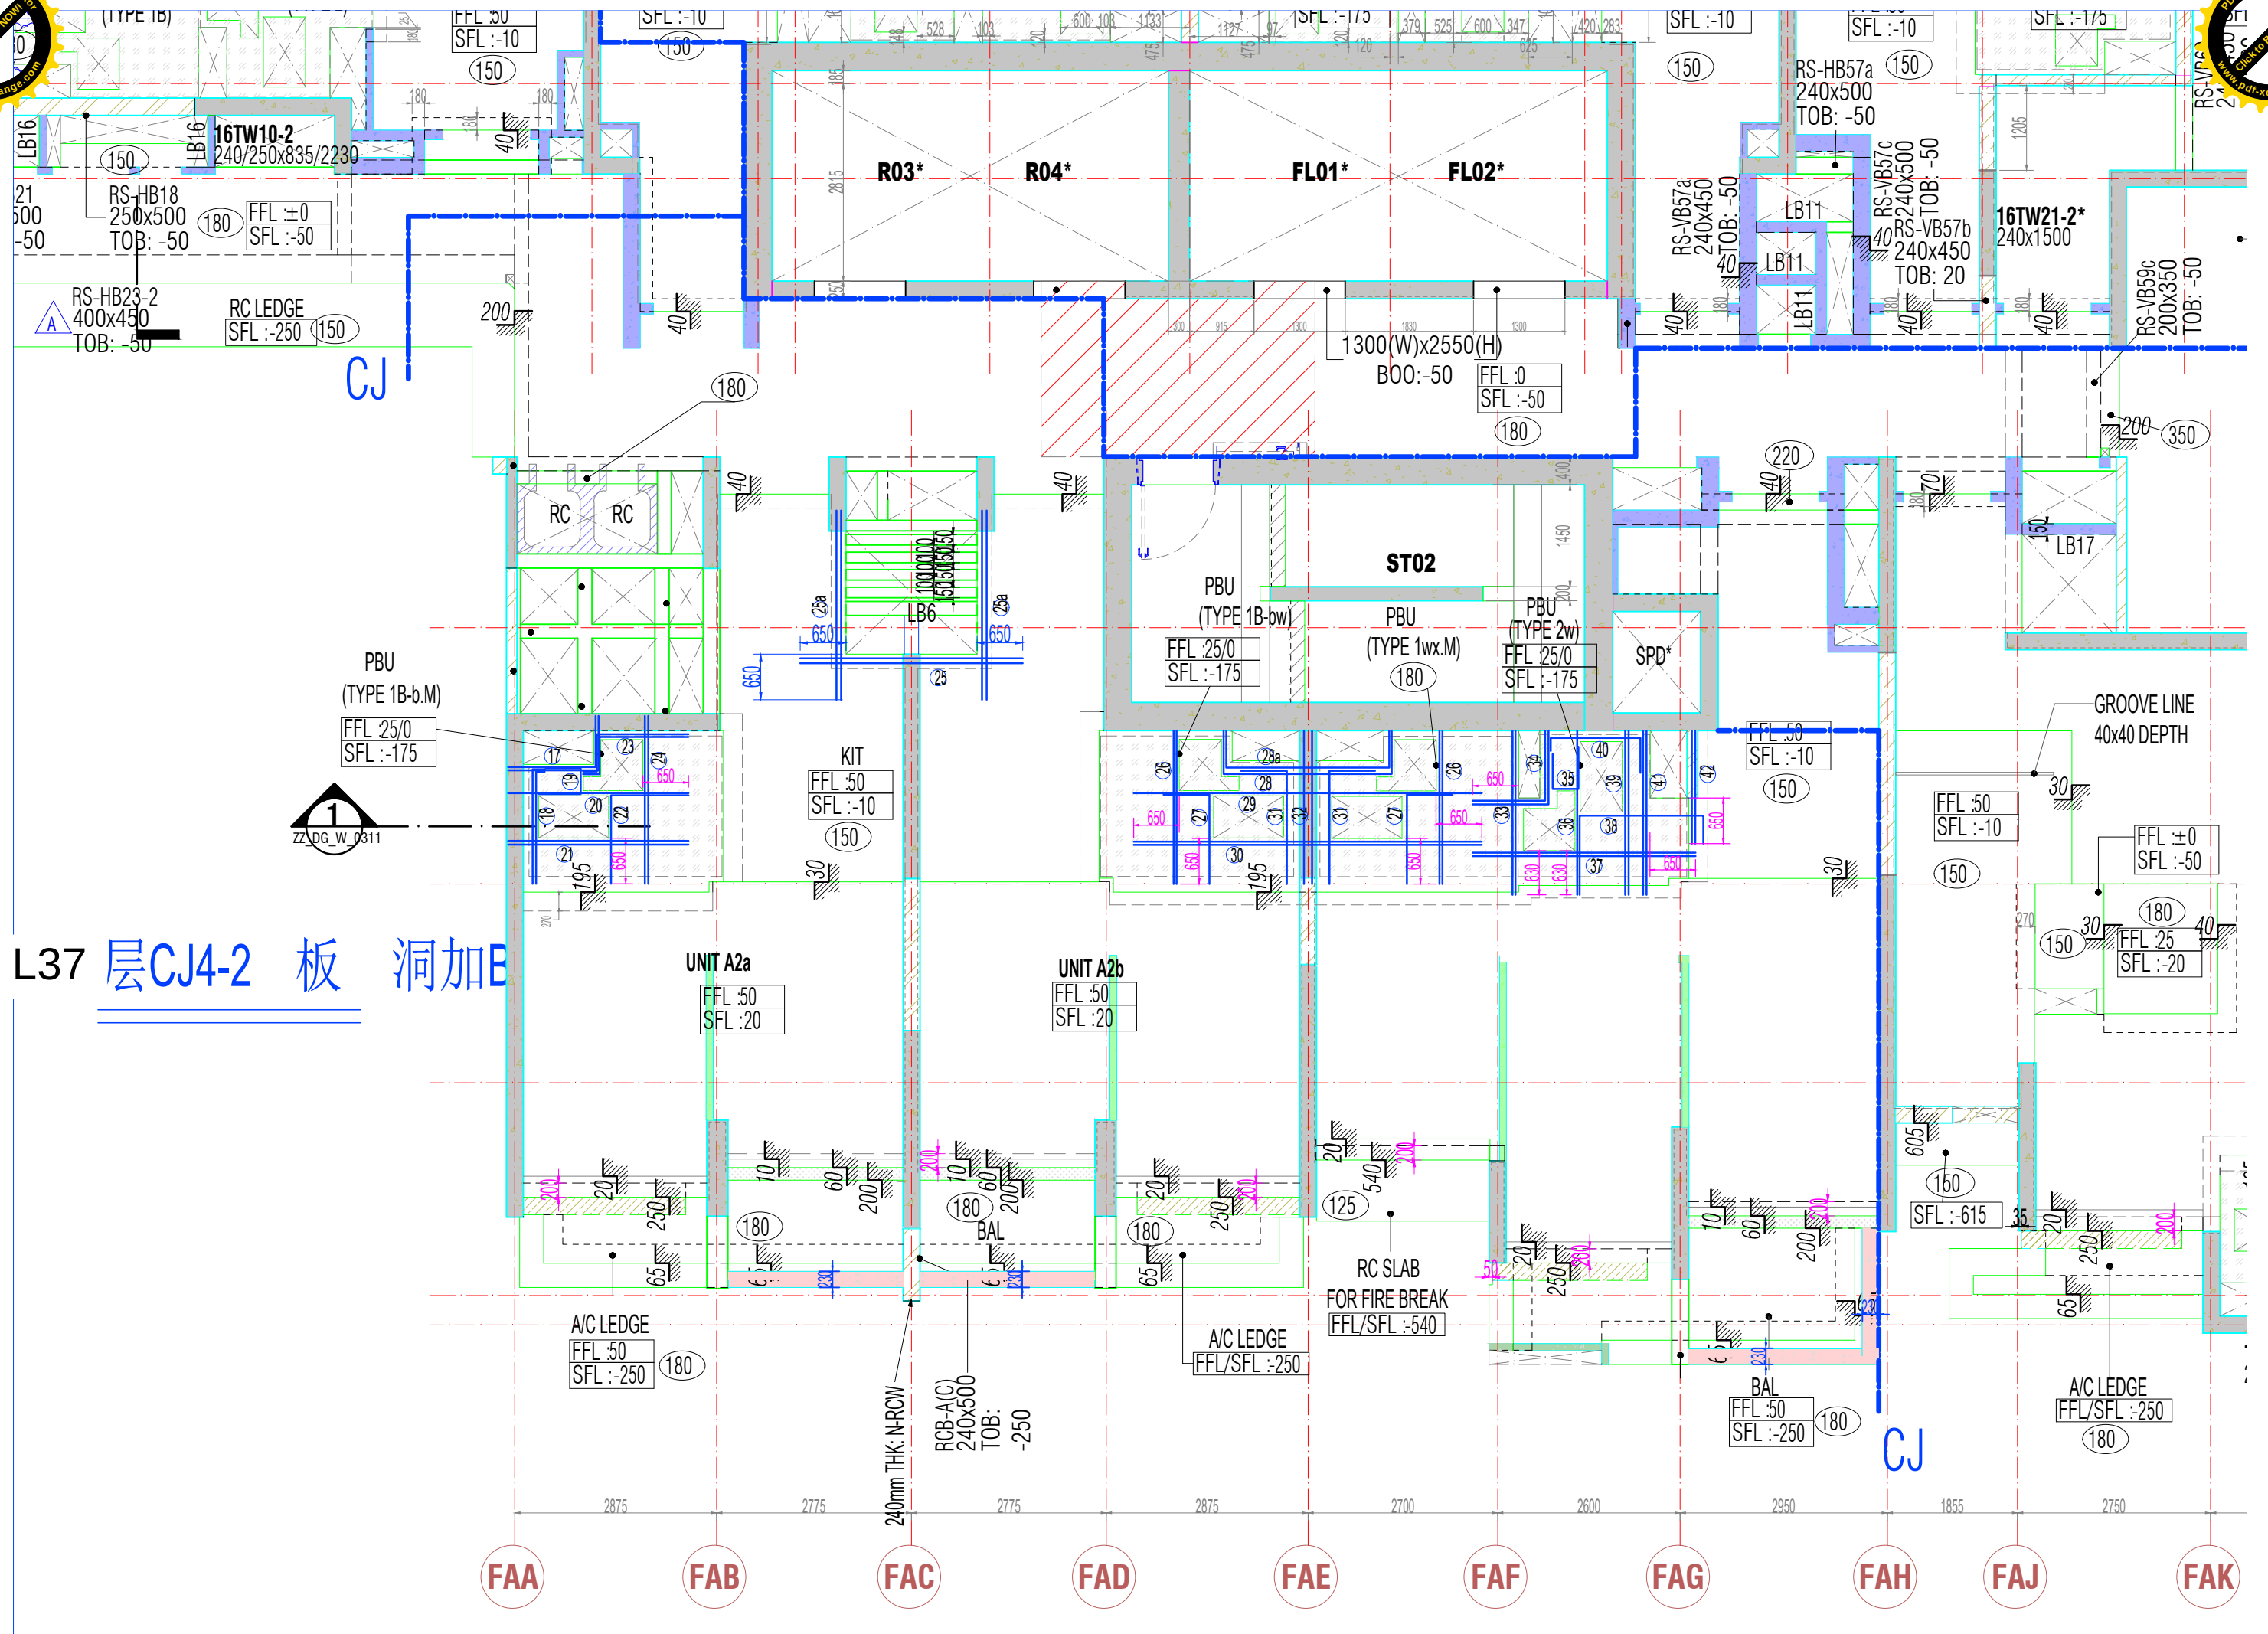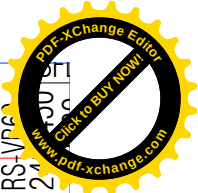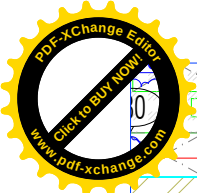



洞加B:

- ①7 2H16 1.28/0.78m

①8 2H16 1.65/0.25m

①9 1H16 0.60/0.35/0.50m

②0 1H16 2.58m

②1 2H16 2.58m

②2 1H16 1.10/1.30m

②3 2H16 1.30/0.53/0.25m

②4 2H16 2.40m

②5 2H16 3.20m

②5a 2*2H16 2.70m
- ②6 2*2H16 2.18m

②7 2*1H16 1.30/1.10m

②8 1H16 0.60/2.39/0.60m

②8a 1H16 0.53/2.35/0.53m

②9 1H16 4.96m

③0 2H16 4.96m

③1 2*1H16 1.67/0.65m

③2 2H16 2.18m
- ③3 2H16 2.34m

③4 2H16 1.03/1.10m

③5 1H16 0.60/0.35/0.50m

③6 1H16 2.34m

③7 2H16 3.18m

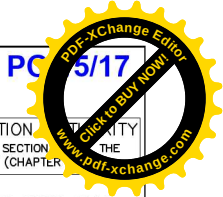
③8 1H16 1.13/1.75/0.40m

③9 2H16 2.34m

④0 1H16 0.25/1.30/0.40m

④1 2H16 2.34m

④2 2H16 1.61m



- NOTES:
- UNLESS NOTED OTHERWISE, SLAB REINFORCEMENTS SHALL BE H10-200 (B/W).
 - SLAB THICKNESS SHALL BE 180.
 - REINFORCEMENT LAPPING LENGTH TO BE TL.
 - FOR REINF. THAT EXCEEDS 12m, THE LAPPING SHOULD BE DONE WHERE STRESS IS LESS. THE LAPPING OF TOP REINFORCEMENT SHOULD BE AWAY FROM SUPPORTS WHERE STRESS IS HIGH.
 - DENOTES ADDITIONAL REINFORCEMENT.
 - TRIMMER BARS FOR OPENINGS, REFER TO DWG. NO. 21.070/N2 FOR DETAILS.

BUILDING AND CONSTRUCTION, APPROVED UNDER SECTION 5 / SECTION BUILDING CONTROL ACT (CHAPTER

Project Ref No : A1252-00566-2022-ST19

for Commissioner of Building Control

PE'S CERTIFICATION



AC'S CERTIFICATION

ACCREDITED CHECKER

NO: 1089

KOK KING MIN
In AC Organisation
Registration No: A054
BUILDING CONTROL ACT
SINGAPORE

CONSTRUCTION SKETCH

ISSUED

19 SEPT 2025

CONSULTANTS PTE. LTD.

2	REVISED SLAB REINFORCEMENT	17/09/25
1	REVISED SLAB REINFORCEMENT	05/03/25
REV	AMENDMENTS	DR DES CHK DATE

PROJECT

PROPOSED NEW ERECTION OF 51 STOREY MIXED USE DEVELOPMENT COMPRISING 5 STOREY HOTEL AND CARPARK PODIUM, 9 STOREY HOTEL (350 ROOMS), 36/37 STOREY RESIDENTIAL FLATS (683 UNITS) AND 2 BASEMENTS ON LOTS 00483K AND 00484N TS 30 AND SUBTERRANEAN SPACE LOT 800772C TS 30 AT MARINA VIEW (DOWNTOWN CORE PLANNING AREA)

ARCHITECT

ARCHITECT 61 PTE. LTD.



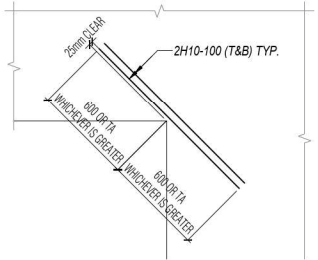
KTP Consultants Pte Ltd
Surbana Jurong Campus 38 Cleantech
Loop, #01-31 Singapore 638741
Tel : +65 6248 1288

DRAWN: CH DATE: DESIGNED: JS/AP/FS
SCALE: 1:150 CHECKED: ChewAL

DWG. NO. 21.070/L17S2

LEVEL - 17 TO L33, L36 TO L48 TYPICAL SLAB BOTTOM REINFORCEMENT LAYOUT

THE OWNERSHIP OF THE COPYRIGHT IN THIS DRAWING IS RETAINED BY KTP CONSULTANTS WHOSE CONSENT MUST BE SOUGHT BEFORE ANY USE OR REPRODUCTION OF THE DRAWING OR ANY PART THEREOF CAN BE MADE.




TYPICAL TRIMMER BARS AT RE-ENTRANT CORNER

SCALE : 1:25

LEVEL - 17 TO L33, L36 TO L48 TYPICAL SLAB BOTTOM REINFORCEMENT LAYOUT

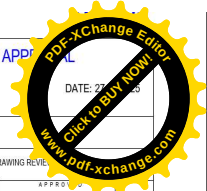SCALE : 1:150



1:17TH - 33RD, 36TH - 48TH STOREY CONCRETE BODY PLAN

1:17TH - 33RD, 36TH - 48TH STOREY CONCRETE BODY PLAN
SCALE 1:100

Autodesk Docs://MVR/MVR_PJW_CO_WH_CST_ZZ_ZZ_M3_W_0005_L17 to L33, L36 to L48.rvt

Typ Resi PBU Slab Fold Opening Trimmer Bar Details

- Copy to
1. PD - Chen Han Qi
 2. SPM/PM
 3. SE
 4. RE/RTO
 5. All Subcon
 6. WH MVR
 7. WH QS
 8. WH Rebar Scheduler
 9. DC
 10. IOI - Muliadi, How See, Darren

From: Calvin Yap
13-Aug-2025

FOR CONSTRUCTION

21 JAN 2026

TECHNICAL
WOH HUP (PRIVATE) LIMITED
MARINA VIEW RESIDENCES (MVR)

ABBREVIATION:

SPL - STRUCTURAL FLOOR LEVEL
PFL - PAVEMENT FLOOR LEVEL
BSL - BASE FLOOR LEVEL
USL - UPPER SLAB LEVEL
BSL - BELOW SLAB LEVEL
MOL - MID SLAB LEVEL
TOS - TOP OF BEAM
BOS - BOTTOM OF BEAM
LSP - LEFT SIDE OF BEAM
TOW - TOP OF WALL
BOO - BOTTOM OF OPENING
BSL - STRUCTURAL INVERT LEVEL
MOL - MASS CONCRETE LEVEL
TOP - TOP OF PILE CAP
TOP - TOP OF PLUMB
TO - TEMPORARY OPENING
PH - PASSENGER HOST

LEGEND

RC WALL / COLUMN
RC WALL / COLUMN BELOW
DOUBLE SLAB
MASS CONCRETE
NON-STRUCTURAL RC WALL
NON-STRUCTURAL RC WALL FOR AWLAWGATION
MSPK WALL/PARAPET WALL
RECESSES
DOWNHANG WALL
TEMPORARY BEAM
TEMPORARY SLAB
TEMPORARY OPENING
MID-HOLE
FOR COMPARISON / K.I.V.
REVISION
SLAB THICKNESS
HOLLOWCORE SLAB THICKNESS
PBU PATCH
WALL WITH 10mm SKIRTING RECESS
BSH SLAB STRENGTHENING BOUNDARY

GENERAL NOTES:

1. ALL DIMENSIONS ARE TO BE IN 'mm' UNLESS OTHERWISE STATED.
2. ALL DIMENSIONS ARE SUBJECT TO SITE VERIFICATION.
3. DO NOT SCALE ON DRAWINGS.
4. ANY DISCREPANCY MUST BE REPORTED TO MAIN CONTRACTOR IMMEDIATELY.
5. ALL DRAWINGS MUST BE USED IN CONJUNCTION WITH M&E AND STRUCTURAL DRAWINGS.

REVISION

NO.	DESCRIPTION	DATE
1	ISSUED FOR CONSTRUCTION	21 JAN 2026

REFERENCE DRAWING NO.:

1. ARCHITECTURAL REFERENCE DWG
2. STRUCTURAL REFERENCE DWG
3. M&E REFERENCE DWG
4. OTHERS

KEY PLAN

DEVELOPER/LAND OWNER:

Boulevard Development Pte Ltd
Boulevard Midtown Pte Ltd

38 Beach Road #14-11
Shangri-La Hotel, Singapore 188167
Tel: 65-6338-8111

ARCHITECT:

architects61
architecture planning

architect 61 pte ltd
150 Beach Road # 04-01
Tel: 65-6737-9877 Fax: 65-6732-5439 5439@architects61.com.sg www.a61.com.sg

CIVIL & STRUCTURAL ENGINEER:

KTP Consultants Pte Ltd
150 Beach Road, #04-01
Singapore 188167
Tel: 65-6732-5439 Fax: 65-6732-5439

MEP CONSULTANT:

three61
three61 Cost Management Pte Ltd
(Three61)
38 Chatterbox Lane
#02-01 Sushana Jaring Campus
Singapore 630141

QUANTITY SURVEYOR:

three61
three61 Cost Management Pte Ltd
(Three61)
38 Chatterbox Lane
#02-01 Sushana Jaring Campus
Singapore 630141

MAIL CONTRACTOR:

WOH HUP (PRIVATE) LIMITED
150 Beach Road, #04-01
Singapore 188167
Tel: 65-6732-5439 Fax: 65-6732-5439

PROJECT TITLE:

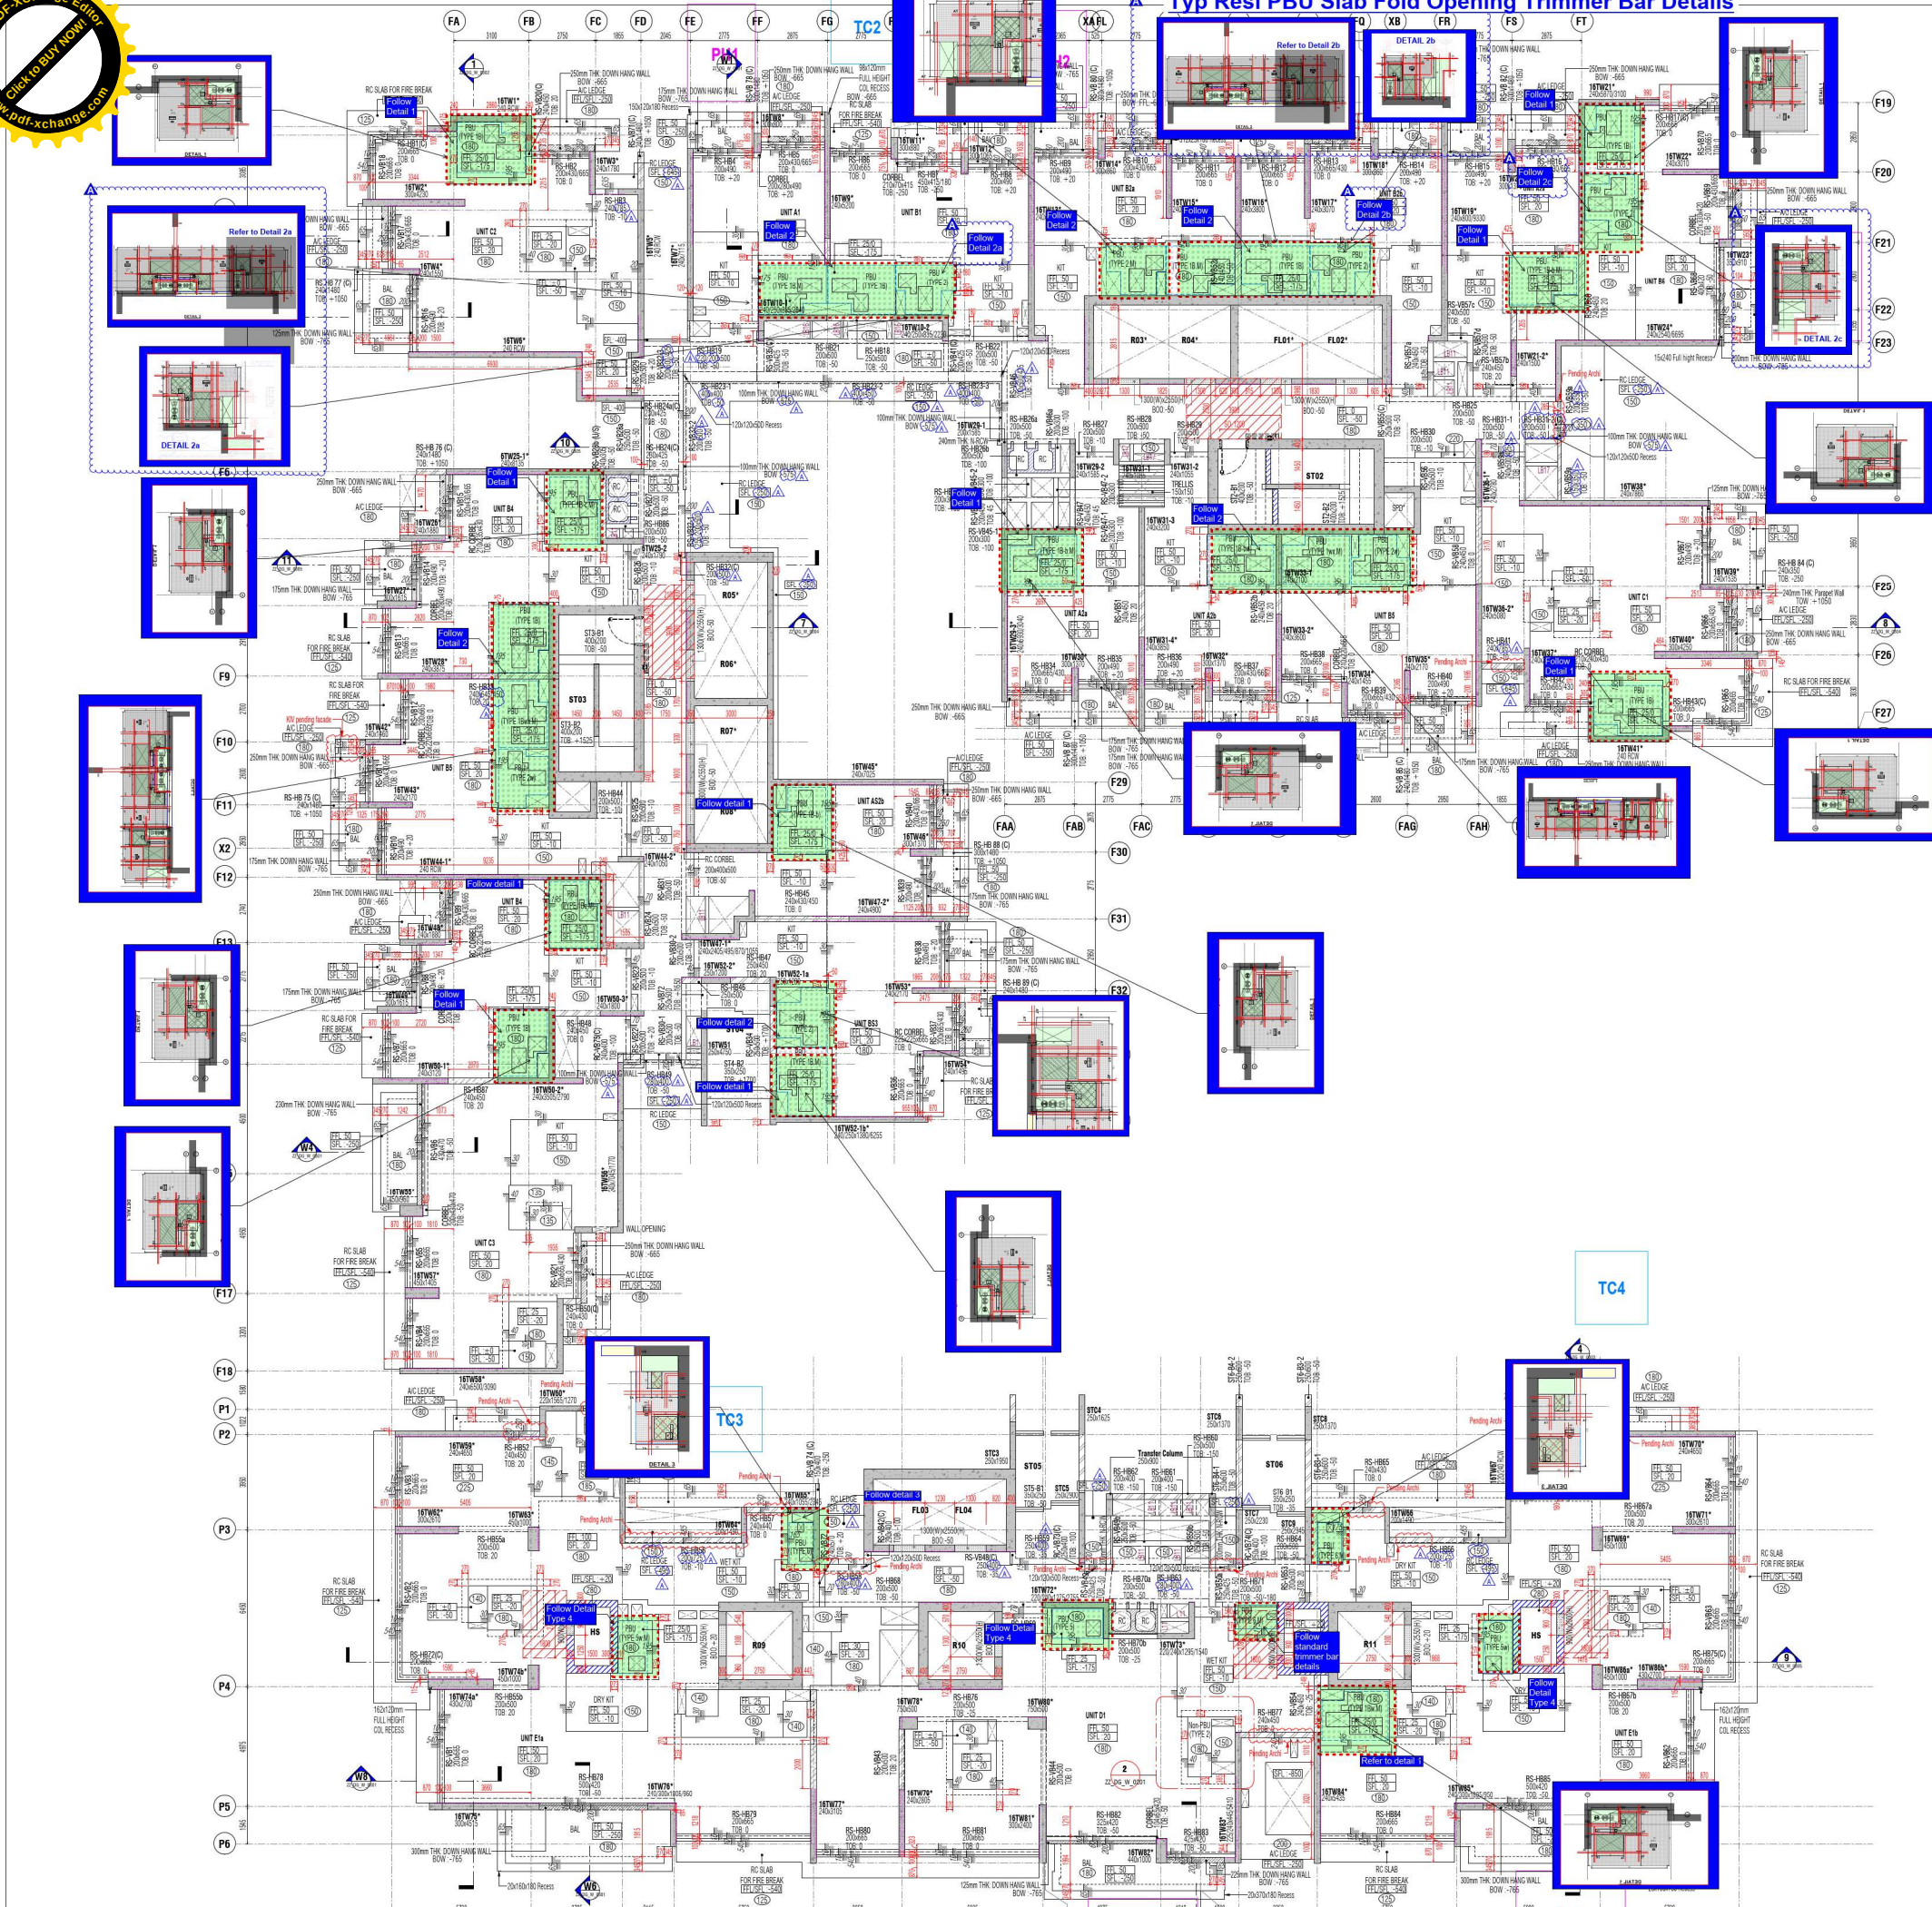
W RESIDENCES MARINA VIEW - SINGAPORE
PROPOSED NEW ERECTION OF 31 STOREY M&E USE DEVELOPMENT COMPRISING
31 STOREY RESIDENTIAL FLATS, 31 STOREY HOTEL, 31 STOREY HOTEL, 31 STOREY HOTEL
AND 31 STOREY HOTEL. THE PROJECT IS SITUATED ON LOT 000000 AND
000001 TO 31 AND 32 AT MARINA VIEW
CONCRETE BODY PLAN

DESIGNED: JC
DRAWN: PNT
DATE: 27.06.2025
DWG NO: MVR_CO_WH_CST_ZZ_ZZ_DG_W_0001
SCALE: As Indicated
SIZE: A0

CHECKED: HSJC
APPROVED: Approver
SCALE: As Indicated
SIZE: A0

REFERENCES:

Arch: 211214 Slab Fold Extension for WP (Kitchen)
M&E: 241216-ME_17TH-33TH STOREY - OVERALL PBU PENETRATION



KTP: No objection
KerkYX 20251223



MVR PJW CO WH CST ZZ ZZ SK W 2516A
Typ Resi PBU Slab Fold Opening Trimmer Bar Details



FOR CONSTRUCTION

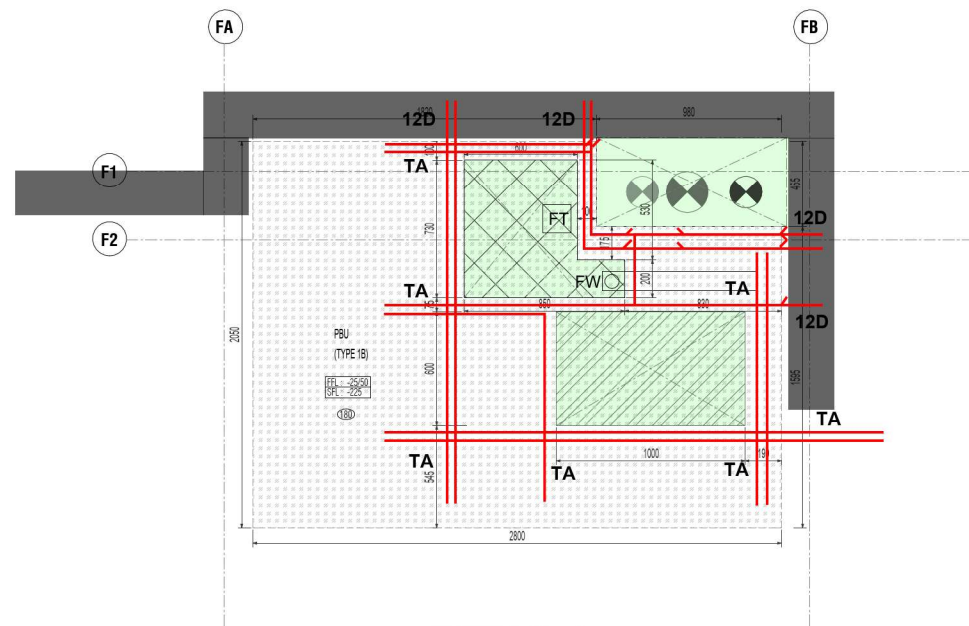
21 JAN 2026

TECHNICAL
WOH HUP (PRIVATE) LIMITED
MARINA VIEW RESIDENCES (MVR)


Copy to

1. PD - Chen Han Qi
2. PM - Wong Wei Siong
3. SE
4. RE/RTO
5. All Subcons
6. MVR WH, MVR Site
7. WH QS
8. WH Rebar Scheduler
9. DC
10. IOI - Muliadi, How See, Darren


From: Joseph Chin
24-Dec-25




DETAIL 1

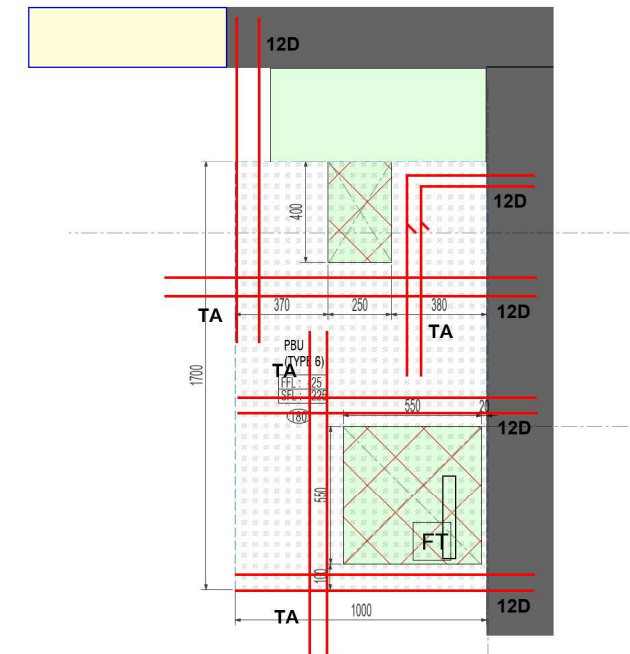

DETAIL 3

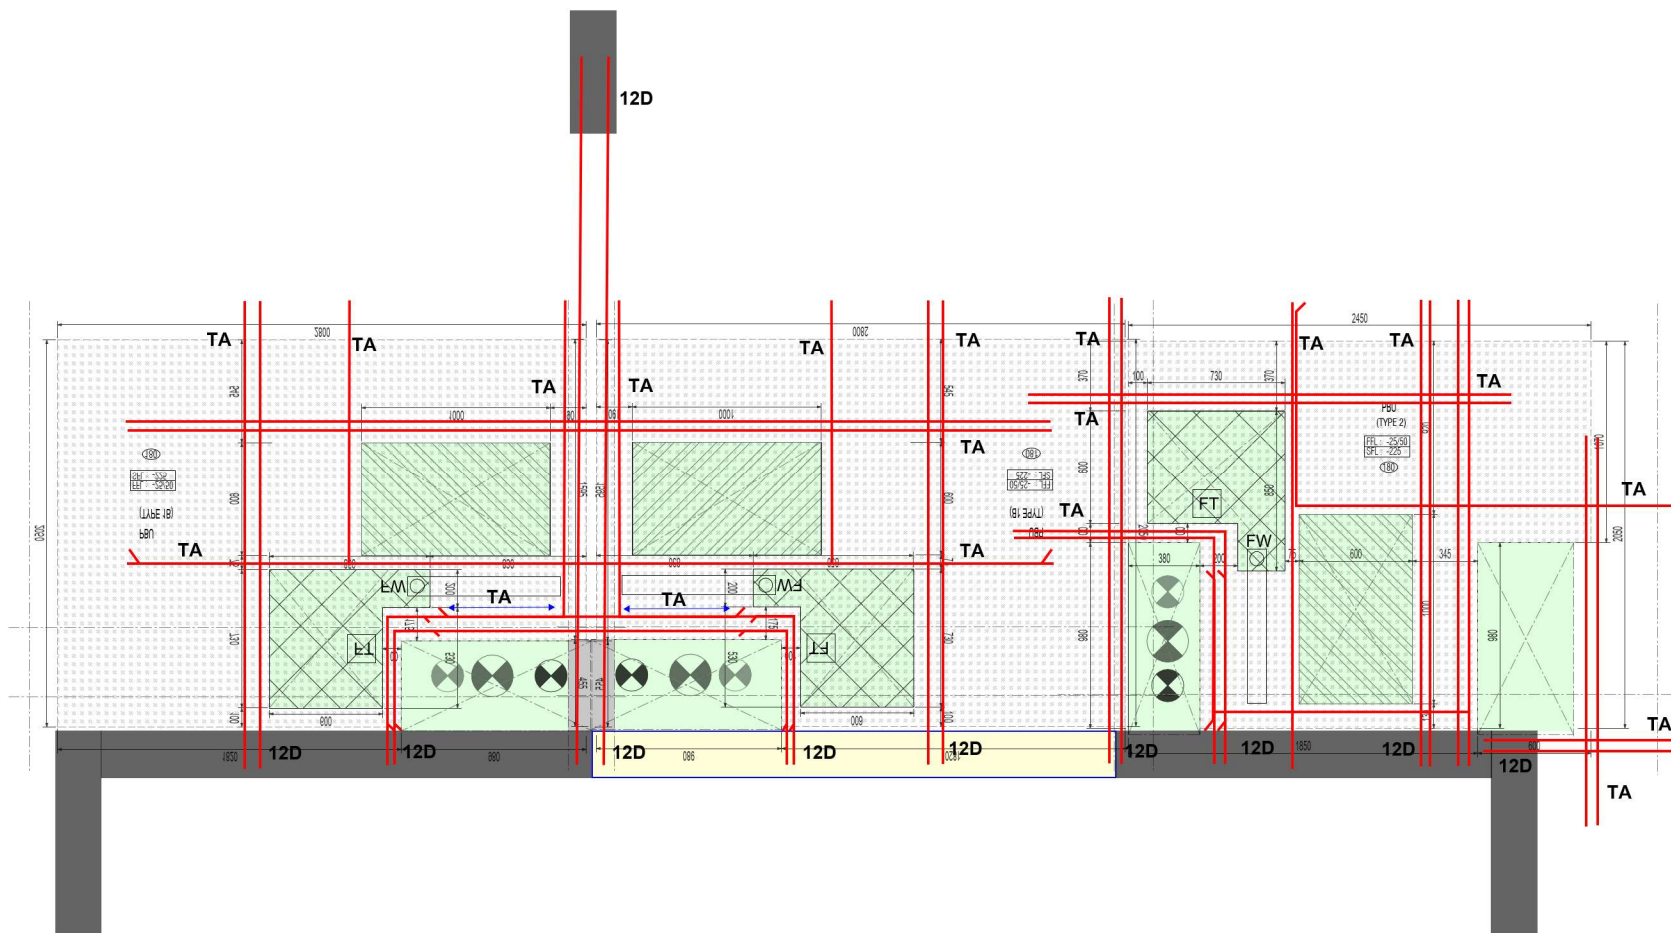

DETAIL 2

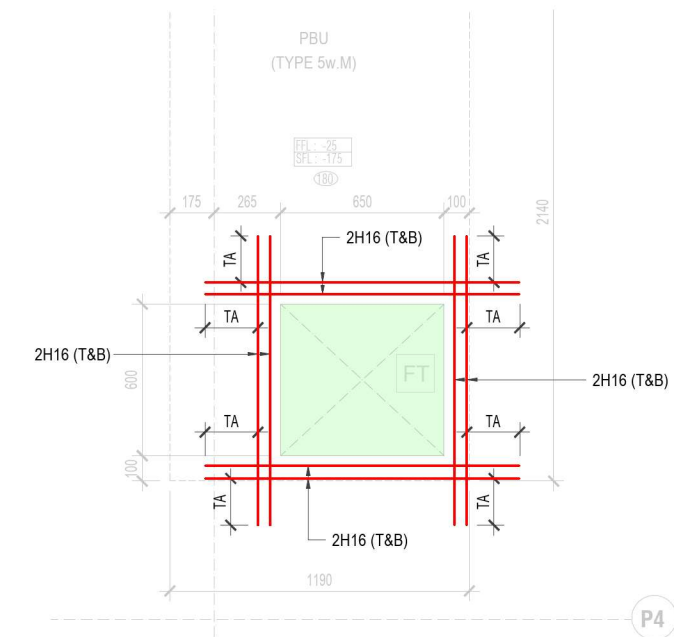

DETAIL 4

TYPICAL PBU TYPE 5w.M


SCALE : 1:15

EXTRACTED FROM ST19 BCA APPROVED DRAWING


Additional Notes:

1. All trimmer bars shall be H16 (T&B).
2. Starter bars provision for H16 trimmer bars from RC walls shall all be H13.
3. If trimmer bars anchored into beam or wall shall be 12D. All other cases shall be minimum TA.

KTP: No objection
KTP|KERKYX 20250828

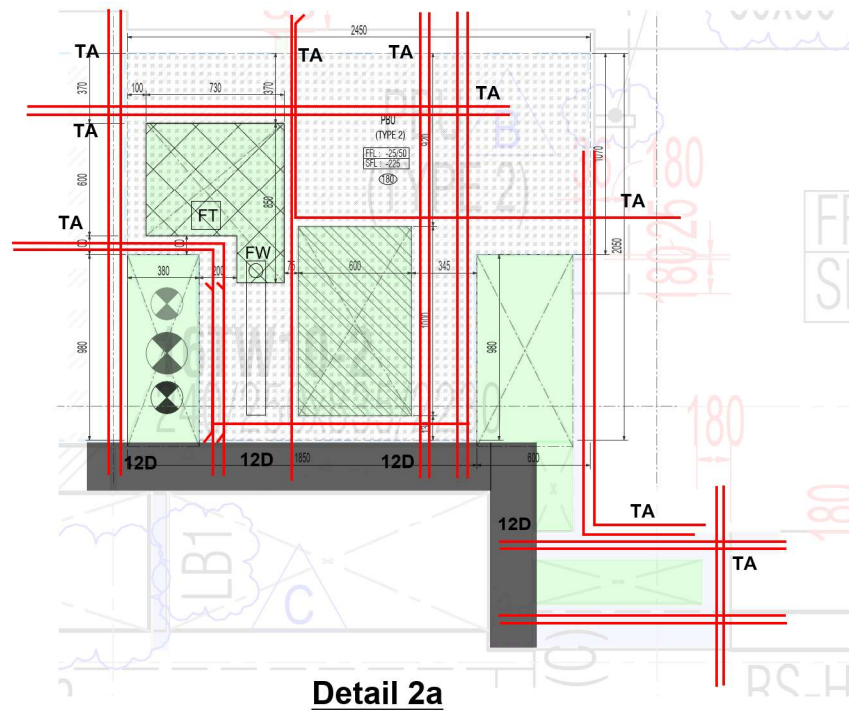

Detail 2a

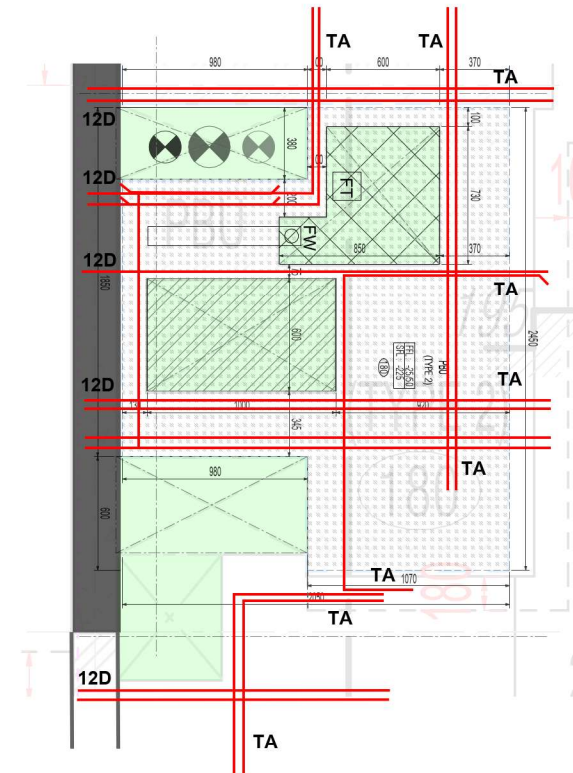


Detail 2c

FOR CONSTRUCTION

21 JAN 2026

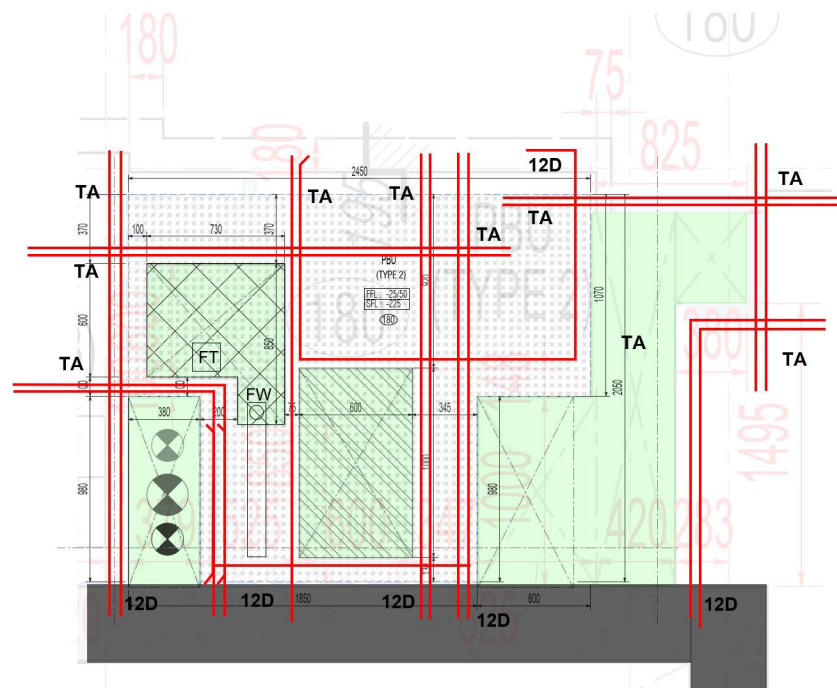TECHNICAL
WOH HUP (PRIVATE) LIMITED
MARINA VIEW RESIDENCES (MVR)



Detail 2b

KTP: No objection

KerkYX 20251223