



Cut & Bend Rebar – JOB ADVICE

工作通知 Fax:6261 9133

BBS No 钢筋加工表	<u>MVR-TT-H318</u>	Total Weight 总重量	<u>4, 151</u>
Contract 合同号码		Total Pages Attached 统计页数	1+6
Customer 承包商	<u>WOH HUP PTE LTD</u>	Gate:	
Project Title 施工地址	<u>MARINA VIEWLP 28F 1 STRAITS BIVD,SINGAPORE 018906</u>		
Description 形容	L37层 CJ4-2 墙 《149.920~153.245》		
Date Order 订单日期	24-Aug-2026	Date Required 交货日期	31-Aug-2026
Remarks 评论			
Check/Approved By 检查/审核/订货人	<u>Zhou Bing</u>	Handphone 手提电话	<u>9847 1699</u>
Site Contact Person 联络人	<u>Kumar</u>	Handphone 手提电话	<u>8133 8587</u>
Material Receiver 收货人	<u>SIVA</u>	Handphone 手提电话	<u>8426 2921</u>
Site Telephone 工地电话		Site Fax No 传真号码	
Scheduler 开料人	<u>Lu Yong Bing</u>	Handphone 手提电话	<u>8982 7022</u>
<u>***Please Allow 5 days for ??? To Process Your Order***</u>			
<u>51 Tuas South Street 5,Singapoer637644</u>			

Name	Contact numbers	Email Address
project Coodinator	Leslie LIM	8524 2927



PROJECT :		MARINA VIEWLP 28F 1 STRAITS BIVD,SINGPORE 018906						Pg. 1 / 6	
BBS No:		MVR-TT-H318					Rev.	Date : 2026/8/24	
Dwg. No.							Rev.	Prepared By:	
TITLE:		L37层 CJ4-2 墙 《149.920~153.245》						BBS NO: MVR-TT-H318	
BAR BENDING SCHEDULE									
MEMBER	BAR MARK	TYPE & SIZE	NO. OF MBRS	NO.O F EACH	TOTAL	SHAP E CODE	SHAPE	CUT OFF LENGTH	WEIGHT
					墙				
			35TW29-1 (150*1580)						
立筋	V	H 16	1	18	18	20		4230	120.23
水平	H	H 10	1	23	23	61		3460	49.02
拉勾		H 08	2	5	10	38a		300	1.19
			35TW29-2 (225*1585)						
立筋	V	H 16	1	22	22	20		4230	146.94
水平	H	H 10	1	23	23	61		3570	50.58
拉勾		H 08	2	5	10			395	1.56
			35TW31-1 (225*1055)						
立筋	V	H 16	1	12	12	20		4230	80.15
水平	H	H 10	1	23	23	61		2520	35.70
拉勾		H 08	1	5	5			395	0.78
BOX	小	H 13	1	2	2	37		1100	2.29
BOX	拉勾	H 13	1	4	4			505	2.10

REBAR SIZE		R06	H08	H10	H13	H16	H20	H25	H32	H40	TOTAL
WEIGHT			3.5	####	4.4	####					490.5 KG



PROJECT :		MARINA VIEWLP 28F 1 STRAITS BIVD,SINGAPORE 018906	Pg. 2 / 6
BBS No:		MVR-TT-H318	Rev. Date : 2026/8/24
Dwg. No.			Rev. Prepared By:
TITLE:		L37层 CJ4-2 墙 《149.920~153.245》	BBS NO: MVR-TT-H318














BAR BENDING SCHEDULE

MEMBER	BAR MARK	TYPE & SIZE	NO. OF MBRS	NO. OF EACH	TOTAL	SHAPE CODE	SHAPE	CUT OFF LENGTH	WEIGHT
			35TW31-2 (225*1055)						
立筋	V	H 16	1	12	12	20		4230	80.15
水平	H	H 10	1	23	23	61		2520	35.70
拉勾		H 08	1	5	5			395	0.78
			35TW29-3 (225/240*6930/3040)						
立筋	V	H 16	1	136	136	20		4230	908.37
水平	H1	H 10	2	23	46	38		3710	105.13
	H2	H 10	2	23	46	38a		1715	48.60
	H3	H 10	2	23	46	20		6700	189.85
拉勾1		H 08	9	5	45			395	7.02
拉勾2		H 08	4	5	20			410	3.24
BOX	小	H 13	2	2	4	37		1100	4.58
BOX	拉勾	H 13	2	4	8			505	4.21
			35TW30 (285*1370)						
立筋	V	H 16	1	22	22	20		4230	146.94
水平	H	H 10	1	23	23	61		3270	46.33

REBAR SIZE		R06	H08	H10	H13	H16	H20	H25	H32	H40	TOTAL
WEIGHT			11.0	####	8.8	####					1580.9 KG



PROJECT :	MARINA VIEWLP 28F 1 STRAITS BIVD,SINGAPORE 018906			Pg. 3 / 6
BBS No:	MVR-TT-H318	Rev.	Date : 2026/8/24	
Dwg. No.		Rev.	Prepared By:	
TITLE:	L37层 CJ4-2 墙 《149.920~153.245》			BBS NO: MVR-TT-H318

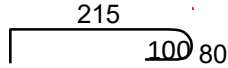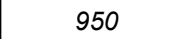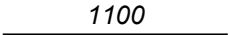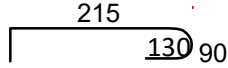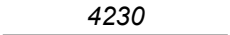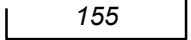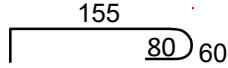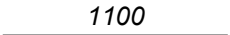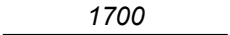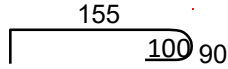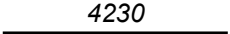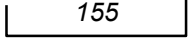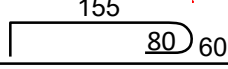BAR BENDING SCHEDULE									
MEMBER	BAR MARK	TYPE & SIZE	NO. OF MBRS	NO. OF EACH	TOTAL	SHAPE CODE	SHAPE	CUT OFF LENGTH	WEIGHT
拉勾		H 10	2	5	10		120  80	515	3.17
BOX	小	H 13	1	2	2	37	150  950	1100	2.29
BOX	大	H 13	1	2	2	20	 1100	1100	2.29
BOX	拉勾	H 13	2	4	8		160  90	595	4.96
			35TW31-3 (225*3200)						
立筋	V	H 16	1	44	44	20	 4230	4230	293.88
水平	H	H 10	2	23	46	38	570  3130	3855	109.24
拉勾		H 08	4	5	20		100  60	395	3.12
BOX	大	H 13	8	2	16	20	 1100	1100	18.34
BOX	超大	H 13	1	2	2	20	 1700	1700	3.54
BOX	拉勾	H 13	9	4	36		160  90	505	18.94
			35TW31-4 (225*2825)						
立筋	V	H 16	1	46	46	20	 4230	4230	307.24
水平	H	H 10	2	23	46	38	570  2750	3475	98.47
拉勾		H 08	4	5	20		100  60	395	3.12

REBAR SIZE		R06	H08	H10	H13	H16	H20	H25	H32	H40	TOTAL
WEIGHT			6.2	####	50.4	####					868.6 KG



PROJECT :		MARINA VIEWLP 28F 1 STRAITS BIVD,SINGAPORE 018906						Pg. 4 / 6	
BBS No:		MVR-TT-H318					Rev.	Date : 2026/8/24	
Dwg. No.							Rev.	Prepared By:	
TITLE:		L37层 CJ4-2 墙 《149.920~153.245》						BBS NO: MVR-TT-H318	
BAR BENDING SCHEDULE									
MEMBER	BAR MARK	TYPE & SIZE	NO. OF MBRS	NO. OF EACH	TOTAL	SHAPE CODE	SHAPE	CUT OFF LENGTH	WEIGHT
BOX	小	H 13	2	2	4	37	150 950	1100	4.58
BOX	大	H 13	2	2	4	20	1100	1100	4.58
BOX	拉勾	H 13	4	4	16		160 155 100 90	505	8.42
			35TW32 (285*1370)						
立筋	V	H 16	1	18	18	20	4230	4230	120.23
水平	H	H 10	1	23	23	61	215 1300	3270	46.33
拉勾		H 10	1	5	5		120 215 100 80	515	1.59
BOX	小	H 13	1	2	2	37	150 950	1100	2.29
BOX	大	H 13	1	2	2	20	1100	1100	2.29
BOX	拉勾	H 13	2	4	8		160 215 130 90	595	4.96
			35TW33-1 (225*2100)						
立筋	V	H 16	1	22	22	20	4230	4230	146.94
水平	H	H 10	1	23	23	38a	2060 155 2060	4275	60.57
拉勾		H 08	3	5	15		100 155 80 60	395	2.34

REBAR SIZE		R06	H8	H10	H13	H16	H20	H25	H32	H40	TOTAL
WEIGHT				####	27.1	####					402.8 KG



PROJECT :	MARINA VIEWLP 28F 1 STRAITS BIVD,SINGAPORE 018906			Pg. 5 / 6
BBS No:	MVR-TT-H318	Rev.	Date : 2026/8/24	
Dwg. No.		Rev.	Prepared By:	
TITLE:	L37层 CJ4-2 墙 《149.920~153.245》			BBS NO: MVR-TT-H318

BAR BENDING SCHEDULE									
MEMBER	BAR MARK	TYPE & SIZE	NO. OF MBRS	NO. OF EACH	TOTAL	SHAPE CODE	SHAPE	CUT OFF LENGTH	WEIGHT
			35TW33-2 (225*3600)						
立筋	V	H 16	1	38	38	20		4230	253.81
水平	H	H 10	2	23	46	38		4255	120.57
拉勾		H 08	4	5	20			395	3.12
BOX	小	H 13	4	2	8	37		1100	9.17
BOX	拉勾	H 13	4	4	16			505	8.42
			35TW34 (225*1455)						
立筋	V	H 16	1	16	16	20		4230	106.87
水平	H	H 10	1	23	23	61		3320	47.04
拉勾		H 08	1	5	5			395	0.78
BOX	小	H 13	1	2	2	37		1100	2.29
BOX	拉勾	H 13	1	4	4			505	2.10
			35TW35 (240*2170)						
立筋	V	H 16	1	24	24	20		4230	160.30
水平	H	H 10	1	23	23	61		4780	67.72
拉勾		H 08	3	5	15			410	2.43

REBAR SIZE		R06	H08	H10	H13	H16	H20	H25	H32	H40	TOTAL
WEIGHT			6.3	####	22.0	####					784.6 KG




REBAR SIZE		R06	H08	H10	H13	H16	H20	H25	H32	H40	TOTAL
WEIGHT					23.8						23.8 KG

MVR PJW CO WH CST ZZ ZZ SK W 2659A Typical Resi Wall Recess Trimmer Bar Optimisation VE Rev A

Q1P: Previous Approved Sketch

*2H20 trimmer bars or equivalent size.

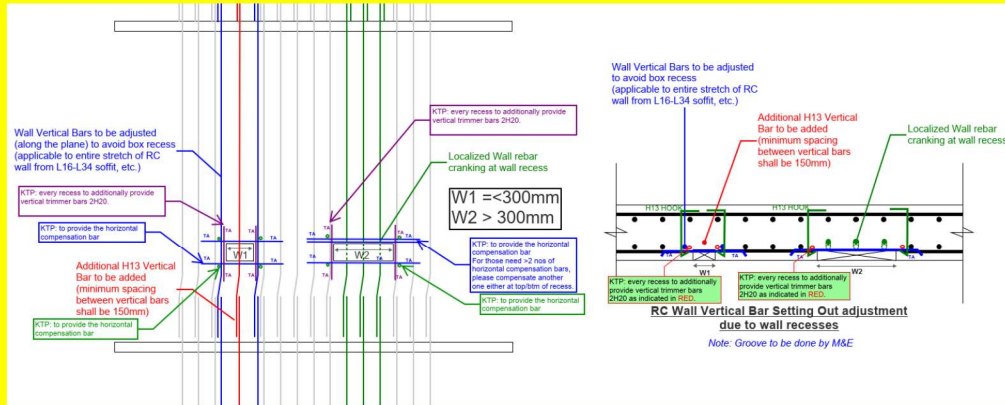


FOR CONSTRUCTION

25 MAR 2026

TECHNICAL
WOH HUP (PRIVATE) LIMITED
MARINA VIEW RESIDENCES (MVR)

UNLESS OTHERWISE STATED IN CBP ABOVE;

THE REST OF WALLS FROM L27- **UNDERSIDE OF L33, L36 to ROOF** are allowed to reduce the vertical trimmer bars to be **2H13** only.

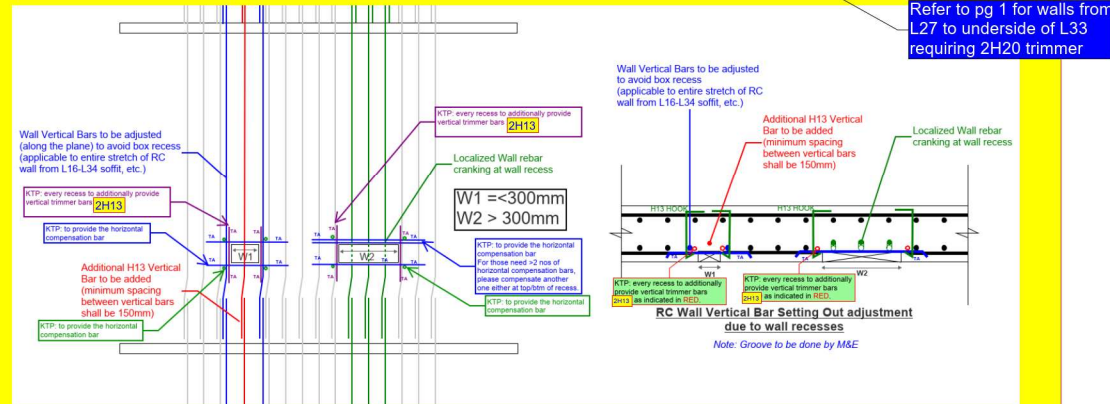



KTP 20260324:

FOR L33 TO UNDERSIDE L36, kindly provide the trimmer bar as per previous approved sketch, which is 2H20 or equivalent.




注意：底部150/360mm高Recess
除非旁边画有详图。其余所有第一道
水平铁从楼层面向上50mm开始施工。

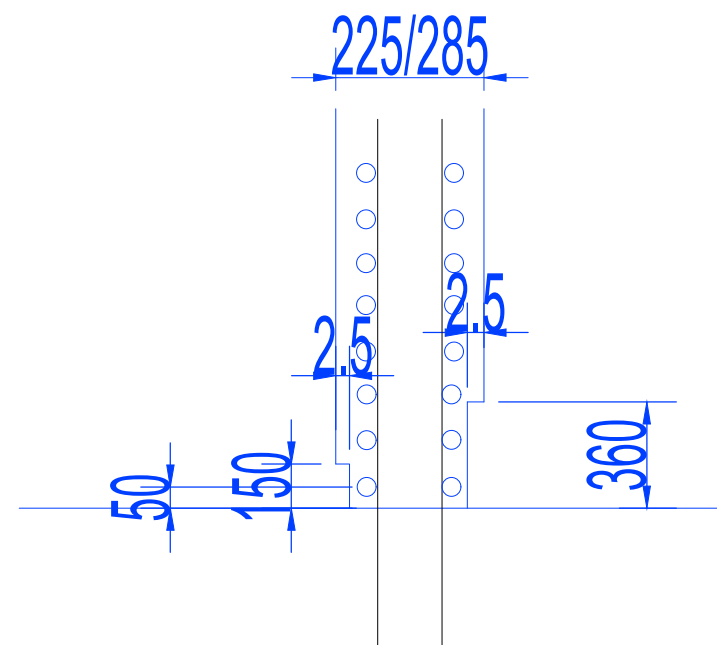

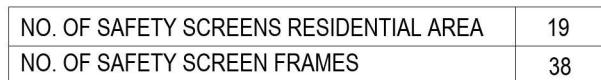


NUFORM PERIMETER SAFETY SCREEN SYSTEM
RESIDENTIAL AREA - TYPICAL 17TH~48TH STOREY PLAN
RESIDENTIAL AREA

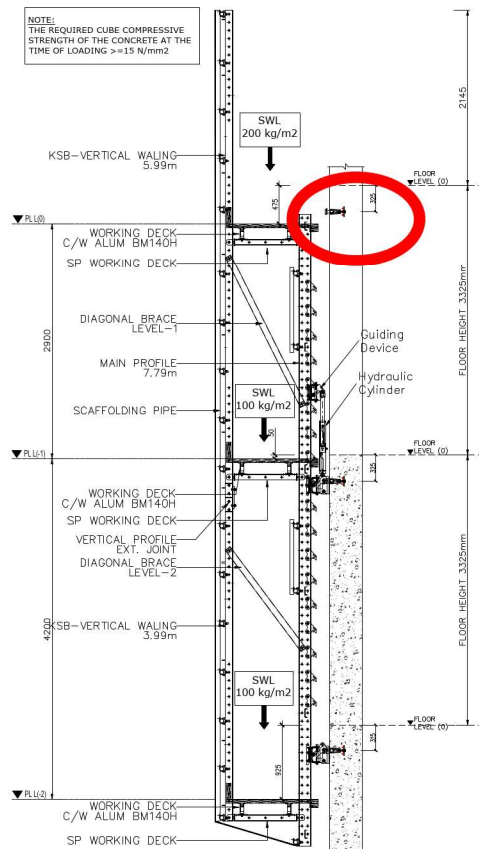


NUFORM CLIMBING SCAFFOLD SYSTEM
TYPICAL SECTION DETAIL FOR
WALL 240mm

SS-R-02 SS-R-03 SS-R-14 SS-R-17

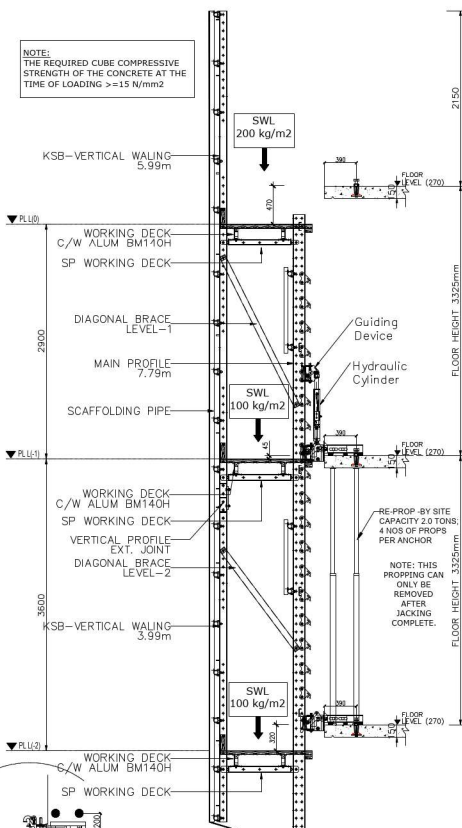


NUFORM PERIMETER SCAFFOLD SYSTEM
TYPICAL SECTION DETAIL FOR
CAST IN-SITU RC LEDGE 150mm

SS-R-01

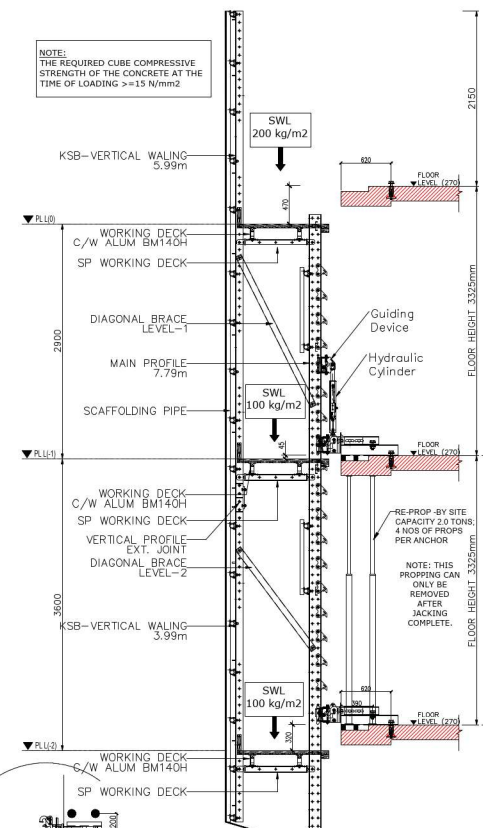






NUFORM PERIMETER SCAFFOLD SYSTEM
TYPICAL SECTION DETAIL FOR
CAST IN-SITU BALCONY 180mm

SS-R-11 SS-R-18

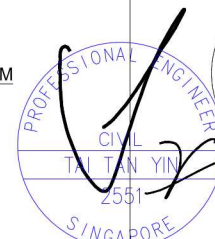


WORKING DRAWING
08 SEPTEMBER 2025


MAIN CONTRACTOR : WOH HUP (PRIVATE) LIMITED BUILDING WITH INTEGRITY 217 Upper Bukit Timah Road #01-01 Woh Hup Building Singapore 588185 Tel: 63895585 Fax: 62723322	PROJECT : PROPOSED NEW ERECTION OF 81 STOREY MIXED USE DEVELOPMENT COMPRISING 8 STOREY HOTEL AND GARDENS POOLUM, 8 STOREY HOTEL (260 ROOMS), 3037 STOREY RESIDENTIAL FLATS (863 UNITS) AND 2 BASEMENTS ON LOT 2048K AND 2048M1 TS 30 AND SUBTERRANEAN SPACE LOT 8802C TS 30 AT MARINA VIEW (DOWNTOWN CORNER PLANNING AREA)	DRAWING : SECTION DETAILS FOR NUFORM PERIMETER SAFETY SCAFFOLD FOR TYPICAL RESIDENTIAL STOREY LAYOUT PLAN LEVEL 17TH--48TH
SUB CONTRACTOR : NUFORM SYSTEM Nuform System Asia Pte Ltd	SUPPLIER : NUFORM SYSTEM Nuform System Asia Pte Ltd	DRAWN BY : AA SCALE : 1:65 PROJECT NO : NU-22-015 CHECKED BY : EMMAN DATE : 08 SEPT 2025 REV :

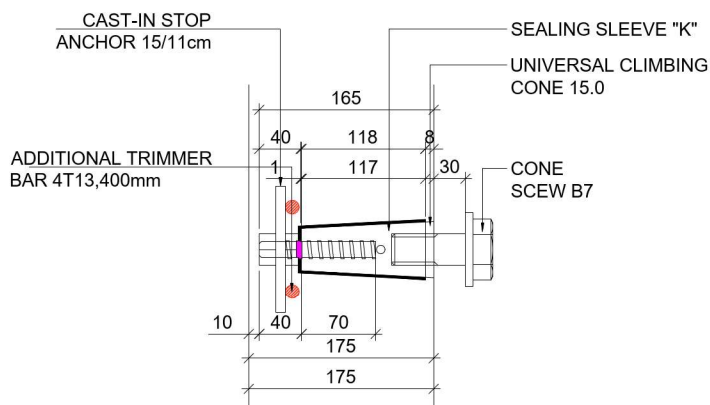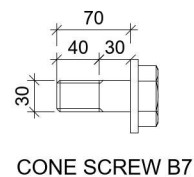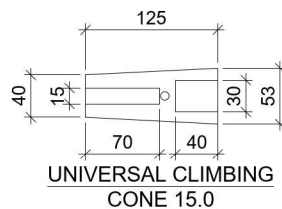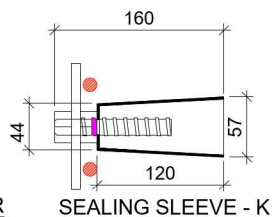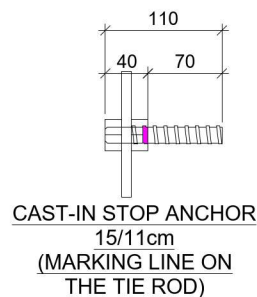

SET UP FOR UNIVERSAL CLIMBING CONE
15.0 WITH STOP ANCHOR 15/11 cm
(WALL THICKNESS >=175~200mm)


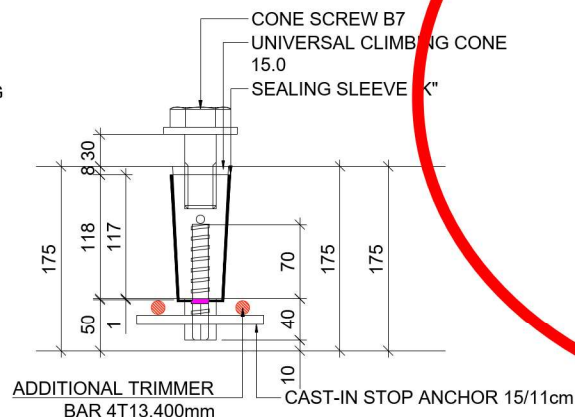



SET UP FOR UNIVERSAL CLIMBING CONE
15.0 WITH STOP ANCHOR 15/11 cm
(SLAB THICKNESS >= 175~200mm)

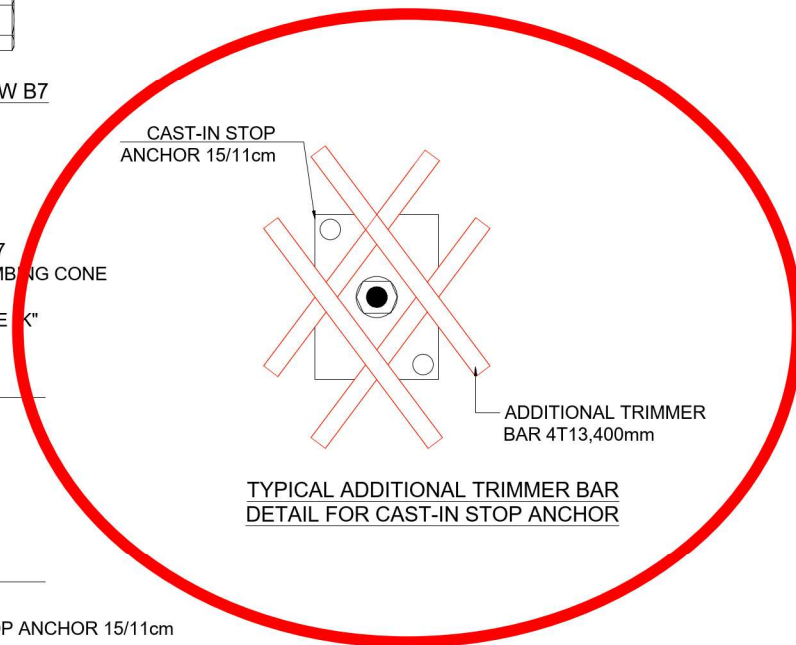


WORKING DRAWING
08 SEPTEMBER 2025

MAIN CONTRACTOR :  WOH HUP (PRIVATE) LIMITED BUILDING WITH INTEGRITY 217 Upper Selegie Road #01-01/02/03/2317/

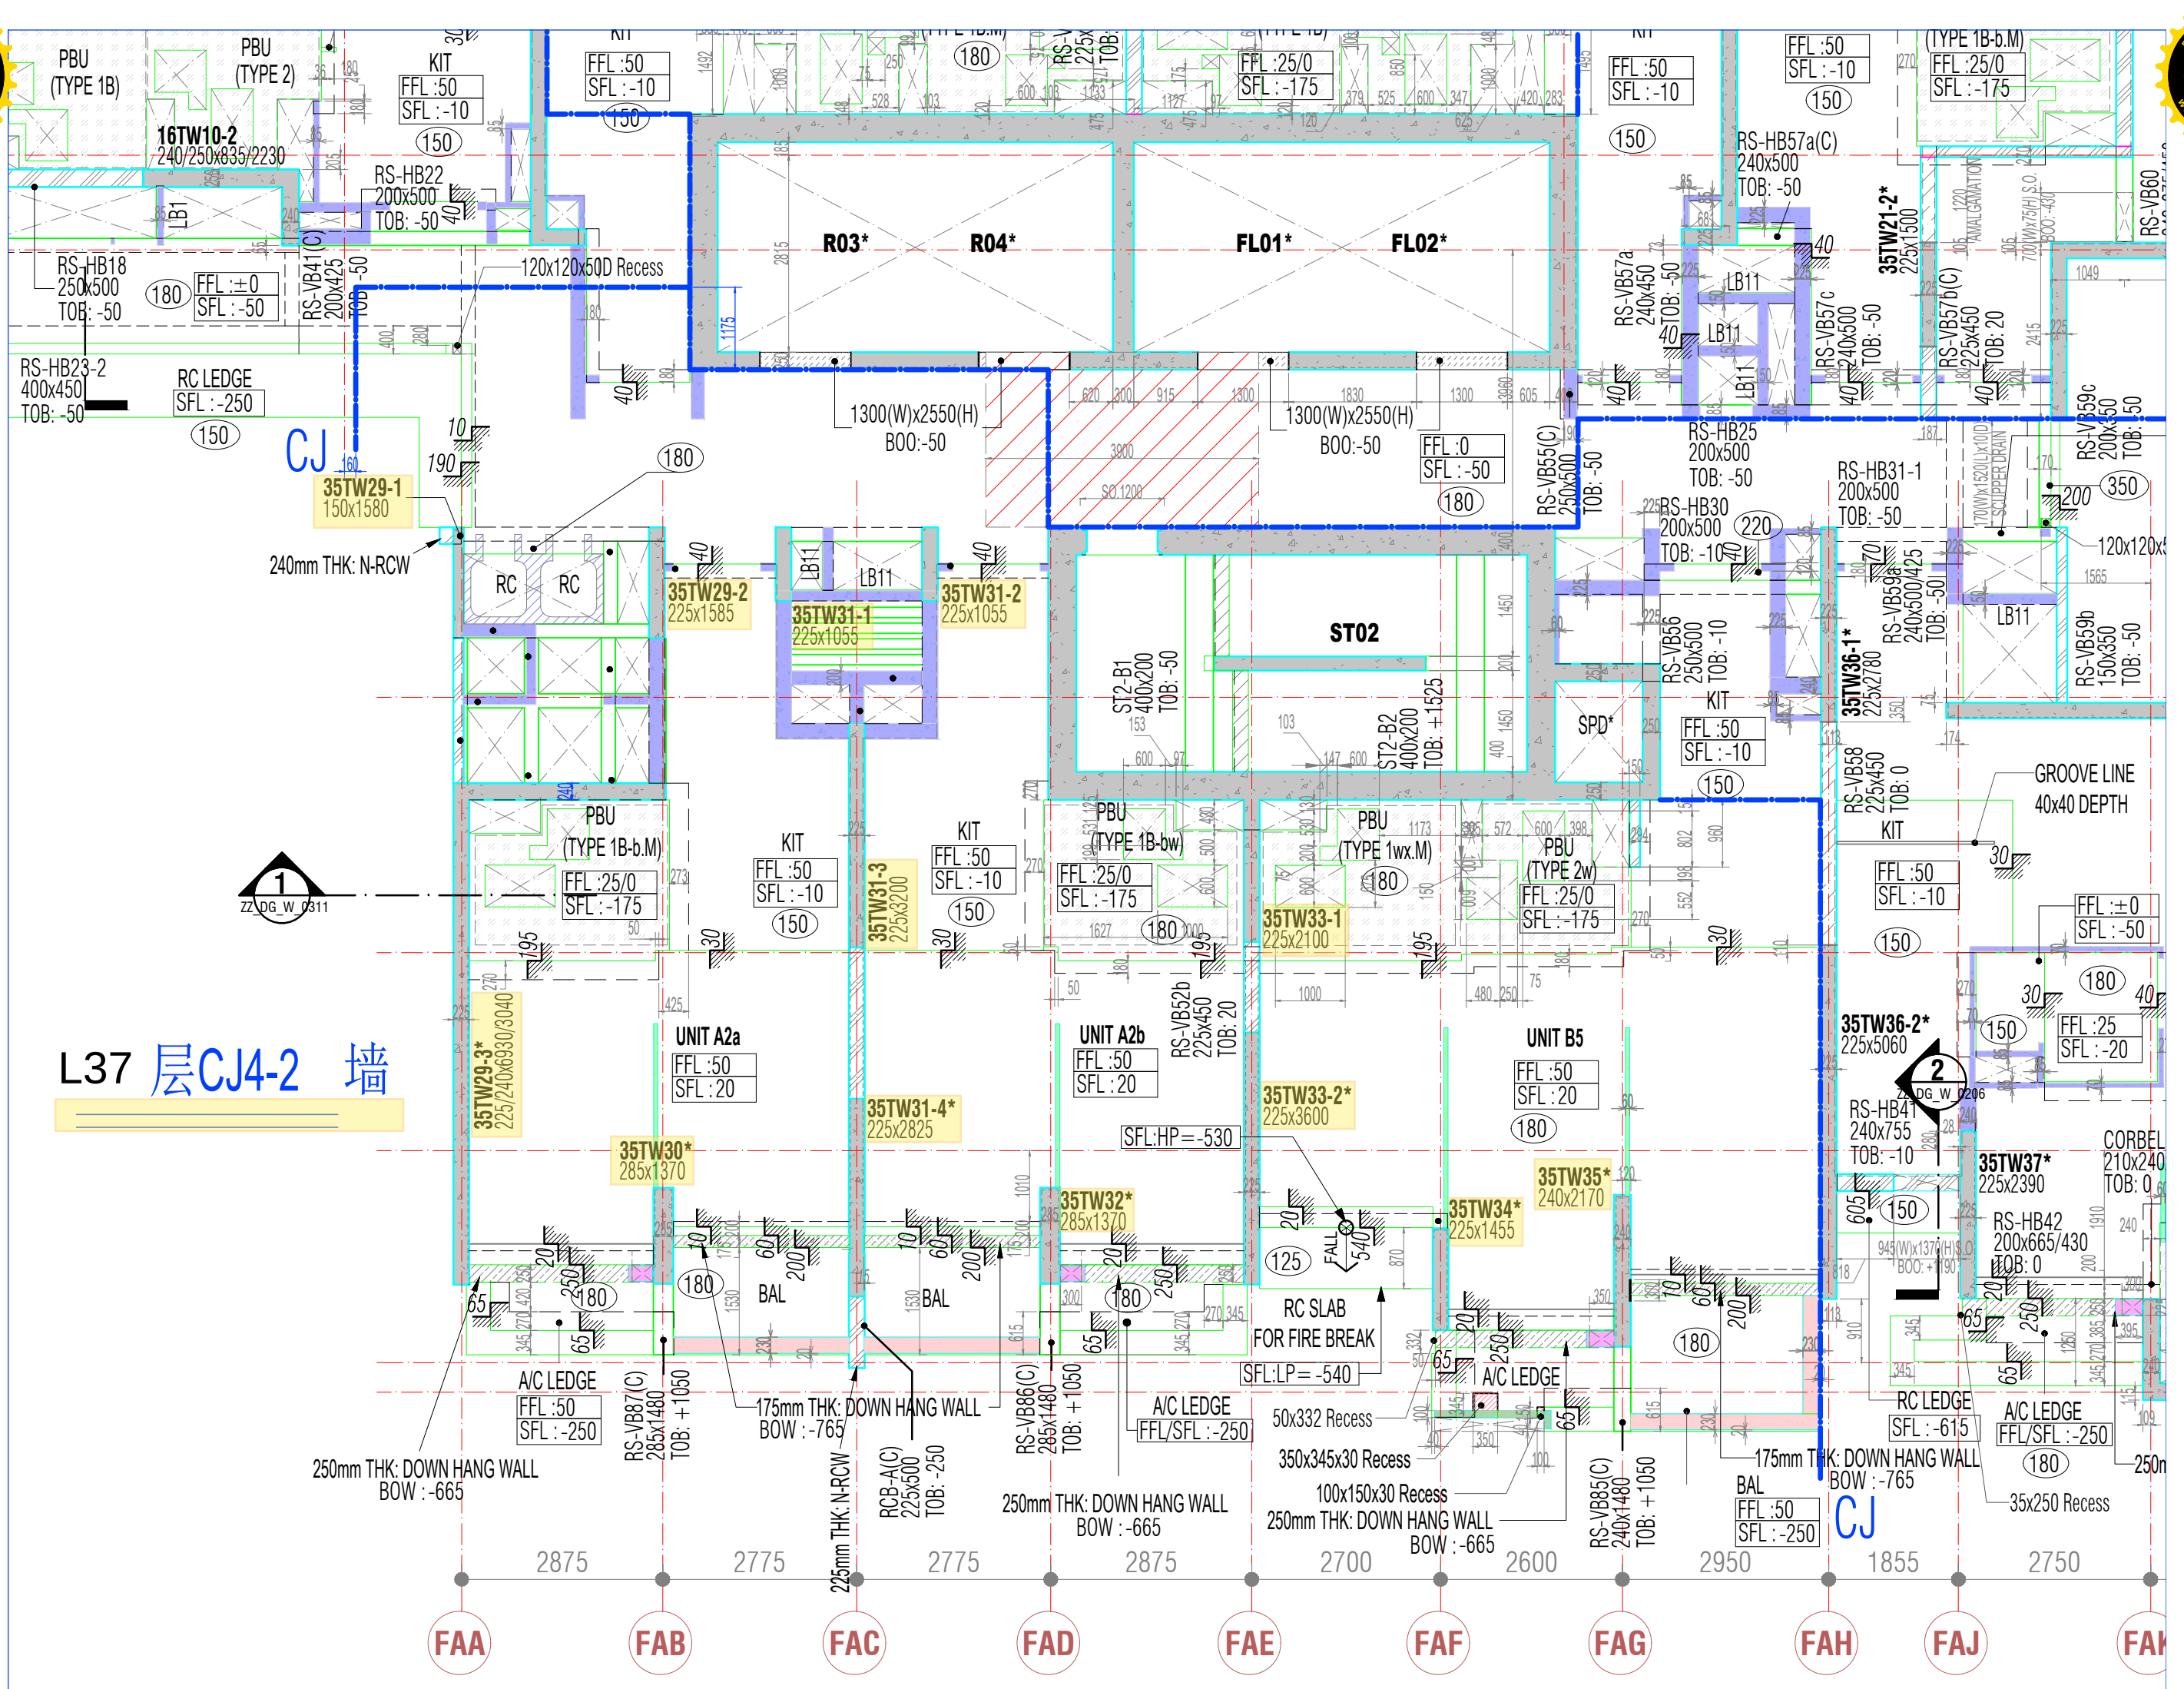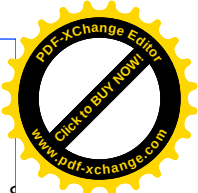


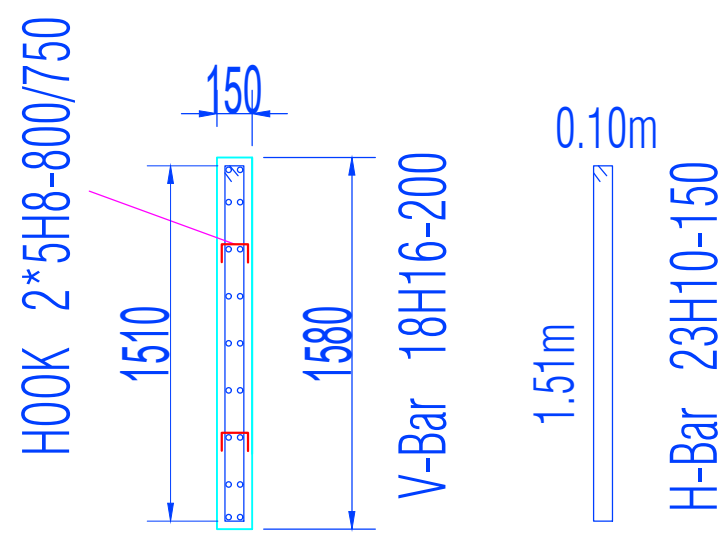


35TW29-1
150x1580
TL = 52D

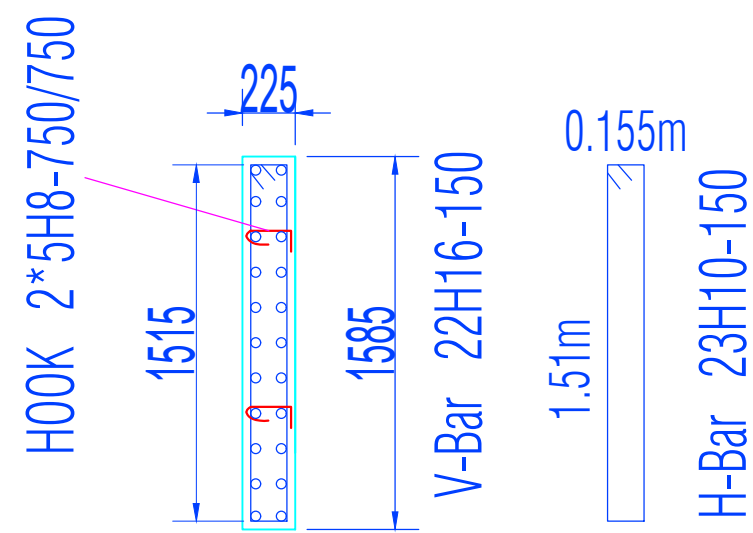




35TW29-2
225x1585
TL = 52D

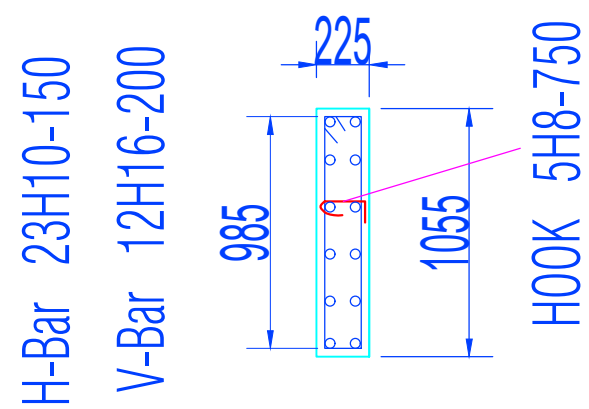


35TW31-1
225x1055
TL = 52D

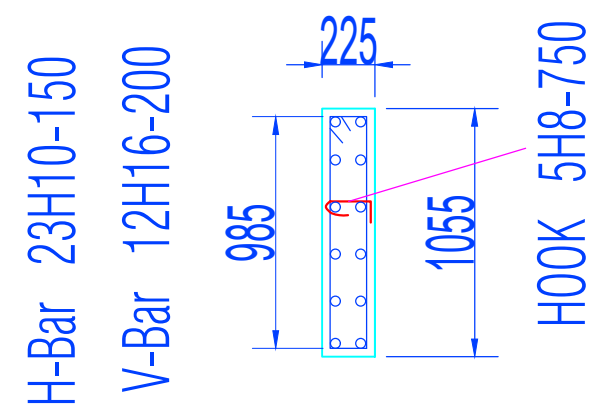


35TW31-2
225x1055
TL = 52D

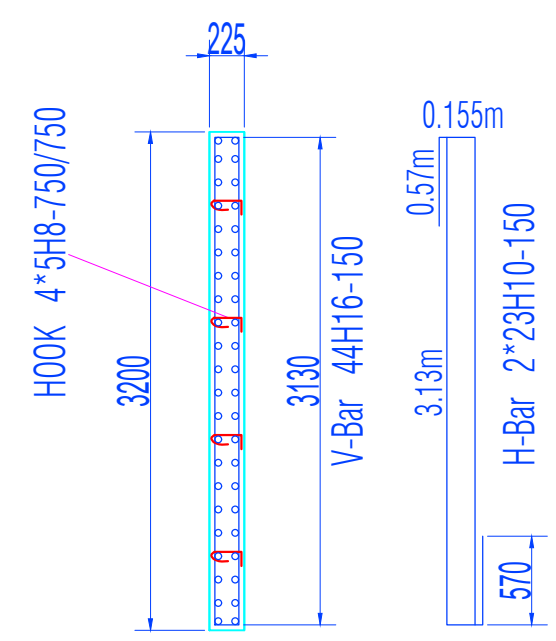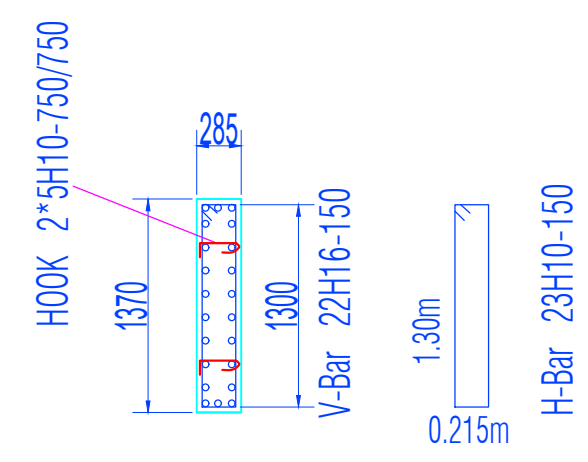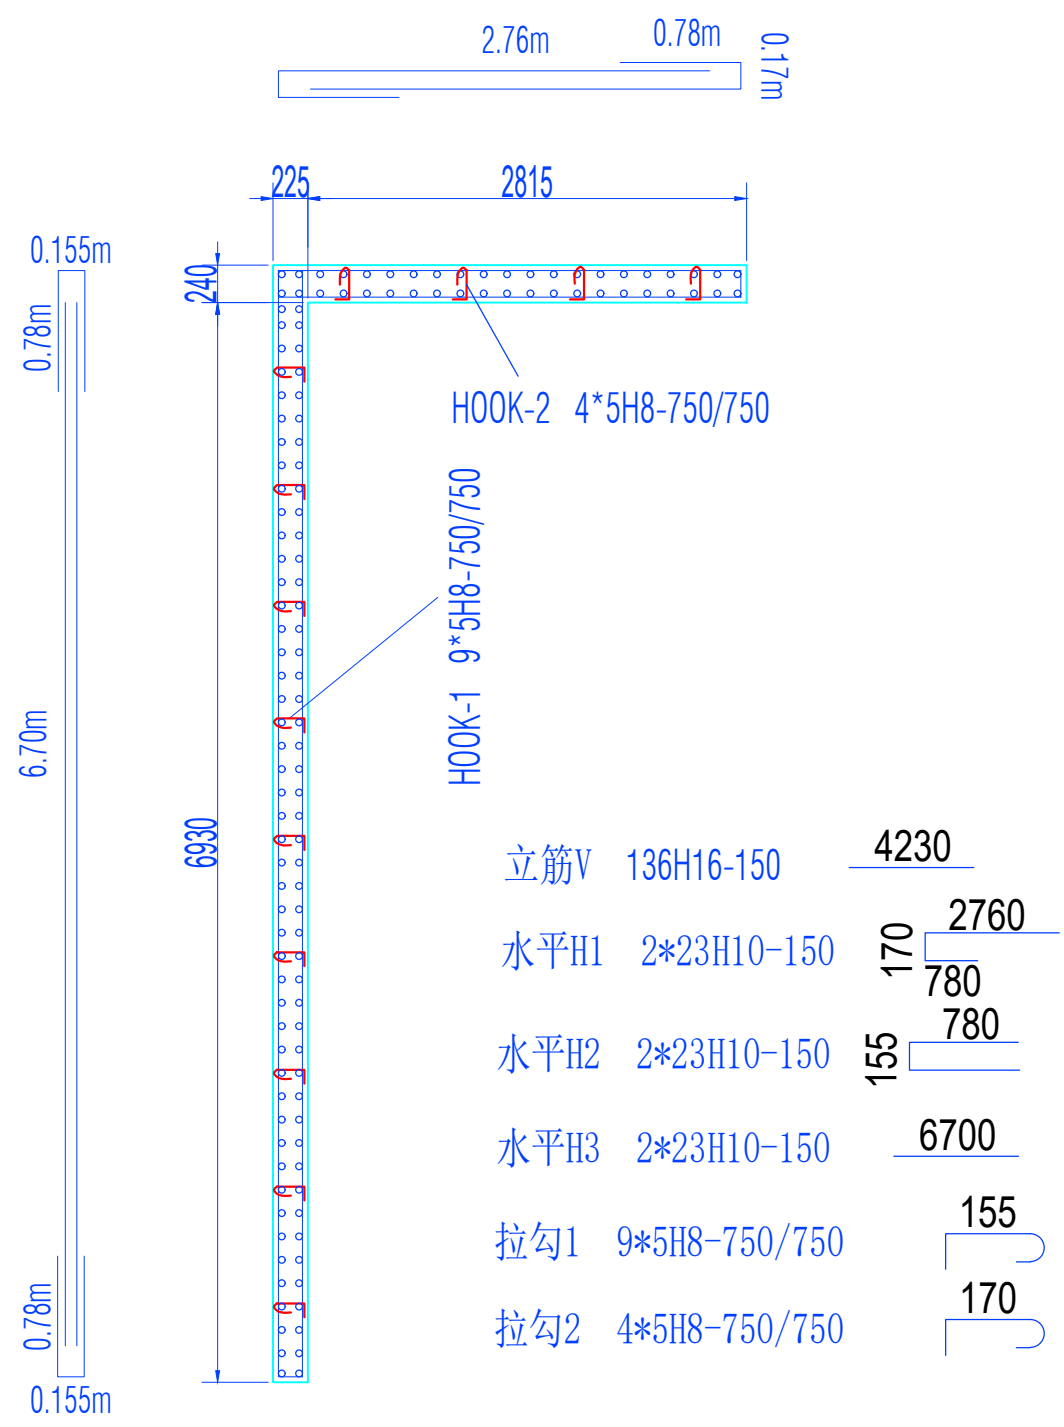


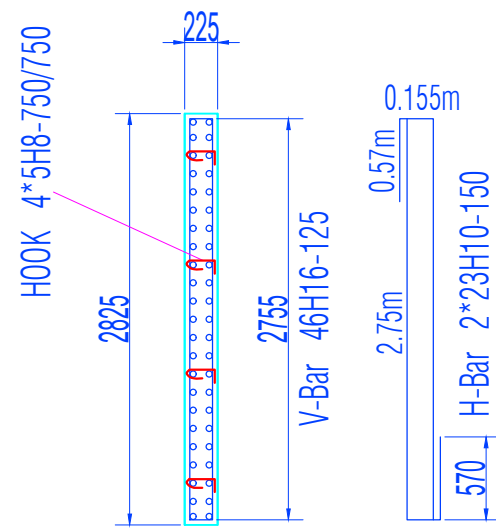


35TW31-4*
225x2825
TL = 52D

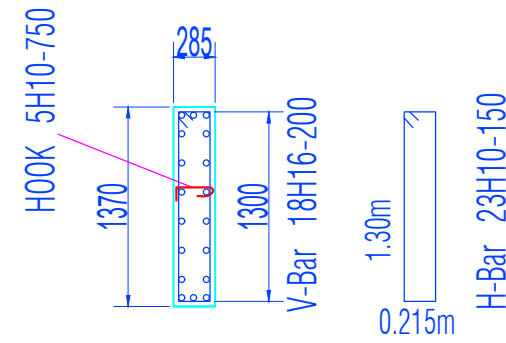


35TW32*
285x1370
TL = 52D

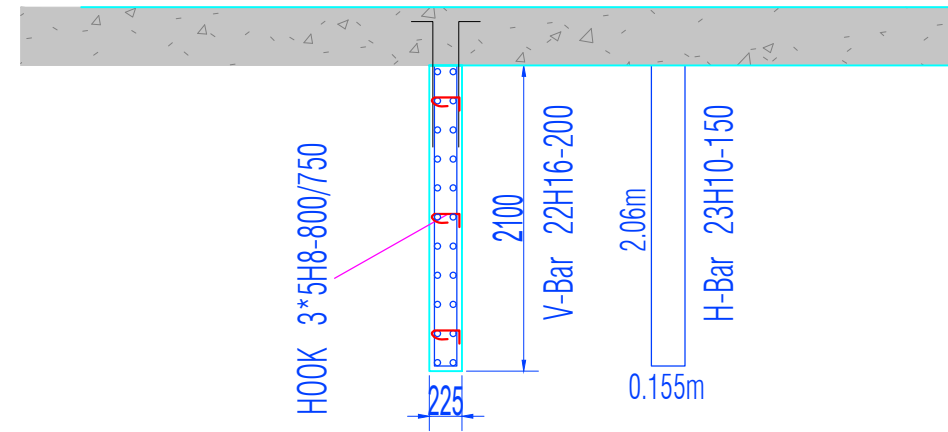


35TW33-1
225x2100
TL = 52D

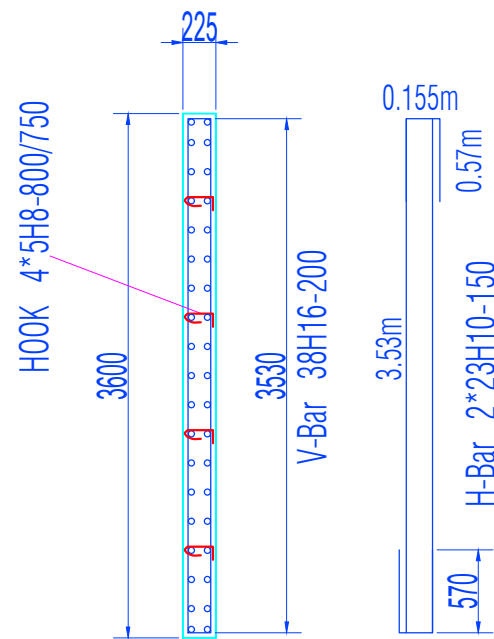


35TW33-2*
225x3600
TL = 52D

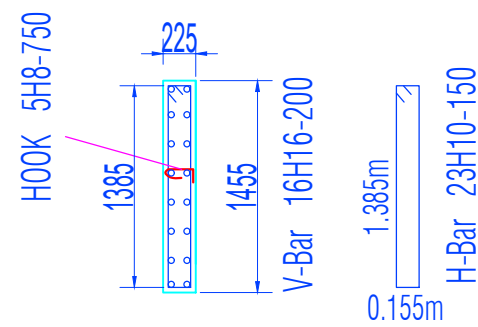

35TW34*
225x1455
TL = 52D

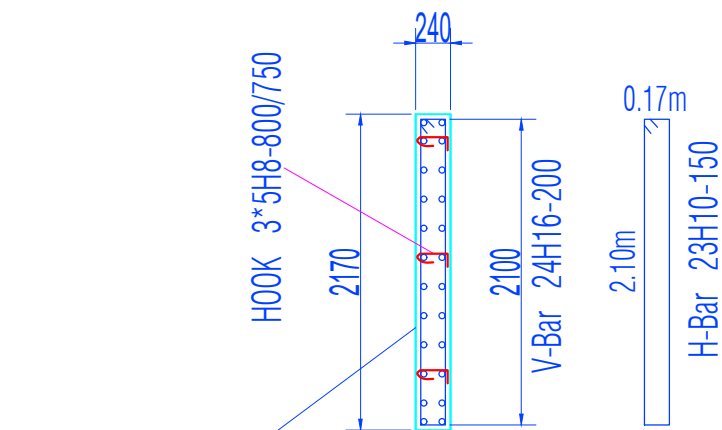

注意：底部150mm高有Recess
Recess位置水平铁向上绑

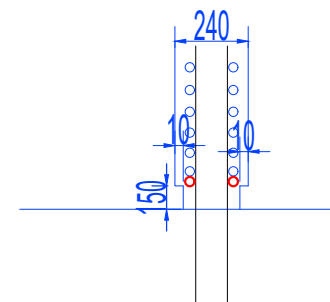

35TW35*
240x2170
TL = 52D



注意: 36~Roof 全部采用此方法施工

FB

FA


Roof
37



37

18TH STOREY SHD79200
SHD : 79200

36

17TH STOREY SHD75875
SHD : 75875

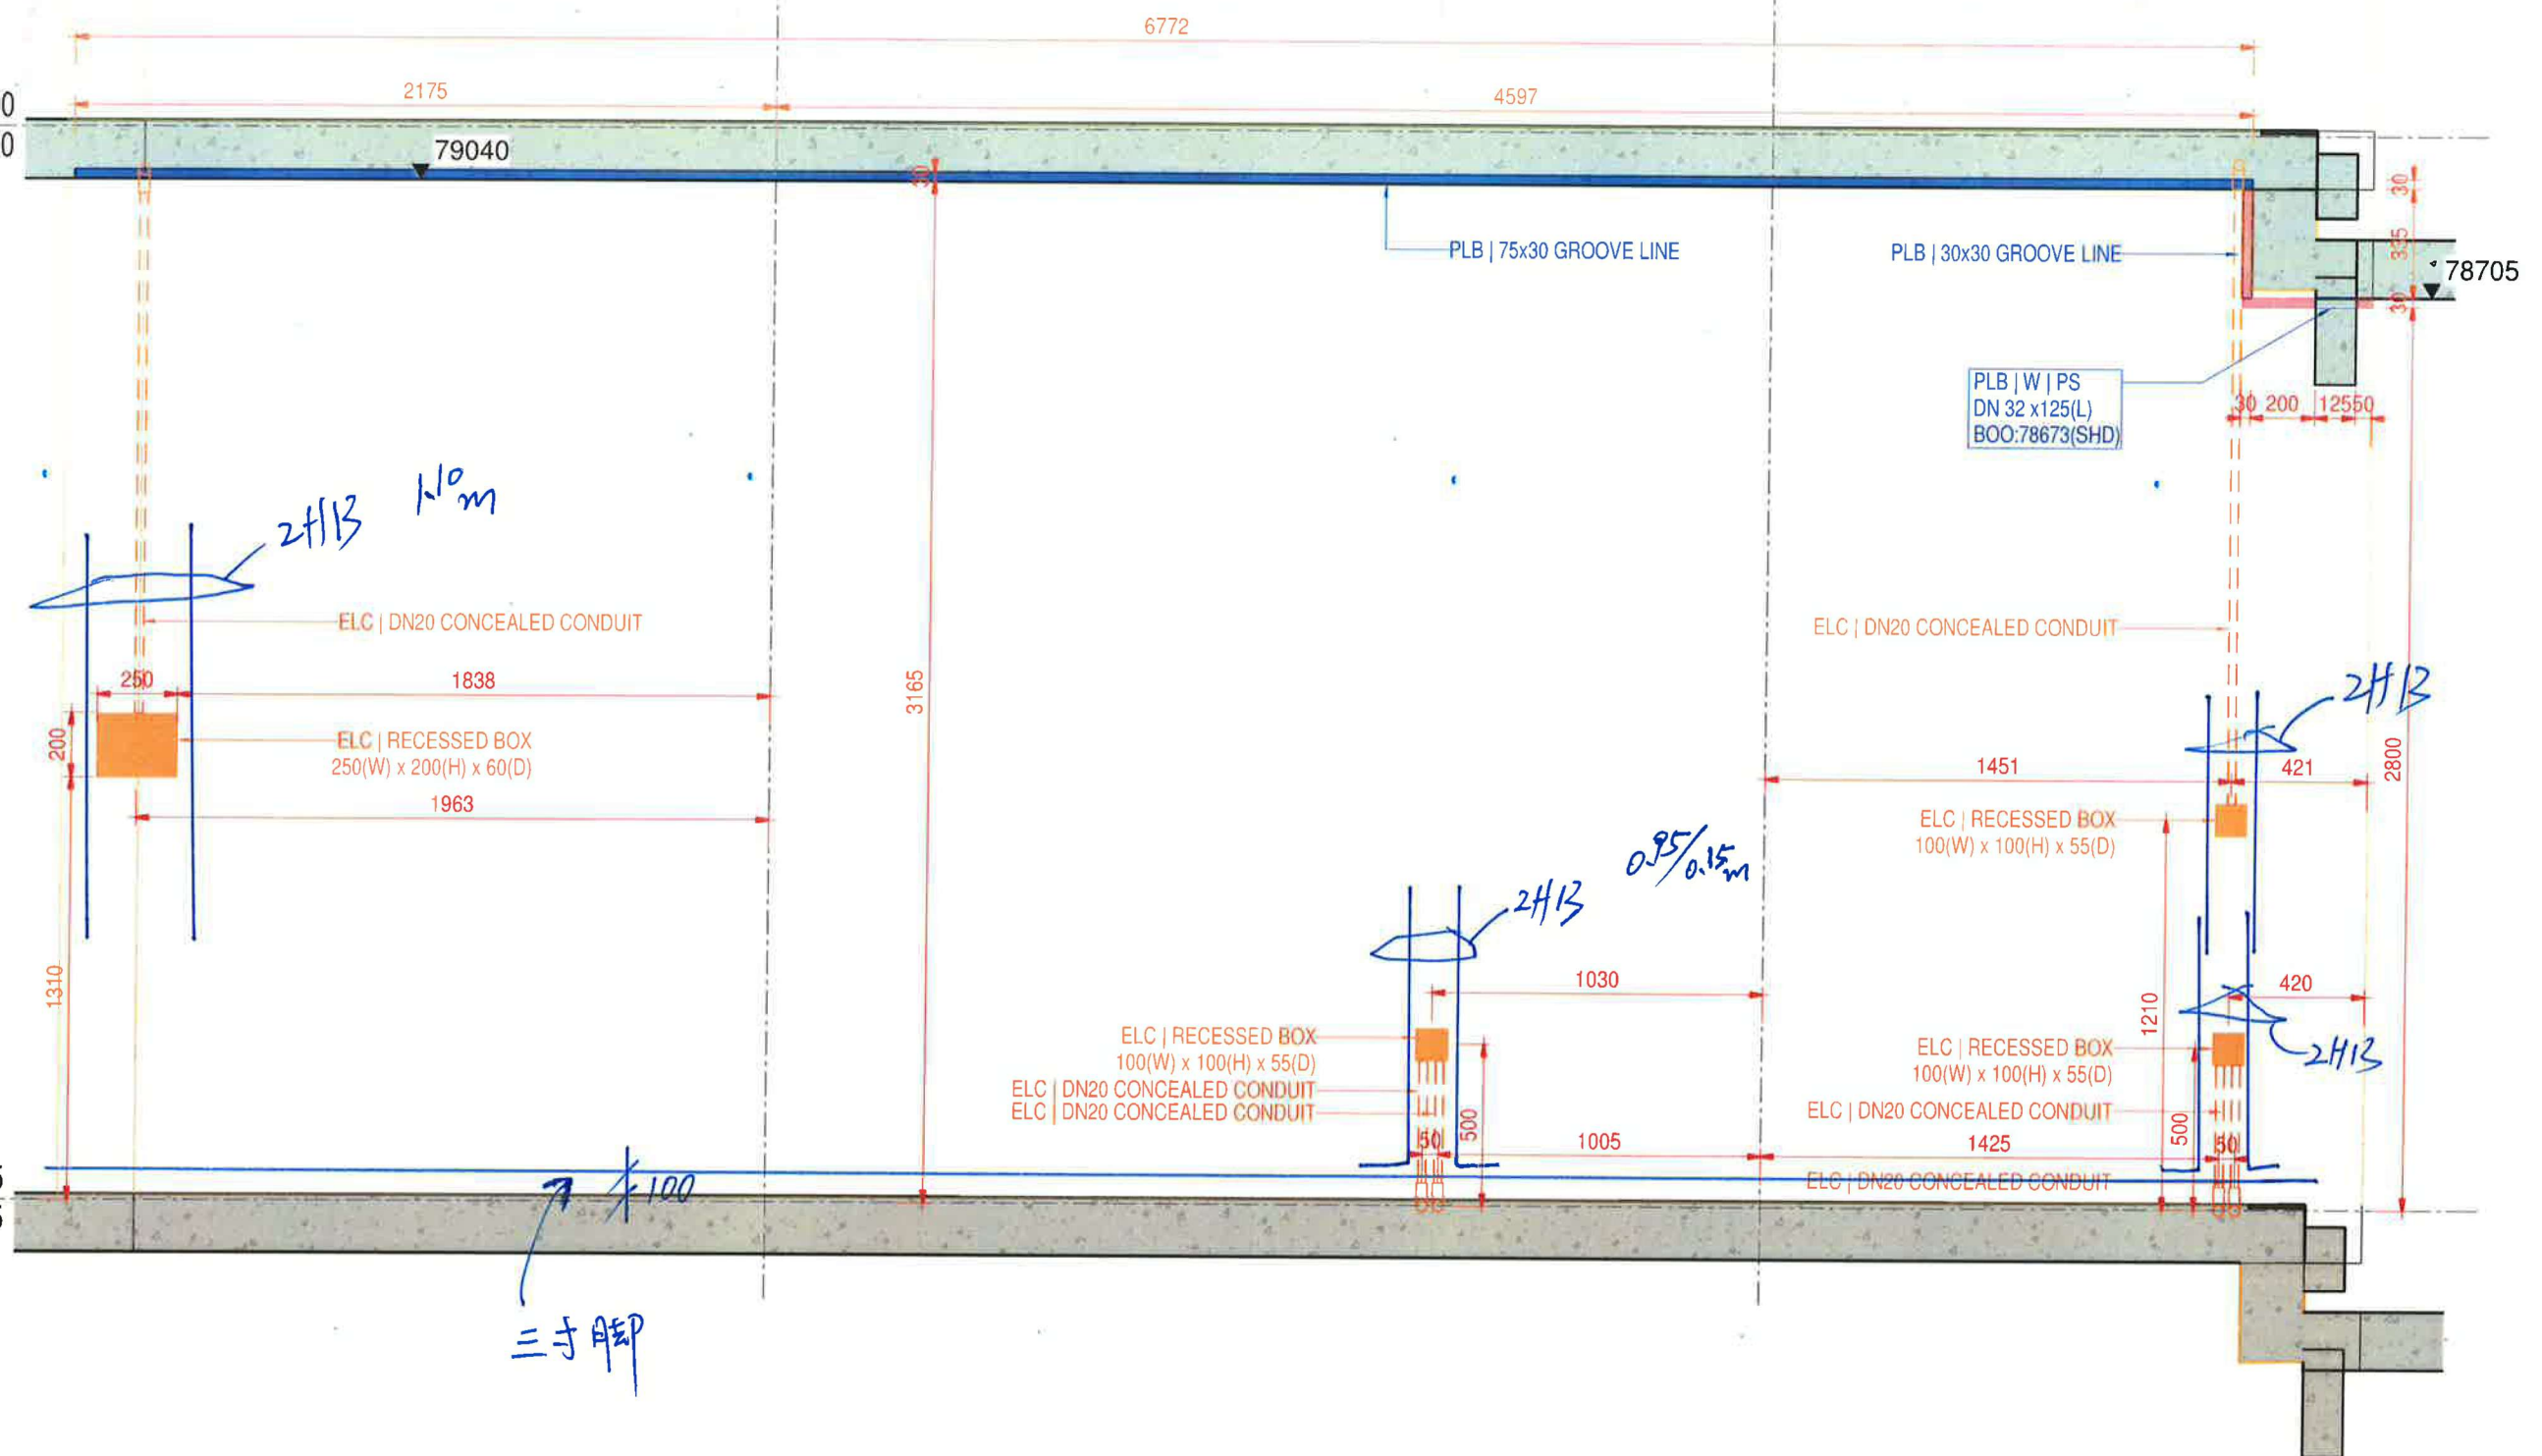

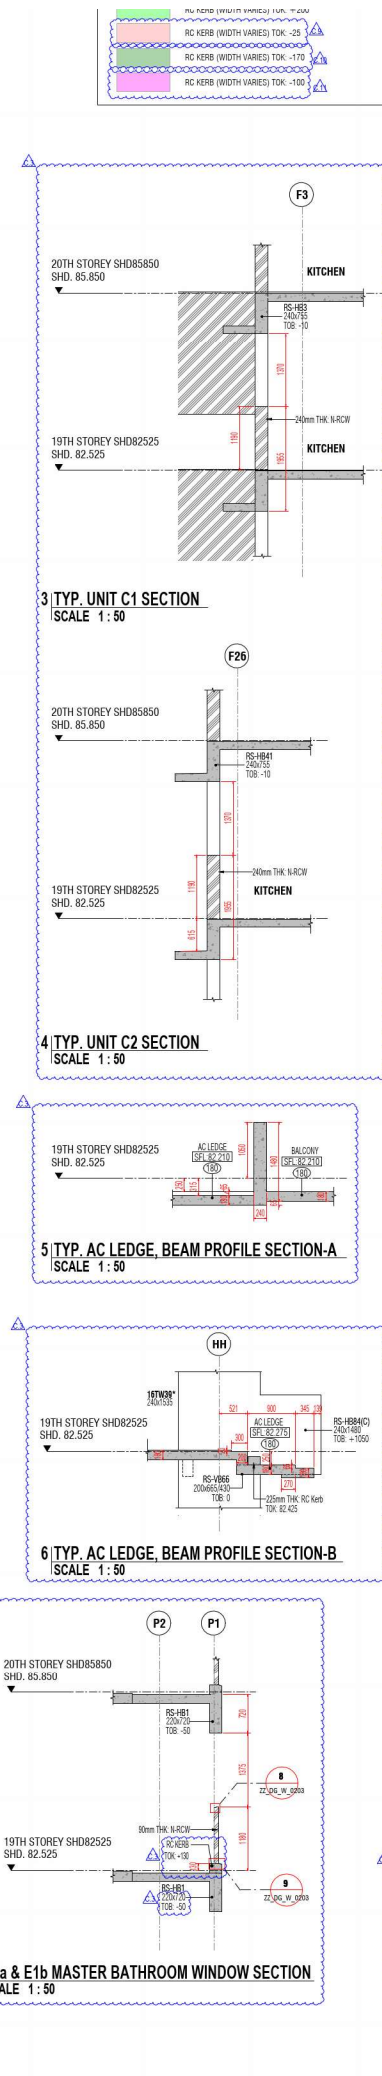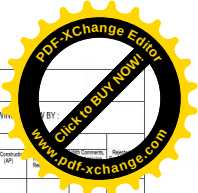

USL - UPPER SLAB LEVEL
 SSL - BELOW SLAB LEVEL
 RSL - BELOW SLAB LEVEL
 T3B - TOP OF BEAM
 BOB - BOTTOM OF BEAM
 T1B - TOP OF WALL
 BOB - BOTTOM OF OPENING
 BOB - BOTTOM OF WALL
 USL - UPSTEAM BEAM
 TOC - TOP OF COLUMN
 TOCB - TOP OF CAPPING BEAM
 SL - STRUCTURAL INVERT LEVEL
 MCL - MASS CONCRETE LEVEL
 TOPC - TOP OF FLE CAP
 TOP - TOP OF PLUMB
 TO - TEMPORARY OPENING
 PH - PASSENGER-HOST

DATE RECEIVED : _____

SHOP DRAWING BY _____

(To Consultant) (By Contractor) (By Engineer)
 (By Architect) (By Structural Engineer) (By MEP Consultant)

☐ ARCHITECT
 Architects Pte Ltd

☐ CIVIL & STRUCTURAL ENGINEER
 KSP Consultants Pte Ltd

☐ MEP CONSULTANT
 J2 Engineer Pte Ltd (Pte Ltd)

☐ INTERIOR DESIGN CONSULTANT

☐ FACADE CONSULTANT
 B&B-H&C Consulting Pte Ltd

☐ LANDSCAPE ARCHITECT
 G&S Design International Pte Ltd

Our comments and corrections made on this shop drawing do not relieve the Contractor (Sub-contractor) of its contractual responsibilities.
 We do not warrant any drawings or specifications. The Contractor is responsible for all contractors of dimensions and details in this drawing and for the full coordination of all aspect of the work.

GENERAL NOTES :

- ALL DIMENSIONS ARE TO BE IN 'mm' UNLESS OTHERWISE STATED.
- ALL DIMENSIONS ARE SUBJECT TO SITE VERIFICATION.
- DO NOT SCALE ON DRAWINGS.
- ANY DISCREPANCY MUST BE REPORTED TO MAIN CONTRACTOR IMMEDIATELY.
- ALL DRAWINGS MUST BE USED IN CONJUNCTION WITH M&E AND STRUCTURAL DRAWINGS.

REFERENCED DRAWING NO. :

- ARCHITECTURAL REFERENCE DWG:
- STRUCTURAL REFERENCE DWG
- M&E REFERENCE DWG
- OTHERS

REV	DATE	DESCRIPTION	BY	CHECKED
C	17/11/25	BASED ON REVISION B	KG	JCCY
REV	DATE	DESCRIPTION	BY	CHECKED

KEY PLAN:

DEVELOPER/LAND OWNER:

Boulevard Development Pte Ltd
Boulevard Marina Bay Pte Ltd

31 Beach Road #04-11,
 South Beach Road, Singapore 189767
 Tel: 65-4338-4111

ARCHITECT:

architects61
 architecture planning

Architects 61 pte ltd
 100 Beach Road # 04 - 01
 Tel: 65-4377-8777 Fax: 65-4377-8438 Email: info@architects61.com www.architects61.com

410 mgc no. 192018-0006
 gateway west singapore 189720
 www.gwsg.com.sg

CIVIL & STRUCTURAL ENGINEER:

threesixty
 Threesixty Cost Management Pte Ltd
 311 Orchard Road
 #07-31 Sutra Jumeirah Campus
 Singapore 238591

MAIN CONTRACTOR:

WOH HUP (PRIVATE) LIMITED
 271 North Bridge Road
 100 Beach Road # 04 - 01
 Tel: 65-4377-8777 Fax: 65-4377-8438 Email: info@woh.com.sg

PROJECT TITLE:

W RESIDENCES MARINA VUE - SINGAPORE

PROPOSED NEW DETACHED OF 51 STOREY MIXED USE DEVELOPMENT COMPRISING 5 STOREY HOTEL AND COMMERCIAL, 8 STOREY HOTEL, 150 ROOMS, 36-21 STOREY RESIDENTIAL PLATS AND UNITS AND 2 BASEMENTS ON LOT 504/6 and 504/6B TO 30 AND SUBTERRANEAN SPACES LOT 503/6 TO 30 AT MARINA VUE (CONJUNCTION CORE PLANNING AREA).

DRAWING TITLE:

RESIDENTIAL

19TH - 33RD, 36TH - 48TH STOREY

CONCRETE BODY PLAN

DESIGNED : JC

CHECKED : JCCY

DRAWN : KGN

APPROVED : Approver

DATE : 26/MAR/2026

SCALE : As Indicated

DWG NO :

MVR_RES_CO_WH_CST_ZZ_ZZ_DG_W_0203_A0_REV

LEGEND:
 RC WALL / COLUMN
 RC WALL / COLUMN BELOW
 DOUBLE SLAB
 MASS CONCRETE
 NON-STRUCTURAL RC WALL
 NON-STRUCTURAL RC WALL FOR AMALGAMATION
 IMPACT WALL/PARAPET WALL
 RECESS
 DOWNPUMP WALL
 BUILD-UP WALL
 STEEL MESH
 TEMPORARY BEAM
 TEMPORARY OPENING
 MUCKHOLE
 SHIELDING WALL
 SG/SBS SLAB STRENGTHENING BOUNDARY
 RECESS SCOFF
 RC WALL / COLUMN w/w WATERPROOFING ADMIN
 SLAB STRENGTHENING DUE TO FACADE
 SLAB THICKNESS
 FOR CONFIRMATION
 REVISION
 WALL WITH 10mm SKIRTING RECESS
 HEIGHT = 120mm from FFL
 WALL WITH 10mm SKIRTING RECESS
 HEIGHT = 300mm from FFL (NET AREAS)

GENERAL NOTES

- SLAB DROPPERS LOCATION & SIZE, STAIRCASE DETAILS, FLY, E.C. WALL, OPENING LOCATION & SIZE REFER TO LATEST ARCH. SETTING OUT PLAN.
- M&E PRELIMINARIES AND OPENING SETTING-OUT INVERT LEVELS LOCATION REFER TO LATEST M&E CONSTRUCTION DRAWING.
- ALL LIFT UP/ DOWN REFER TO LATEST M&E DRAWING.
- ALL WASTE SURPACIS SIZE & INVERT LEVEL REFER TO LATEST M&E DRAWING.
- ALL LIFTS DOWN OPENING TO REFER TO LATEST M&E DRAWING.
- ALL DOUBLE SLAB SHALL BE 150mm THK U.O.L.

RESIDENTIAL LEVEL (TYPICAL)

FLOOR	LIFT LOBBY FFL	UNIT FFL
17TH STOREY	73.875	73.925
18TH STOREY	73.200	73.250
19TH STOREY	82.525	82.575
20TH STOREY	85.800	85.850
21TH STOREY	89.175	89.225
22TH STOREY	92.500	92.550
23TH STOREY	95.825	95.875
24TH STOREY	99.150	99.200
25TH STOREY	102.475	102.525
26TH STOREY	105.800	105.850
27TH STOREY	109.125	109.175
28TH STOREY	112.450	112.500
29TH STOREY	115.775	115.825
30TH STOREY	119.100	119.150
31TH STOREY	122.425	122.475
32TH STOREY	125.750	125.800
33TH STOREY	129.075	129.125
34TH STOREY	132.400	132.450
35TH STOREY	135.725	135.775
36TH STOREY	139.050	139.100
37TH STOREY	142.375	142.425
38TH STOREY	145.700	145.750
39TH STOREY	149.025	149.075
40TH STOREY	152.350	152.400
41TH STOREY	155.675	155.725
42TH STOREY	159.000	159.050
43TH STOREY	162.325	162.375
44TH STOREY	165.650	165.700
45TH STOREY	168.975	169.025
46TH STOREY	172.300	172.350
47TH STOREY	175.625	175.675
48TH STOREY	178.950	179.000
49TH STOREY	182.275	182.325
48TH STOREY	185.600	185.650

(XD)

1. L36-L48 PBU TYPE 2xM PART PLAN
SCALE 1 : 50

(PJ)

2. L36-L48 PBU TYPE 2xM PART PLAN
SCALE 1 : 50

DETAIL-1
SCALE 1:10

9. DETAIL-2
SCALE 1:10



REFERENCES:

Arch: 250917_BFAU/MAR/ARCH/MA/145A
 MAR: 251110_MAR/251110_STOREY/ OVERLAY 1 PBU/ Penetration


GABLE END & INTERNAL WALL THICKNESS REDUCTION

EXTERNAL CASE: GABLE END WALL


INTERNAL CASE: INTERNAL UNIT WALL

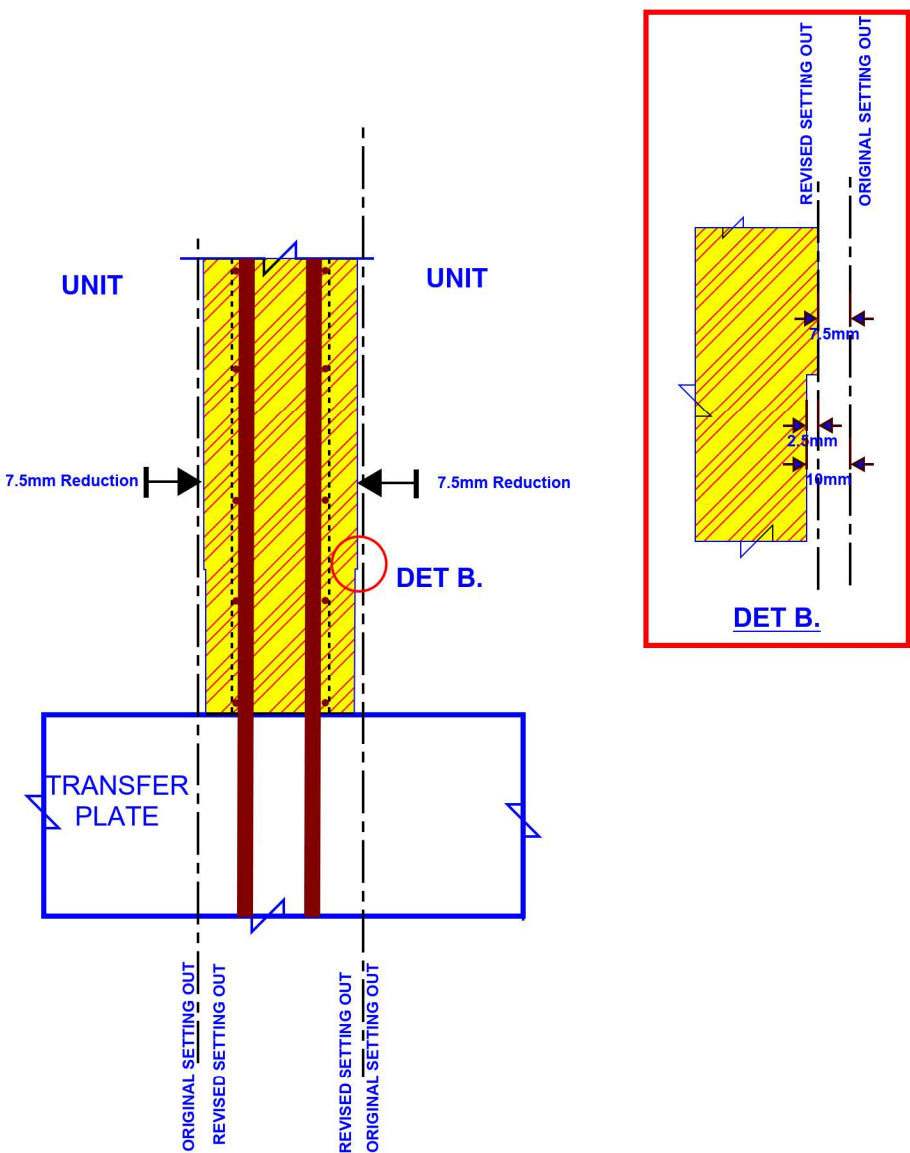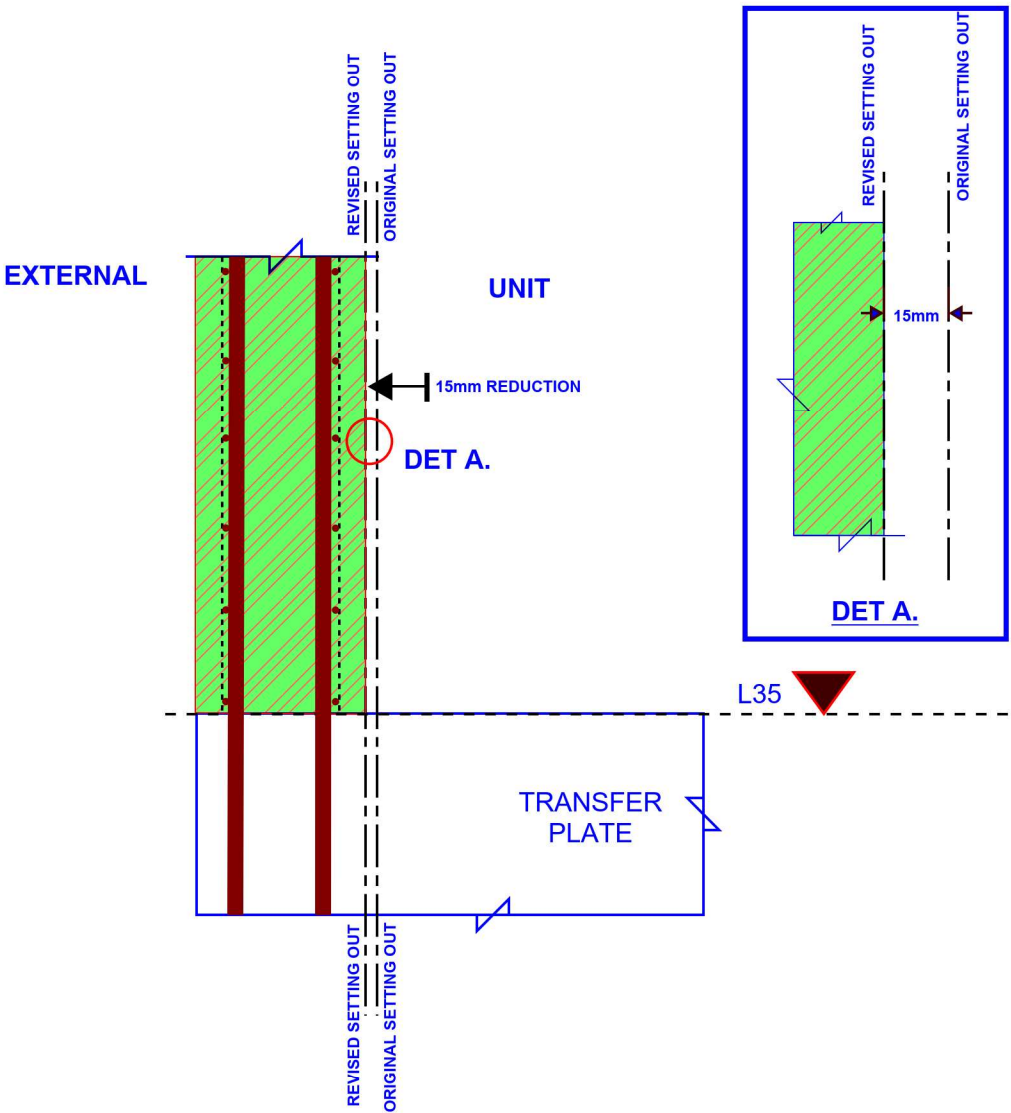

NOTE:
CONCRETE COVER SHALL REMAINED AS PER KTP GENERAL NOTE:
WALL - 35MM

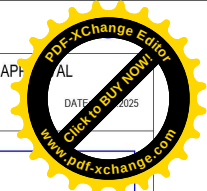


MVR PJW_CO_WH_CST_ZZ_ZZ_SK_W_2543A
ResResi RC Wall Recess due to Skirting & Waterproofing Overlap Rev A

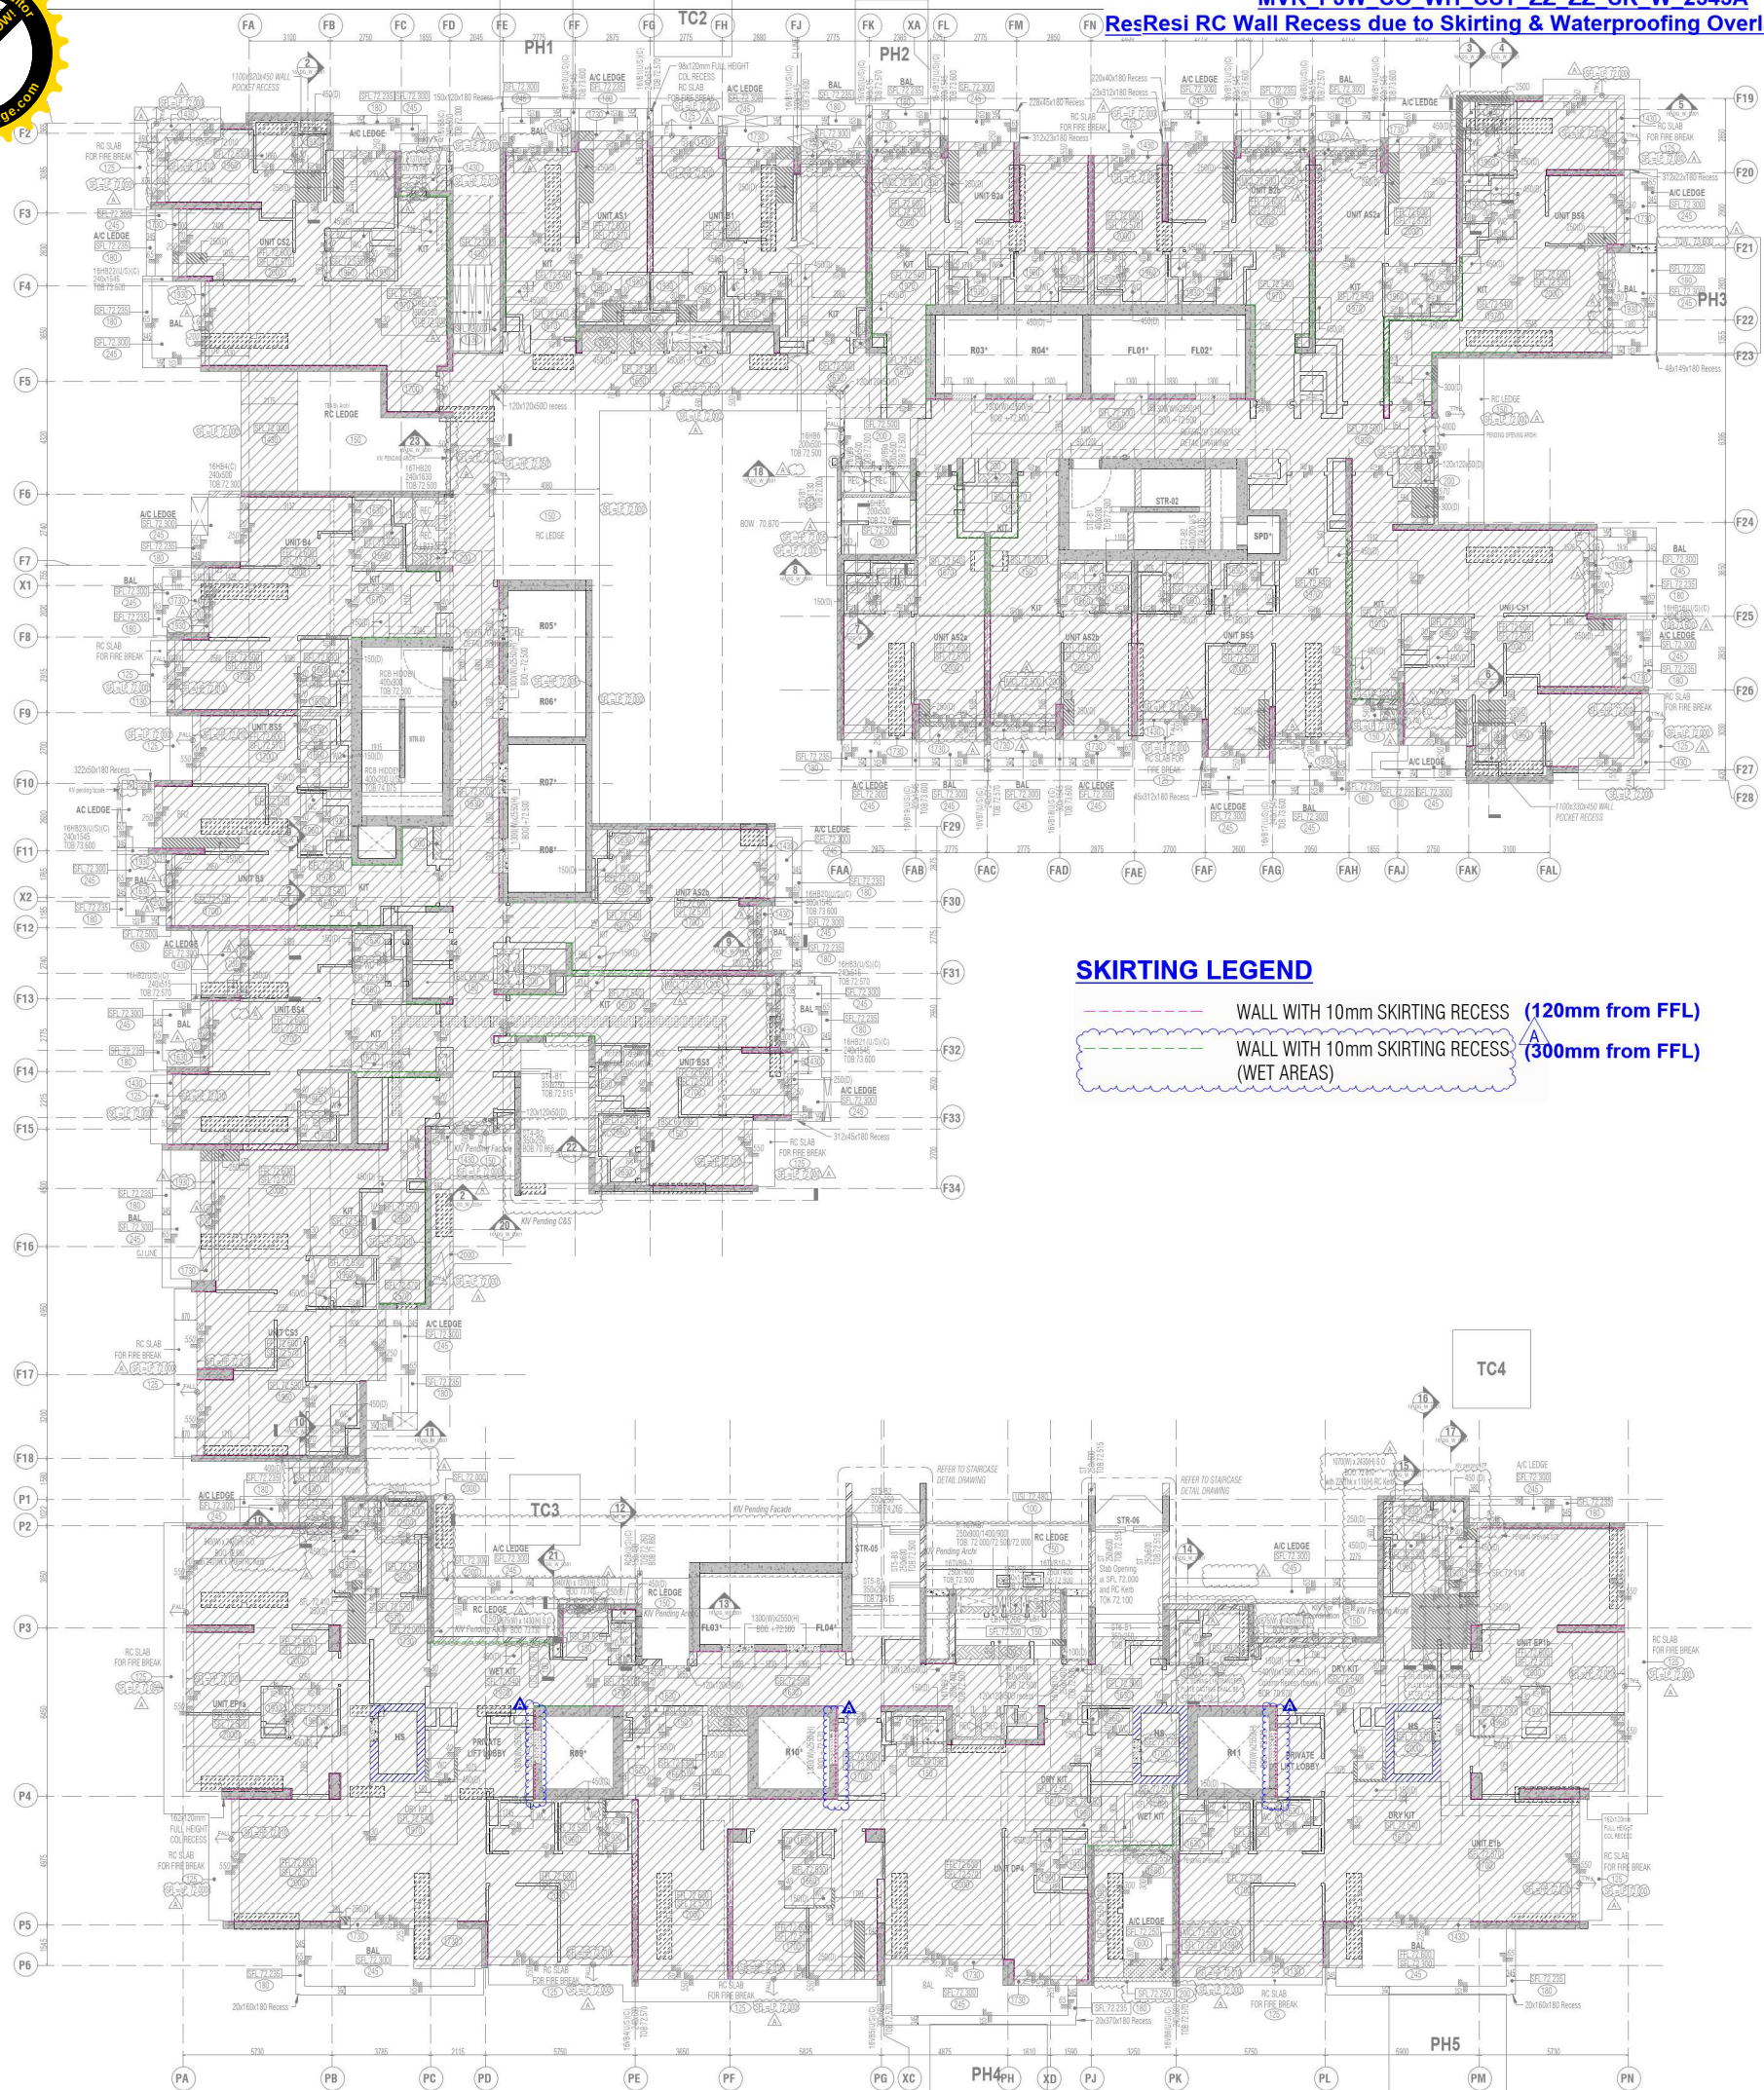


SKIRTING LEGEND

- WALL WITH 10mm SKIRTING RECESS (120mm from FFL)
- WALL WITH 10mm SKIRTING RECESS (300mm from FFL) (WET AREAS)

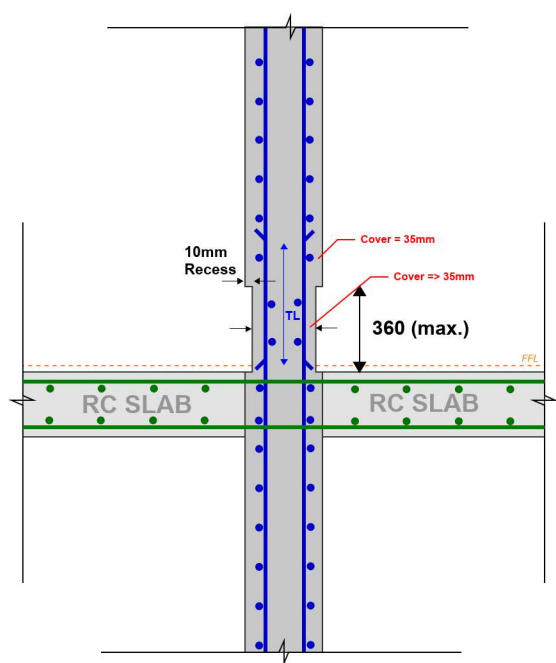

RESI RC WALL SKIRTING RECESS DETAIL

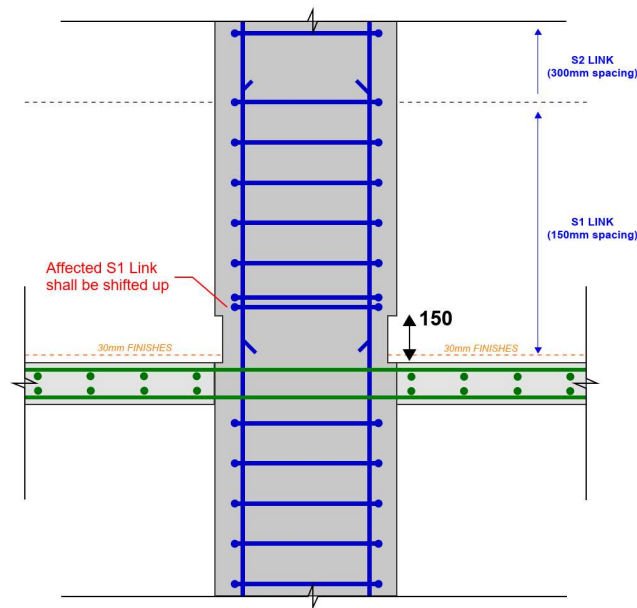

RESI RC COLUMN SKIRTING RECESS DETAIL

DETAIL DISCUSSED AND CONFIRMED WITH KTP
IN TECHNICAL MEETING DATED 25-FEB-25

FOR CONSTRUCTION

16 Oct 2025

TECHNICAL
WOH HUP (PRIVATE) LIMITED
MARINA VIEW RESIDENCES (MVR)

- Copy to
1. PD - Chen Han Qi
 2. PM - Wong Wei Siong
 3. SE
 4. RE/RTO
 5. All Subcons
 6. MVR WH, MVR Site
 7. WH QS
 8. WH Rebar Scheduler
 9. DC
 10. IOI - Muliadi, How See, Darren

From: Joseph Chin
16-Oct-25

GENERAL NOTES:
1. ALL DIMENSIONS ARE TO BE IN 'mm' UNLESS OTHERWISE STATED.
2. ALL DIMENSIONS ARE SUBJECT TO SITE VERIFICATION.
3. DO NOT SCALE ON DRAWINGS.
4. ANY DISCREPANCY MUST BE REPORTED TO MAIN CONTRACTOR IMMEDIATELY.
5. ALL DRAWINGS MUST BE USED IN CONJUNCTION WITH M&E AND STRUCTURAL DRAWINGS.

REFERENCED DRAWING NO.

1. ARCHITECTURAL REFERENCE DWG.
2. STRUCTURAL REFERENCE DWG.
3. WH/ME REFERENCE DWG.
4. OTHERS

REV	DATE	DESCRIPTION	BY	CHECKED
A	17.09.25	REVISED AC TRA MVR/RC WH/11A	KQCB	JC
B	25.09.25	FOR APPROVAL	PHT	JC



DEVELOPER/LAND OWNER:
Boulevard Development Pte Ltd
Boulevard Midtown Pte Ltd
38 Beach Road #04-11,
South Beach Tower, Singapore 189817
Tel: 65-6338-8111

ARCHITECT:
architects61
architecture
planning
architect 61 pte ltd
150 beach road # 04-01
Tel: 65-6732-5438
architect 61 pte ltd
150 beach road # 04-01
Tel: 65-6732-5438

CIVIL & STRUCTURAL ENGINEER:
KTP
KTP Consultants Pte Ltd
150 Beach Road
Tel: 65-6732-5438

MEP CONSULTANT:
KTP
KTP Consultants Pte Ltd
150 Beach Road
Tel: 65-6732-5438


QUANTITY SURVEYOR:
threesixty
Threesixty Cost Management Pte Ltd
(Threesixty)
150 Beach Road
Tel: 65-6732-5438

MAIN CONTRACTOR:
WOH HUP (PRIVATE) LIMITED
150 Beach Road
Tel: 65-6732-5438


PROJECT TITLE:
W RESIDENCES MARINA VIEW - SINGAPORE
PROPOSED NEW ERECTION OF 14 STOREY MIXED USE DEVELOPMENT COMPRISING
3 STOREY HOTEL AND CARPARK PODIUM, 1 STOREY HOTEL, 100 ROOMS, 96 3P
STOREY RESIDENTIAL FLATS (80 UNITS) AND 2 BASEMENTS ON LOT 0068/06 AND
SHAWA 15.30 ARE AND WATERFRONT MARINA SPACE LOT 0007/02 TO 30 AT MARINA VIEW
(DOWNTOWN CORE PLANNING AREA)

DRAWING TITLE:
RESIDENTIAL
16TH STOREY
CONCRETE BODY PLAN

DESIGNED: JC	CHECKED: JC
DRAWN: PHT	APPROVED: Approver
DATE: 17.09.2025	SCALE: As indicated
DWG NO: MVR_RES_CO_WH_CST_ZZ_16.DG_W_0201	SIZE: A0
REV: A	REV: A

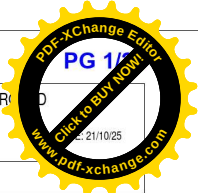

L17-L33 & L36-L48 Typical Resi Floor Slab, Beam & Wall Penetration Rev 15

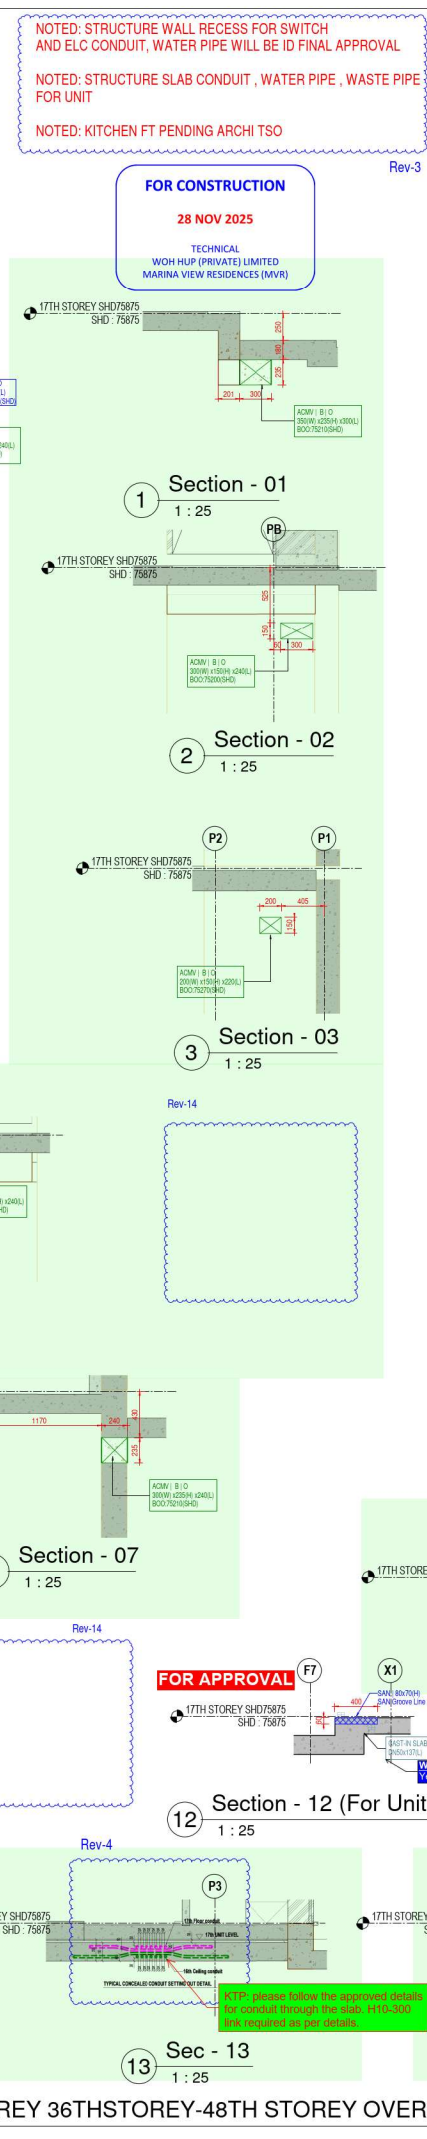

DATE RECEIVED: _____ DATE RETURNED: _____
 CHECKED BY: _____ SUBMISSION NO: _____

☐ IN PRINCIPLE NO OBJECTIONS, EXCEPT FOR AND SUBJECT TO COMPLIANCE TO THE REQUIREMENTS AND COMMENTS AS ATTACHED FOR CONTRACTOR'S FULL COMPLIANCE AT NO COST AND IMPRISONMENT.

☐ IN PRINCIPLE NO OBJECTIONS (PARTIAL) - FOR ARI USE ONLY, REFER TO COMMENTS.

☐ REWIS AND RESUBMIT COMPLIANT TO COMMENTS NOT TO PROCEED. RESUBMISSION REQUIRED.

☐ REJECTED TO RESUBMIT. DRAWINGS ARE NOT IN ORDER.

☐ NO COMMENTS, NOT OUR SCOPE.

COMMENTS AND CORRECTIONS MADE ON THIS SHOP DRAWING DO NOT RELIEVE THE CONTRACTOR OF HIS RESPONSIBILITIES FOR THE DESIGN, RESPONSIBILITIES AND FROM COMPLIANCE WITH REQUIREMENTS OF THE SPECIFICATIONS AND DRAWINGS. CHECK FOR ANY REVISION OF GENERAL REQUIREMENTS WITH THE DESIGN CONCEPT OF THE PROJECT AND GENERAL COMPLIANCE WITH THE REQUIREMENTS OF THE SPECIFICATIONS AND DRAWINGS. THE CONTRACTOR IS RESPONSIBLE FOR CONFIRMING AND CORRELATING ALL DIMENSIONS, MATERIALS, METHODS, AND TECHNIQUES OF CONSTRUCTION COORDINATING HIS WORK WITH THAT OF ALL OTHER TRADES AND PERFORMING HIS WORK IN A SAFE AND SATISFACTORY MANNER.


 Date: 21/10/25
www.pdf-xchange.com

DATE RECEIVED : _____

SHOP DRAWING REVIEW BY :

	APPROVED			
	For Contractor (JWS)	ASE Consultants (Responsible JWS)	ASE Consultants (Responsible JWS)	Respected (Responsible comments)
☐ ARCHITECT Architects of Pte Ltd				
☐ CIVIL & STRUCTURAL ENGINEER JSP Consultants Pte Ltd				
☐ MEP CONSULTANT JSP Engineers (S) Pte Ltd				

TOO	TOP OF OPENING
BOO	BOTTOM OF OPENINGS
BOT	BOTTOM
TL	TOP LEFT
IL	INVERT
PS	PIPE SIZE
PF	PUDDLE
RE	RETURN
PLI	FRESH
GIC	CAST IN
CIC	CAST IN
GIC	CAST IN
CITL	CAST IN
CIFT	CAST IN
CIT	CAST IN
O	OPENING
W	WALL
S	SLAB
C	COLUMN
R	BEAM
SHD	SINKAP
DN	DIAMETER

1. PD - Chen Han Qi
2. PM - Wong Wei Siong
3. SE
4. RE/RTO
5. All Subcons
6. MVR WH, MVR Site
7. WH QS
8. WH Rebar Scheduler
9. DC
10. IOI - Muliadi, How See, Darren

HSPS	HOLLOW SLAB PIPE SLEEVE
DS	DRAIN SLAB
IC	INJECTION CHAMBER
LFX	LIGHTING FIXTURE
ERT	ERTH PARTITION
MHL	MANHOLE
PL	POLE LIGHT
GAS	GAS PIPE
FA	FIRE ALARM
SAL	SANITARY
PLM	PLUMBING
PRL	PREFR
GEN	GENSET
ELC	ELECTRICAL
LFT	LOW LIGHT
LTE	LIGHT
RW	RAIN WATER
ACM/	AIR CONDITIONING AND MECHANICAL VENTILATION
BMS	BUILDING MANAGEMENT SYSTEM
SCV	SECURITY
WCS	WASTE COLLECTION SYSTEM
ME	MECHANICAL AND ELECTRICAL, GENERAL
SK	SKIN ON 40 CAST-IN PIPE
WD	DISH WASHER 1 DN 50 CAST-IN PIPE
WD	WASHER & DRYER 1 DN 50 CAST-IN PIPE
NP	DN 50 CAST-IN PIPE
NP	DN 50 PIPE SLEEVE

	BLANK OPENING
	SLAB OPENING COLORS SYSTEM
	SLAB OPENING FOR AC SYSTEM
	SLAB OPENING FOR ELV SYSTEM
	SLAB OPENING FOR TELV SYSTEM
	SLAB OPENING FOR GAS SYSTEM
	SLAB OPENING FOR AB SYSTEM
	SLAB OPENING FOR SAN SYSTEM
	SLAB OPENING FOR CARPARK WASTE SYSTEM
	SLAB OPENING FOR KITCHEN WASTE SYSTEM
	SLAB OPENING FOR SPK SYSTEM
	SLAB OPENING FOR RWSP SYSTEM
	SLAB OPENING FOR SECURITY SYSTEM
	SLAB OPENING FOR WASTE COLLECTION SYSTEM
	TEMPORARY BEAM
	CEILING CONCEALED CONDUIT
	FLOOR CONCEALED CONDUIT
	DOWN CONDUCTOR

REV	DATE	DESCRIPTION	BY	CHECK
<u>KEY PLAN:</u>				

38 Beach Road #34-11,
South Beach Tower, Singapore 189757
Tel: 65-6338-8111

architects61

architect 61 pte ltd co reg no. 199201400
150 beach road # 04 - 01 gateway west singapore 189
tel: 65.6737 5977 fax: 65.6732 5439 a61@a61.com.sg www.a61.com.sg

CIVIL & STRUCTURAL ENGINEER

K T P

Member of the Salsana Jurong Group

KTP Consultants Pte Ltd
158 Jalan Bukit Merah, #01-01,
Connection One, Singapore 150158
Tel : 6273 5622 Fax : 6273 8434

MEP CONSULTANT:

 152 BEACH ROAD
#07-01/04 GARDENWAY EAST Singapore 118972
Tel: (65) 67320288 Fax: (65) 67320988

J. ROGER PRESTON (S) PTE LTD
MECHANICAL & ELECTRICAL CONSULTING ENGINEERS

threesixty
Cost Management
Threesixty Cost Management Pte Ltd
(Threesixty)
38 Cleartech Loop
#01-31 Surbana Jurong Campus
Singapore 637631

WOH HUP (PRIVATE) LIMITED
BUILDING WITH INTEGRITY
277 Upper Bukit Timah Road
Woh Hup Building Singapore 588145
Tel: 63968595 Fax: 62703832


MARINA VIEW
PROPOSED NEW ERECTION OF 51 STOREY MIXED USE DEVELOPMENT COM-
5 STOREY HOTEL AND CARPARK PODIUM, 9 STOREY HOTEL (350 ROOMS), 36/
STOREY RESIDENTIAL FLATS (883 UNITS) AND 2 BASEMENTS ON LOT 00483A/
00484N TS 30 AND SUBTERRANEAN SPACE LOT 80072G TS 30 AT MARINA VIEW

17TH STOREY-33TH STOREY 36THSTOREY-48TH
STOREY OVERALL PLAN


DESIGNED : CHIEN/ESTHER	CHECKED : JOHN
REVIEW : MATHIAS/JOHN	APPROVED : J. J.

DATE : 21/10/25	SCALE : As indicated
DWG NO :	SIZE :

| MVD DEC 20 11 44 MED TVD 77 MR W 0001 | AN

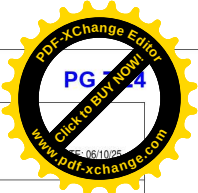

MVR PJW CO WH CST ZZ ZZ SK W 2564B

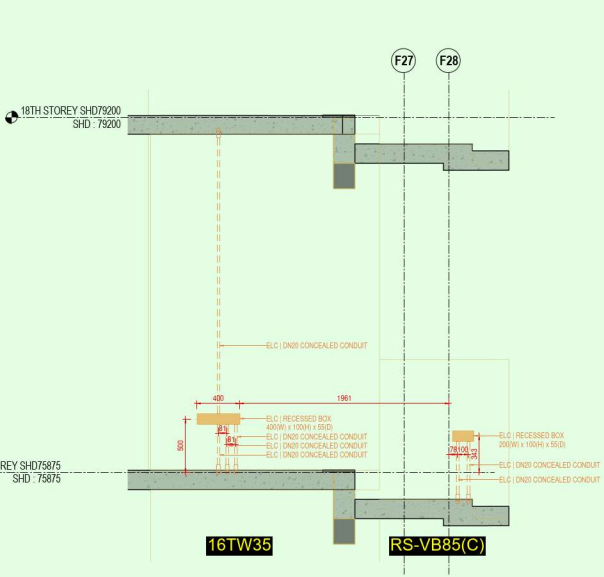


PRIMA VIEW RESIDENCE:


ALL DRAWINGS MUST BE USED IN CONJUNCTION WITH THE
STRUCTURAL DRAWINGS.

[illegible]

	0	100	200	
--	---	-----	-----	-----	-----	-----	-----	-----	-----	-----	------	------	-------


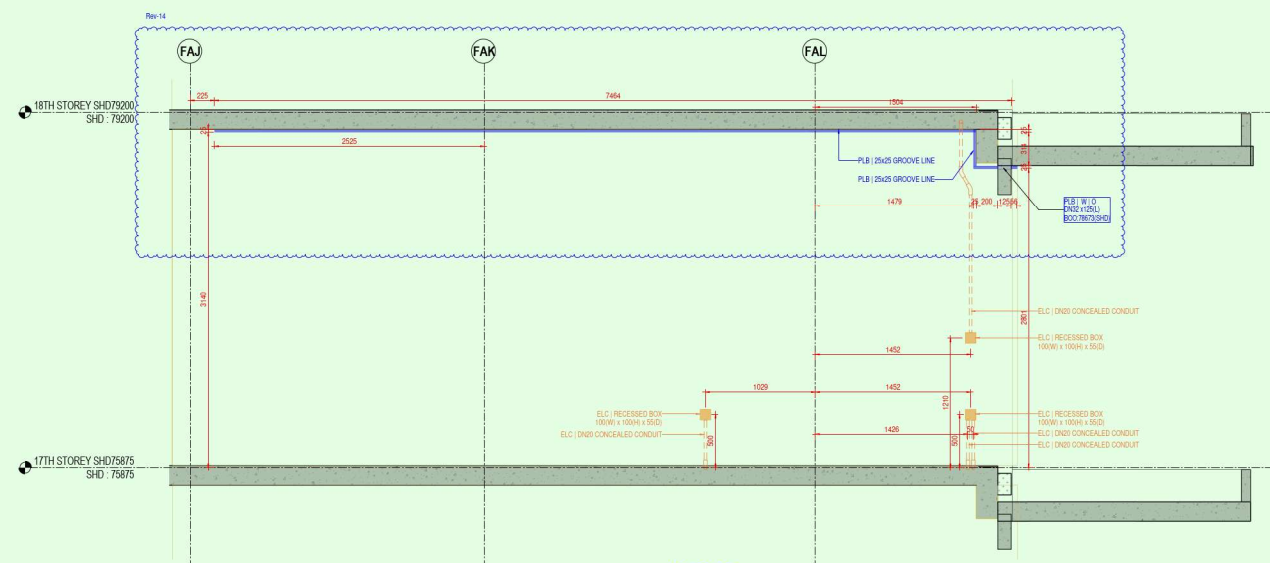


55 C1-2
1 : 25

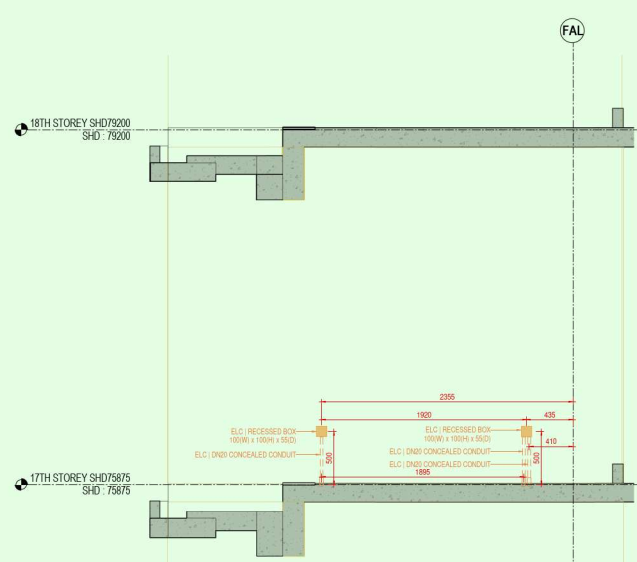

16TW40
C1-6
59

KTP: No objection, all penetrations/recesses please follow previous approved details

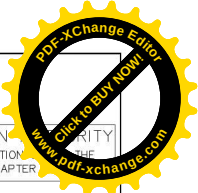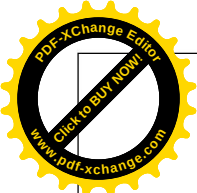

for Commissioner of Building Control

DT-MVR-C&S-227

FOR CONSTRUCTION

16 JUL 2026

TECHNICAL
WOH HUP (PRIVATE) LIMITED
MARINA VIEW RESIDENCES (MVR)

PE'S CERTIFICATION



AC'S CERTIFICATION

ACCREDITED CHECKER

NO: 1089

KOK KING MIN
In AC Organisation
Registration No: A054
BUILDING CONTROL ACT
SINGAPORE

CONSTRUCTION DRAWING

ISSUED

13 JULY 2026

KTP CONSULTANTS PTE. LTD.

5	REVISED WALL DETAIL				25.05.26
4	REVISED WALL DETAIL				22.05.26
3	REVISED WALL DETAIL				09.03.26
2	REVISED WALL DETAIL				24.02.26
1	REVISED WALL DETAIL				10.02.26
REV	AMENDMENTS	DR	DES	CHK	DATE

PROJECT

PROPOSED NEW ERECTION OF 51 STOREY MIXED USE DEVELOPMENT COMPRISING 5 STOREY HOTEL AND CARPARK PODIUM, 9 STOREY HOTEL (350 ROOMS), 36/37 STOREY RESIDENTIAL FLATS (683 UNITS) AND 2 BASEMENTS ON LOTS 00483K AND 00484N TS 30 AND SUBTERRANEAN SPACE LOT 800772C TS 30 AT MARINA VIEW (DOWNTOWN CORE PLANNING AREA)

ARCHITECT

ARCHITECT 61 PTE. LTD.

KTP **KTP Consultants Pte Ltd**
Surbana Jurong Campus 38 CleanTech
Loop, #01-31 Singapore 636741
Tel : +65 6248 1288

DRAWN: CH DATE: DESIGNED: JS/AP/PS

SCALE: AS SHOWN CHECKED: Chwa/L

DWG. NO. 21.070/WD11

WALL DETAILS-11

THE OWNERSHIP OF THE COPYRIGHT IN THIS DRAWING IS RETAINED BY KTP CONSULTANTS
WHOSE CONSENT MUST BE SOUGHT BEFORE ANY USE OR REPRODUCTION OF THE DRAWING
OR ANY PART THEREOF CAN BE MADE.

