



Cut & Bend Rebar – JOB ADVICE

工作通知 Fax:6261 9133

BBS No 钢筋加工表	<u>MVR-TT-H393</u>	Total Weight 总重量	<u>890</u>
Contract 合同号码		Total Pages Attached 统计页数	1+6
Customer 承包商	<u>WOH HUP PTE LTD</u>	Gate:	
Project Title 筑工地址	<u>MARINA VIEWLP 28F 1 STRAITS BIVD,SINGAPORE 018906</u>		
Description 形容	L39层CJ4-2 板 B1		
Date Order 订单日期	14-Sep-2026	Date Required 交货日期	21-Sep-2026
Remarks 评论			
Check/Approved By 检查/审核/订货人	<u>Zhou Bing</u>	Handphone 手提电话	<u>9847 1699</u>
Site Contact Person 联络人	<u>Kumar</u>	Handphone 手提电话	<u>8133 8587</u>
Material Receiver 收货人	<u>SIVA</u>	Handphone 手提电话	<u>8426 2921</u>
Site Telephone 工地电话		Site Fax No 传真号码	
Scheduler 开料人	<u>Lu Yong Bing</u>	Handphone 手提电话	<u>8982 7022</u>
<u>***Please Allow 5 days for ??? To Process Your Order***</u>			
<u>51 Tuas South Street 5,Singapoer637644</u>			

Name	Contact numbers	Email Address
project Coodinator	Leslie LIM	8524 2927



PROJECT :	MARINA VIEWLP 28F 1 STRAITS BIVD,SINGAPORE 018906		Pg. 1 / 6
BBS No:	MVR-TT-H393	Rev.	Date : 2026/9/14
Dwg. No.		Rev.	Prepared By:
TITLE:	L39层CJ4-2 板 B1		BBS NO: MVR-TT-H393

BAR BENDING SCHEDULE

MEMBER	BAR MARK	TYPE & SIZE	NO. OF MBRS	NO. OF EACH	TOTAL	SHAPE CODE	SHAPE	CUT OFF LENGTH	WEIGHT
					B1				
	43	H 10	1	3	3	20		4750	8.78
	44	H 10	1	3	3	37		3300	6.10
	45	H 10	1	5	5	38a		1370	4.22
	46	H 10	1	8	8	38a		880	4.34
	47	H 10	1	12	12	37		8420	62.24
	48	H 10	1	2	2	38a		2450	3.02
	49	H 10	1	14	14	38a		2110	18.20
	50	H 10	1	14	14	37		1830	15.78
	51	H 10	1	6	6	37		5730	21.18
	52	H 10	1	2	2	54		1280	1.58
	53	H 10	1	1	1			2730	1.68
	54	H 10	1	4	4			2030	5.00
	55	H 10	1	1	1	38a		1480	0.91
	56	H 10	1	2	2	38a		1230	1.52
	57	H 10	1	3	3	38a		570	1.05
	58	H 10	1	3	3			2520	4.66
	59	H 10	1	3	3			3970	7.34

REBAR SIZE		R06	H08	H10	H13	H16	H20	H25	H32	H40	TOTAL
WEIGHT				####							167.6 KG



PROJECT :		MARINA VIEWLP 28F 1 STRAITS BIVD,SINGAPORE 018906	Pg. 2 / 6
BBS No:		MVR-TT-H393	Rev. Date : 2026/9/14
Dwg. No.			Rev. Prepared By:
TITLE:		L39层CJ4-2 板 B1	BBS NO: MVR-TT-H393

BAR BENDING SCHEDULE

MEMBER	BAR MARK	TYPE & SIZE	NO. OF MBRS	NO. OF EACH	TOTAL	SHAPE CODE	SHAPE	CUT OFF LENGTH	WEIGHT
	60	H 10	1	2	2			3580	4.41
	61	H 10	1	11	11	38a		5540	37.54
	62	H 10	1	1	1	53		6540	4.03
	63	H 10	1	1	1	20		6500	4.00
	64	H 10	1	18	18	37		6550	72.63
	65	H 10	1	18	18	20		6250	69.30
	66	H 10	1	2	2	38a		3200	3.94
	67	H 10	1	4	4	38a		1600	3.94
	68	H 10	1	11	11	37		1370	9.28
	69	H 10	1	11	11			1100	7.45
	70	H 10	1	13	13	38a		2020	16.18
	71	H 10	1	13	13	38a		2020	16.18
	72	H 10	1	2	2	38a		3200	3.94
	73	H 10	1	11	11	37		1370	9.28
	74	H 10	1	11	11			1100	7.45
	75	H 10	1	4	4	38a		1600	3.94
	76	H 10	1	13	13	38a		1130	9.05
	77	H 10	1	2	2	54		880	1.08

REBAR SIZE		R06	H08	H10	H13	H16	H20	H25	H32	H40	TOTAL
WEIGHT				####							283.6 KG



PROJECT :	MARINA VIEWLP 28F 1 STRAITS BIVD,SINGAPORE 018906	Pg. 3 / 6
BBS No:	MVR-TT-H393	Rev. Date : 2026/9/14
Dwg. No.		Rev. Prepared By:
TITLE:	L39层CJ4-2 板 B1	BBS NO: MVR-TT-H393

BAR BENDING SCHEDULE

MEMBER	BAR MARK	TYPE & SIZE	NO. OF MBRS	NO. OF EACH	TOTAL	SHAPE CODE	SHAPE	CUT OFF LENGTH	WEIGHT
	78	H 10	1	1	1			2780	1.71
	79	H 10	1	4	4			2030	5.00
	80	H 10	1	3	3			2510	4.64
	81	H 10	1	2	2	38a		300	0.37
	82	H 10	1	2	2	38a		2590	3.19
	83	H 10	1	2	2	38a		2090	2.57
	84	H 10	1	3	3	38a		810	1.50
	85	H 10	1	1	1	38a		2050	1.26
	86	H 10	1	2	2	38a		300	0.37
	87	H 10	1	4	4	38a		1300	3.20
	88	H 10	1	1	1	38a		2350	1.45
	89	H 10	1	2	2	38a		1860	2.29
	90	H 10	1	1	1			6930	4.27
	91	H 10	1	2	2	54		4530	5.58
	92	H 10	1	2	2	54		6130	7.55
	93	H 10	1	1	1	54		4130	2.54
	94	H 10	1	1	1	54		5780	3.56
	95	H 10	1	1	1	53		7150	4.40

REBAR SIZE		R06	H08	H10	H13	H16	H20	H25	H32	H40	TOTAL
WEIGHT				55.5							55.5 KG



PROJECT :		MARINA VIEWLP 28F 1 STRAITS BIVD,SINGAPORE 018906						Pg. 4 / 6		
BBS No:		MVR-TT-H393					Rev.	Date : 2026/9/14		
Dwg. No.							Rev.	Prepared By:		
TITLE:		L39层CJ4-2 板 B1						BBS NO: MVR-TT-H393		
BAR BENDING SCHEDULE										
MEMBER	BAR MARK	TYPE & SIZE	NO. OF MBRS	NO.O F EACH	TOTAL	SHAP E CODE	SHAPE		CUT OFF LENGTH	WEIGHT
	96	H 10	1	1	1	38a	100 1500 100		1700	1.05
	97	H 10	1	4	4	38a	100 500 100		700	1.72
	98	H 10	1	5	5		350 230 230 100		910	2.80
	99	H 10	1	4	4	38a	100 330 100		530	1.31
	100	H 10	1	1	1		350 230 1150 100		1830	1.13
	101	H 10	1	3	3		350 230 1820 100		2500	4.62
	102	H 10	1	11	11	37	170 2630		2800	18.97
	103	H 10	1	1	1	20	3300		3300	2.03
	104	H 10	1	1	1	20	5400		5400	3.33
	105	H 10	1	18	18	20	8000		8000	88.70
	106	H 10	1	4	4	37	100 5500		5600	13.80
	107	H 10	1	3	3	38a	100 2740 100		2940	5.43
	108	H 10	1	9	9	38a	100 1360 100		1560	8.65
	109	H 10	1	5	5	37	100 1430		1530	4.71
	110	H 10	1	5	5		320 130 550 100		1100	3.39
	111	H 10	1	14	14	38a	100 2230 100		2430	20.96

REBAR SIZE		R06	H8	H10	H13	H16	H20	H25	H32	H40	TOTAL
WEIGHT				####							182.6 KG



PROJECT :	MARINA VIEWLP 28F 1 STRAITS BIVD,SINGAPORE 018906	Pg. 5 / 6
BBS No:	MVR-TT-H393	Rev. Date : 2026/9/14
Dwg. No.		Rev. Prepared By:
TITLE:	L39层CJ4-2 板 B1	BBS NO: MVR-TT-H393

BAR BENDING SCHEDULE

MEMBER	BAR MARK	TYPE & SIZE	NO. OF MBRS	NO. OF EACH	TOTAL	SHAPE CODE	SHAPE	CUT OFF LENGTH	WEIGHT
							洞加B		
	17	H 16	1	2	2	37	780 1280	2060	6.51
	18	H 16	1	2	2	37	250 1650	1900	6.00
	19	H 16	1	1	1	38	500 350 600	1450	2.29
	20	H 16	1	1	1	20	2580	2580	4.07
	21	H 16	1	2	2	20	2580	2580	8.15
	22	H 16	1	1	1	37	1100 1300	2400	3.79
	23	H 16	1	2	2	54	250 1300 530	2080	6.57
	24	H 16	1	2	2	20	2400	2400	7.58
	25	H 16	1	2	2	20	3200	3200	10.11
	25a	H 16	2	2	4	20	2700	2700	17.05
	26	H 16	2	2	4	20	2180	2180	13.77
	27	H 16	2	1	2	37	1100 1300	2400	7.58
	28	H 16	1	1	1	38a	600 2390 600	3590	5.67
	28a	H 16	1	1	1	38a	530 2350 530	3410	5.38
	29	H 16	1	1	1	20	4960	4960	7.83
	30	H 16	1	2	2	20	4960	4960	15.66



REBAR SIZE		R06	H08	H10	H13	H16	H20	H25	H32	H40	TOTAL
WEIGHT						####					128 KG





PROJECT :	MARINA VIEWLP 28F 1 STRAITS BIVD,SINGAPORE 018906		Pg. 6 / 6
BBS No:	MVR-TT-H393	Rev.	Date : 2026/9/14
Dwg. No.		Rev.	Prepared By:
TITLE:	L39层CJ4-2 板 B1		BBS NO: MVR-TT-H393

BAR BENDING SCHEDULE									
MEMBER	BAR MARK	TYPE & SIZE	NO. OF MBRS	NO. OF EACH	TOTAL	SHAPE CODE	SHAPE	CUT OFF LENGTH	WEIGHT
	31	H 16	2	1	2	37	650 1670	2320	7.33
	32	H 16	1	2	2	20	2180	2180	6.88
	33	H 16	1	2	2	20	2340	2340	7.39
	34	H 16	1	2	2	37	1030 1100	2130	6.73
	35	H 16	1	1	1	38	500 350 600	1450	2.29
	36	H 16	1	1	1	20	2340	2340	3.69
	37	H 16	1	2	2	20	3180	3180	10.04
	38	H 16	1	1	1	38	400 1750 1130	3280	5.18
	39	H 16	1	2	2	20	2340	2340	7.39
	40	H 16	1	1	1	38	250 1300 400	1950	3.08
	41	H 16	1	2	2	20	2340	2340	7.39
	42	H 16	1	2	2	20	1610	1610	5.08

REBAR SIZE		R06	H08	H10	H13	H16	H20	H25	H32	H40	TOTAL
WEIGHT						72.5					72.5 KG

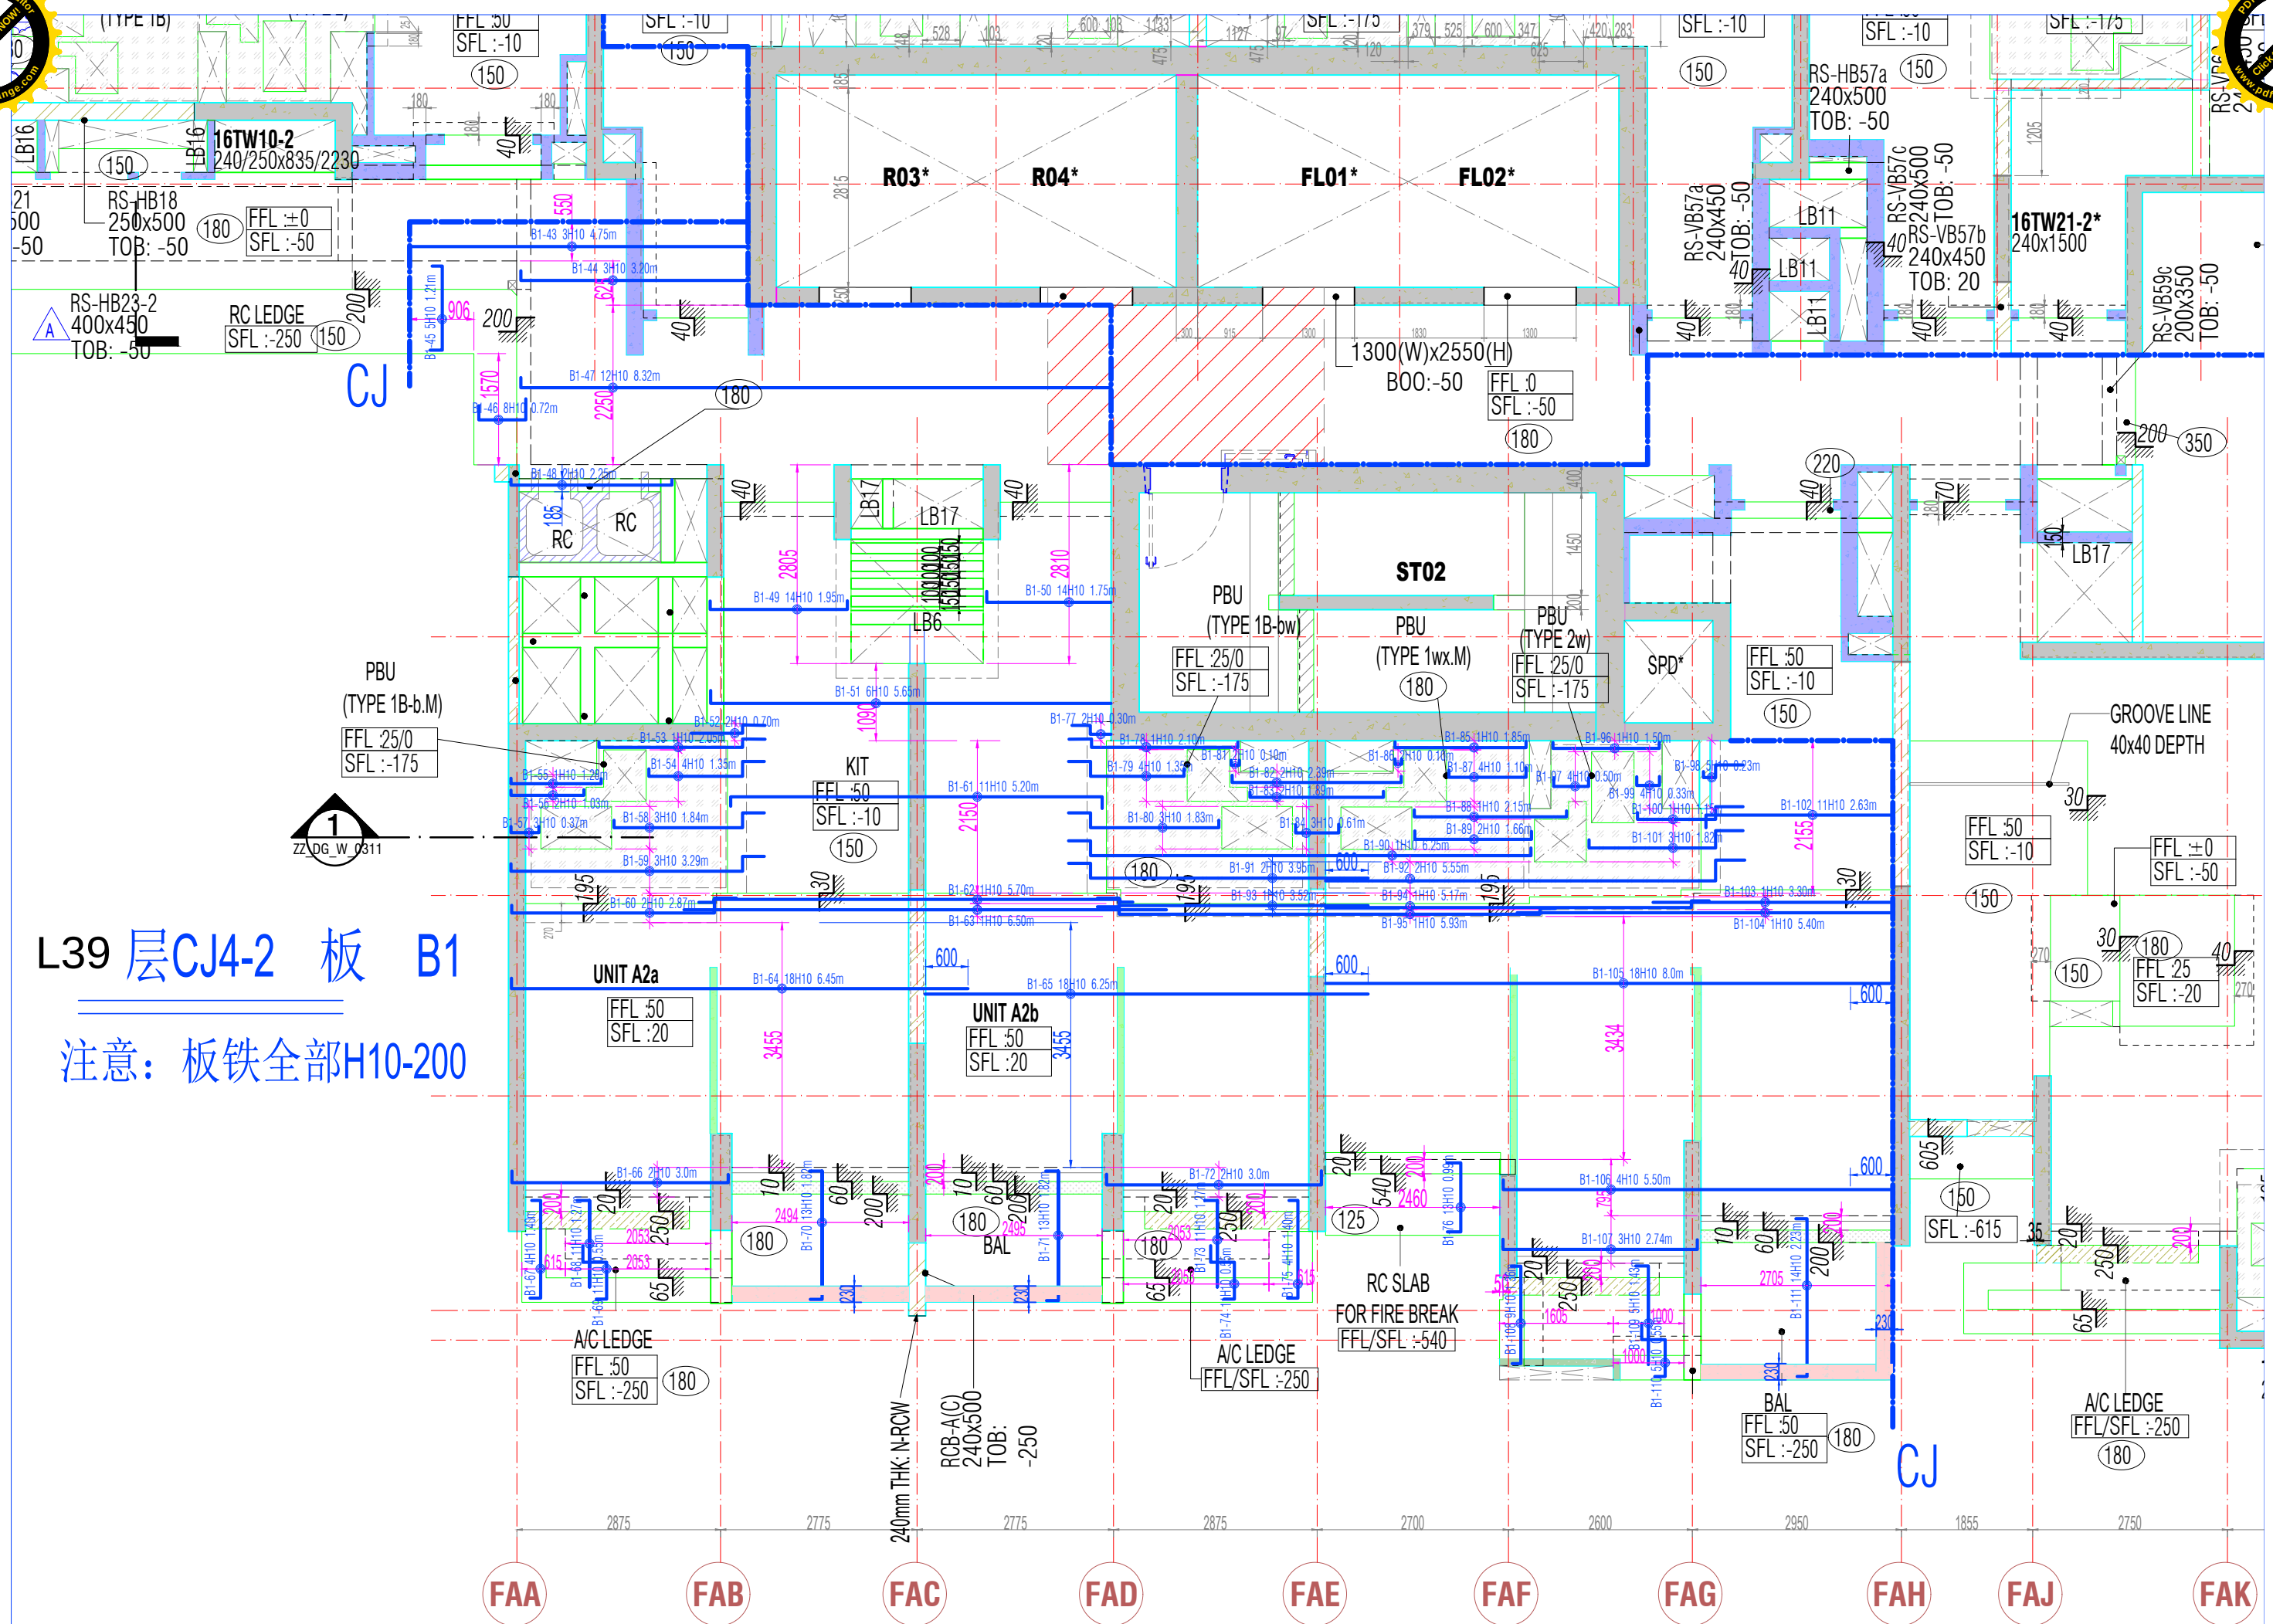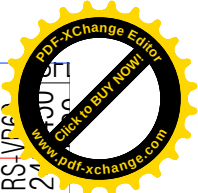

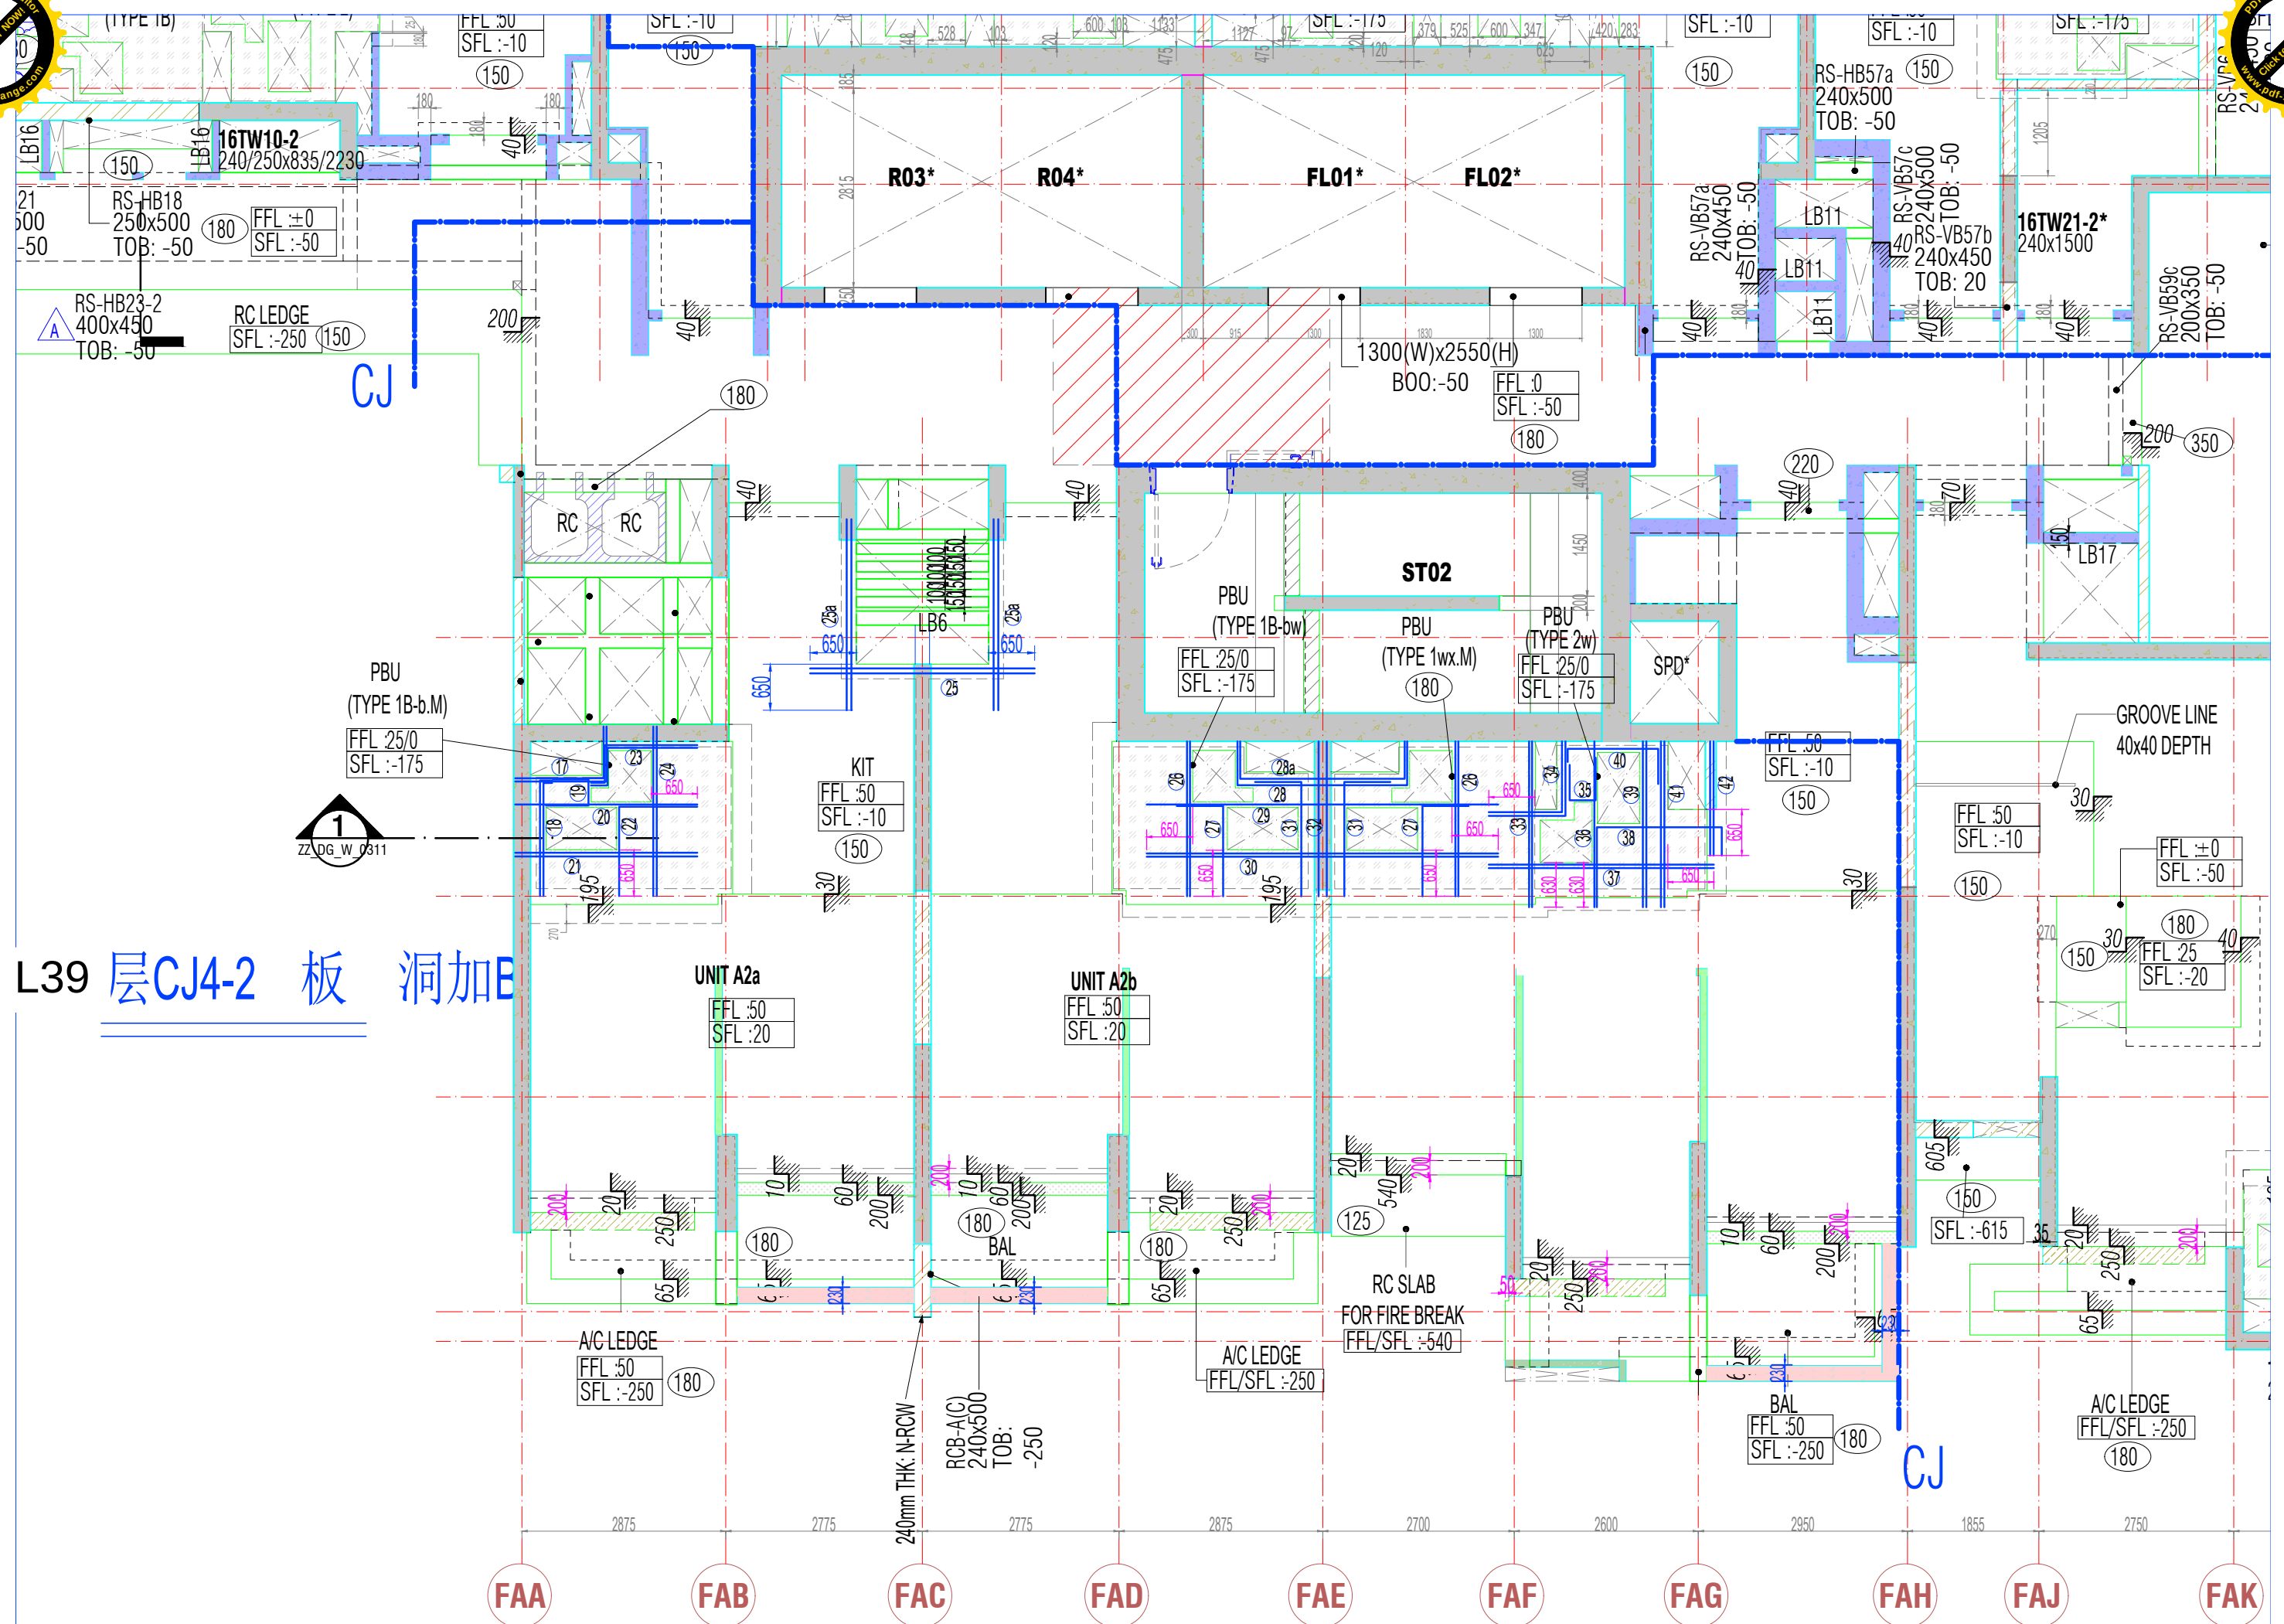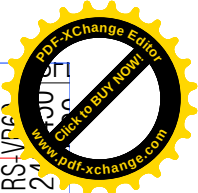



洞加B:

- ①7 2H16 1.28/0.78m

①8 2H16 1.65/0.25m

①9 1H16 0.60/0.35/0.50m

②0 1H16 2.58m

②1 2H16 2.58m

②2 1H16 1.10/1.30m

②3 2H16 1.30/0.53/0.25m

②4 2H16 2.40m

②5 2H16 3.20m

②5a 2*2H16 2.70m
- ②6 2*2H16 2.18m

②7 2*1H16 1.30/1.10m

②8 1H16 0.60/2.39/0.60m

②8a 1H16 0.53/2.35/0.53m

②9 1H16 4.96m

③0 2H16 4.96m

③1 2*1H16 1.67/0.65m

③2 2H16 2.18m
- ③3 2H16 2.34m

③4 2H16 1.03/1.10m

③5 1H16 0.60/0.35/0.50m

③6 1H16 2.34m

③7 2H16 3.18m


③8 1H16 1.13/1.75/0.40m

③9 2H16 2.34m

④0 1H16 0.25/1.30/0.40m

④1 2H16 2.34m

④2 2H16 1.61m

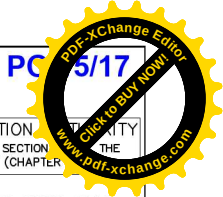

- NOTES:
- UNLESS NOTED OTHERWISE, SLAB REINFORCEMENTS SHALL BE H10-200 (B/W).
 - SLAB THICKNESS SHALL BE 180.
 - REINFORCEMENT LAPPING LENGTH TO BE TL.
 - FOR REINF. THAT EXCEEDS 12m, THE LAPPING SHOULD BE DONE WHERE STRESS IS LESS. THE LAPPING OF TOP REINFORCEMENT SHOULD BE AWAY FROM SUPPORTS WHERE STRESS IS HIGH.
 - DENOTES ADDITIONAL REINFORCEMENT.
 - TRIMMER BARS FOR OPENINGS, REFER TO DWG. NO. 21.070/N2 FOR DETAILS.

BUILDING AND CONSTRUCTION, APPROVED UNDER SECTION 5 / SECTION BUILDING CONTROL ACT (CHAPTER

Project Ref No : A1252-00566-2022-ST19

for Commissioner of Building Control

PE'S CERTIFICATION



AC'S CERTIFICATION

ACCREDITED CHECKER

NO: 1089

KOK KING MIN
In AC Organisation
Registration No: A054
BUILDING CONTROL ACT
SINGAPORE

CONSTRUCTION SKETCH

ISSUED

19 SEPT 2025

CONSULTANTS PTE. LTD.

2	REVISED SLAB REINFORCEMENT	17/09/25
1	REVISED SLAB REINFORCEMENT	05/03/25
REV	AMENDMENTS	DR DES CHK DATE

PROJECT

PROPOSED NEW ERECTION OF 51 STOREY MIXED USE DEVELOPMENT COMPRISING 5 STOREY HOTEL AND CARPARK PODIUM, 9 STOREY HOTEL (350 ROOMS), 36/37 STOREY RESIDENTIAL FLATS (683 UNITS) AND 2 BASEMENTS ON LOTS 00483K AND 00484N TS 30 AND SUBTERRANEAN SPACE LOT 800772C TS 30 AT MARINA VIEW (DOWNTOWN CORE PLANNING AREA)

ARCHITECT

ARCHITECT 61 PTE. LTD.




KTP Consultants Pte Ltd
Surbana Jurong Campus 38 Cleantech
Loop, #01-31 Singapore 638741
Tel : +65 6248 1288

DRAWN: CH DATE: DESIGNED: JS/AP/FS
SCALE: 1:150 CHECKED: ChewAL

DWG. NO. 21.070/L17S2

LEVEL - 17 TO L33, L36 TO L48 TYPICAL SLAB BOTTOM REINFORCEMENT LAYOUT

THE OWNERSHIP OF THE COPYRIGHT IN THIS DRAWING IS RETAINED BY KTP CONSULTANTS WHOSE CONSENT MUST BE SOUGHT BEFORE ANY USE OR REPRODUCTION OF THE DRAWING OR ANY PART THEREOF CAN BE MADE.

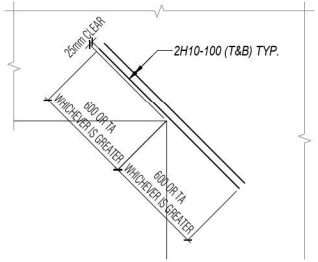

TYPICAL TRIMMER BARS AT RE-ENTRANT CORNER

SCALE : 1:25

LEVEL - 17 TO L33, L36 TO L48 TYPICAL SLAB BOTTOM REINFORCEMENT LAYOUT

SCALE : 1:150



TECHNICAL
WOH HUP (PRIVATE) LIMITED
MARINA VIEW RESIDENCES (MVR)

1. PD - Chen Han Qi
2. PM - Wong Wei Siong
3. SE
4. RE/RTO
5. All Subcons
6. MVR WH, MVR Site
7. WH QS
8. WH Rebar Scheduler
9. DC
10. IOI - Muliadi, How See, Darren

From: Joseph Chin
24-Dec-25



TYPICAL PBU TYPE 5w.M

SCALE : 1:15

EXTRACTED FROM ST19 BCA APPROVED DRAWING

1. All trimmer bars shall be H16 (T&B).
2. Starter bars provision for H16 trimmer bars from RC walls shall all be H13.
3. If trimmer bars anchored into beam or wall shall be 12D. All other cases shall be minimum TA.

KTP: No objection
KTP|KERKYX 20250828

